


THANK YOU

keerthish.g.durai@gmail.com
+91 91083 54056

PORTFOLIO

KEERTHISH G
SELECTED WORKS 2024-2026

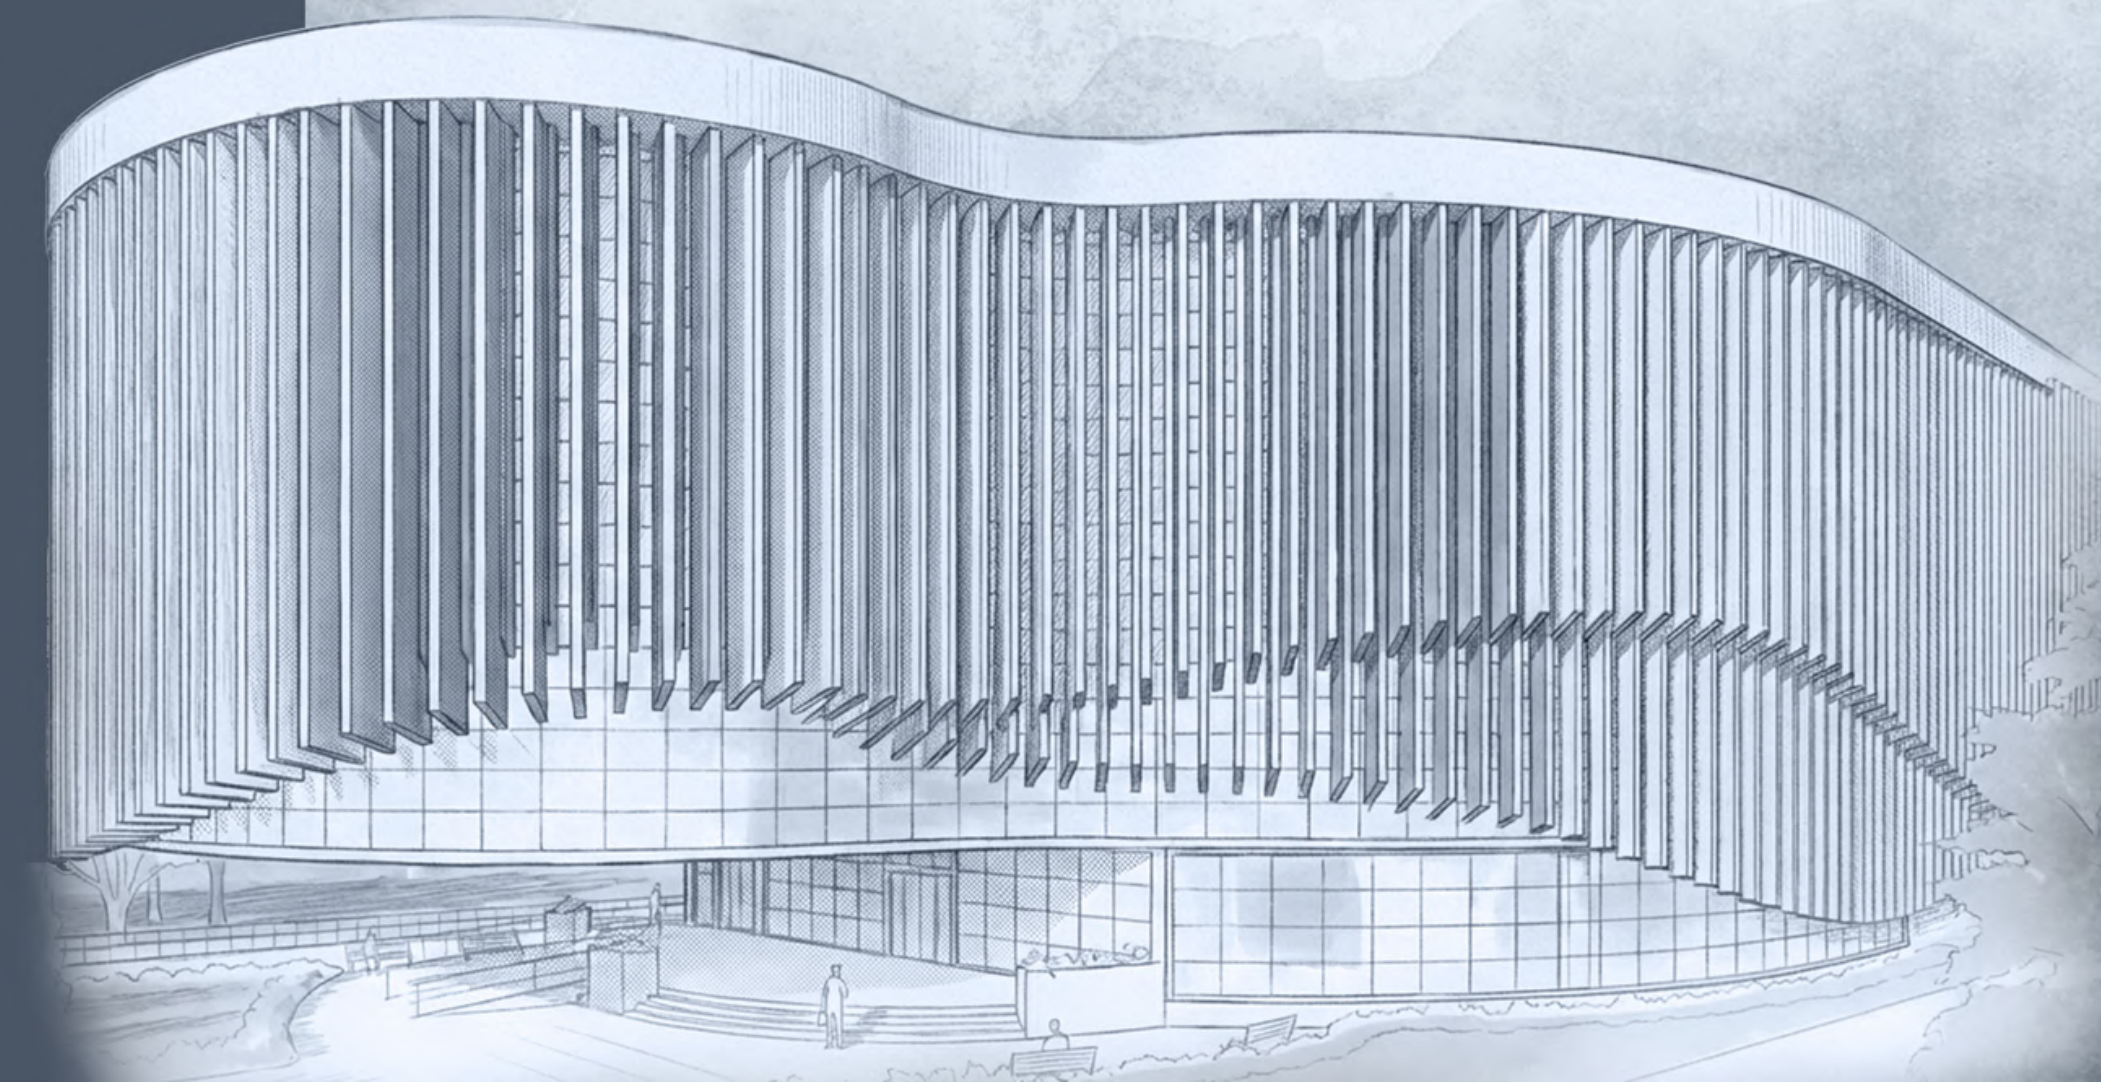




KEERTHISH G DURAI

06/10/2003
Bangalore, Karnataka

I am interested in Architecture as a process of organizing complexity into clear, functional spaces. My design approach is rooted in technical master planning and functional floor layouts that respond to program, circulation, and site conditions. I enjoy working across scales, from developing comprehensive master plans to resolving efficient and purposeful spatial layouts.

Through a balance of creativity and technical clarity, I aim to design architecture that is thoughtful, efficient, and meaningful, while continuously learning and refining my approach.

(+91) 91083 54056
keerthish.g.durai@gmail.com
@keerthish_g
<https://www.linkedin.com/in/keerthish-g>

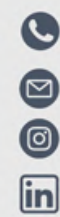


EDUCATION

- 2019 & 2021 **10th & 12th Grade**
Kendriya Vidyalaya RWF, Yelahanka, Bangalore
- 2021 - 2016 **Bachelor of Architecture**
SOA, Ramaiah Institute of Technology, Bangalore

CERTIFICATION


- National Award Competition For Innovative Use of Steel in Architecture , INSDAG , 2024
- Interior Design Competition, Transperence Bridge Master, 2024

SOFT SKILLS

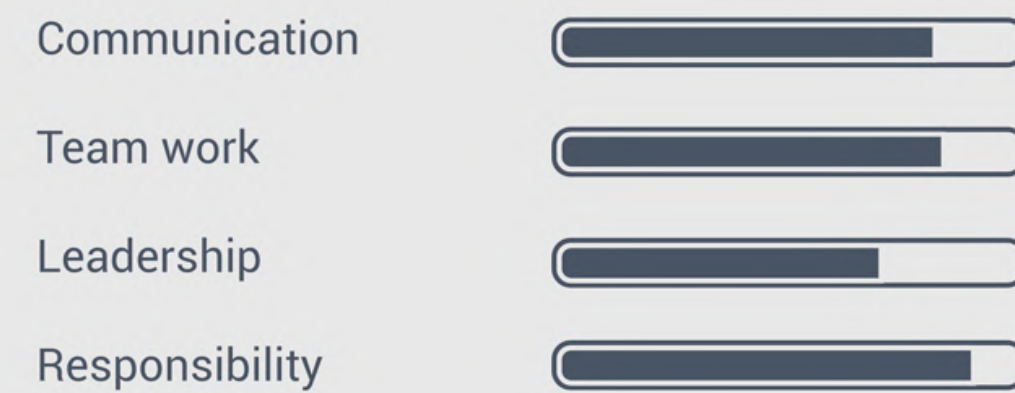

SOFTWARE SKILLS

BIM | Drafting

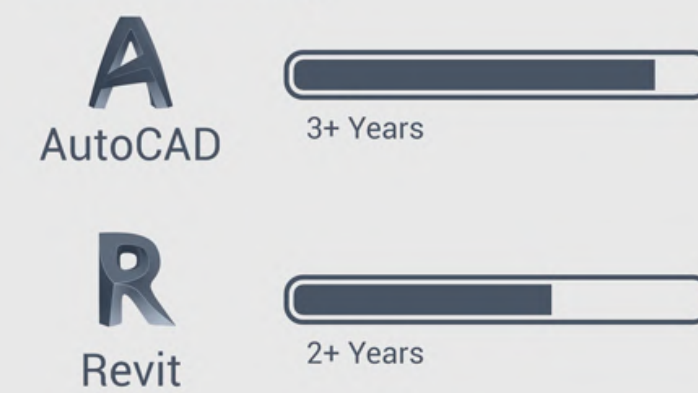

3D modelling



LANGUAGE

- English - Fluent
- Hindi - Fluent
- Tamil - Native
- Kannada - Fluent

EXPERIENCE

- buildAhome Pvt Ltd
[6 months]
Role : Architect Intern



INTEREST



Music



Travelling



Reading Fiction



Sketching



Photography



Gaming

Visualisation




Post Production | Presentation



CONTENT

01

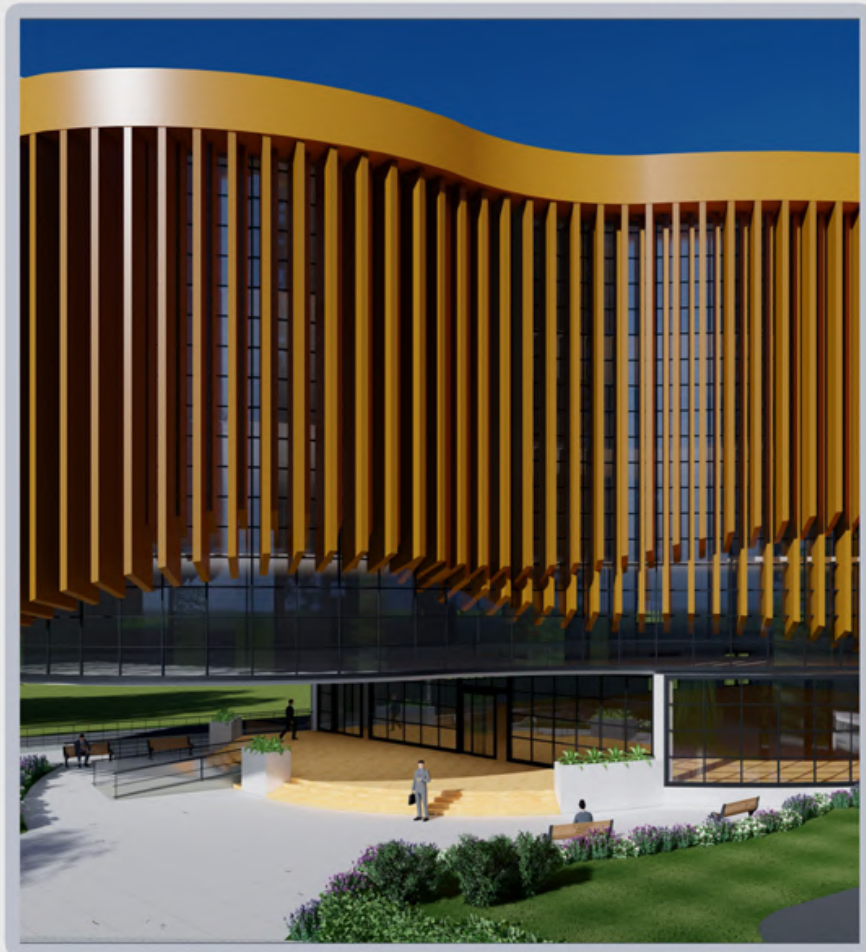

CIVIC SQUARE
Pg no : 5-10

02




LITHOS - MUSEUM
Pg no : 11-18

03



INTERNSHIP WORK
Pg no : 19-46

04

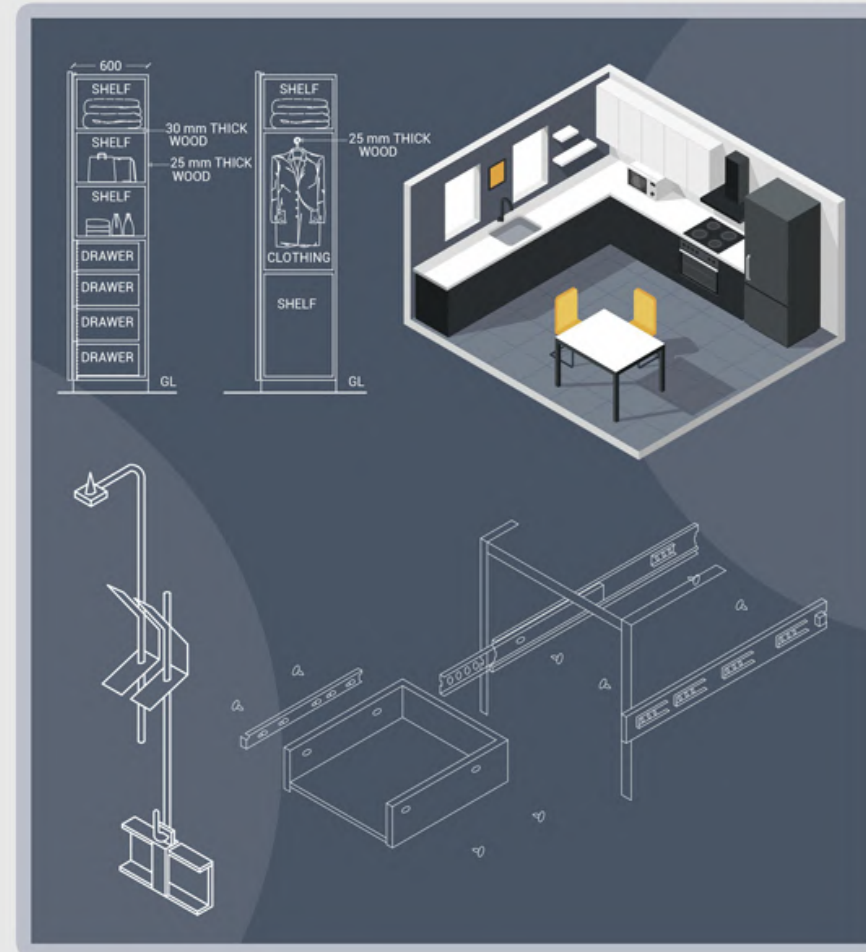


BMCT
Pg no : 47-50

05



MISCELLANEOUS
Pg no : 51-52

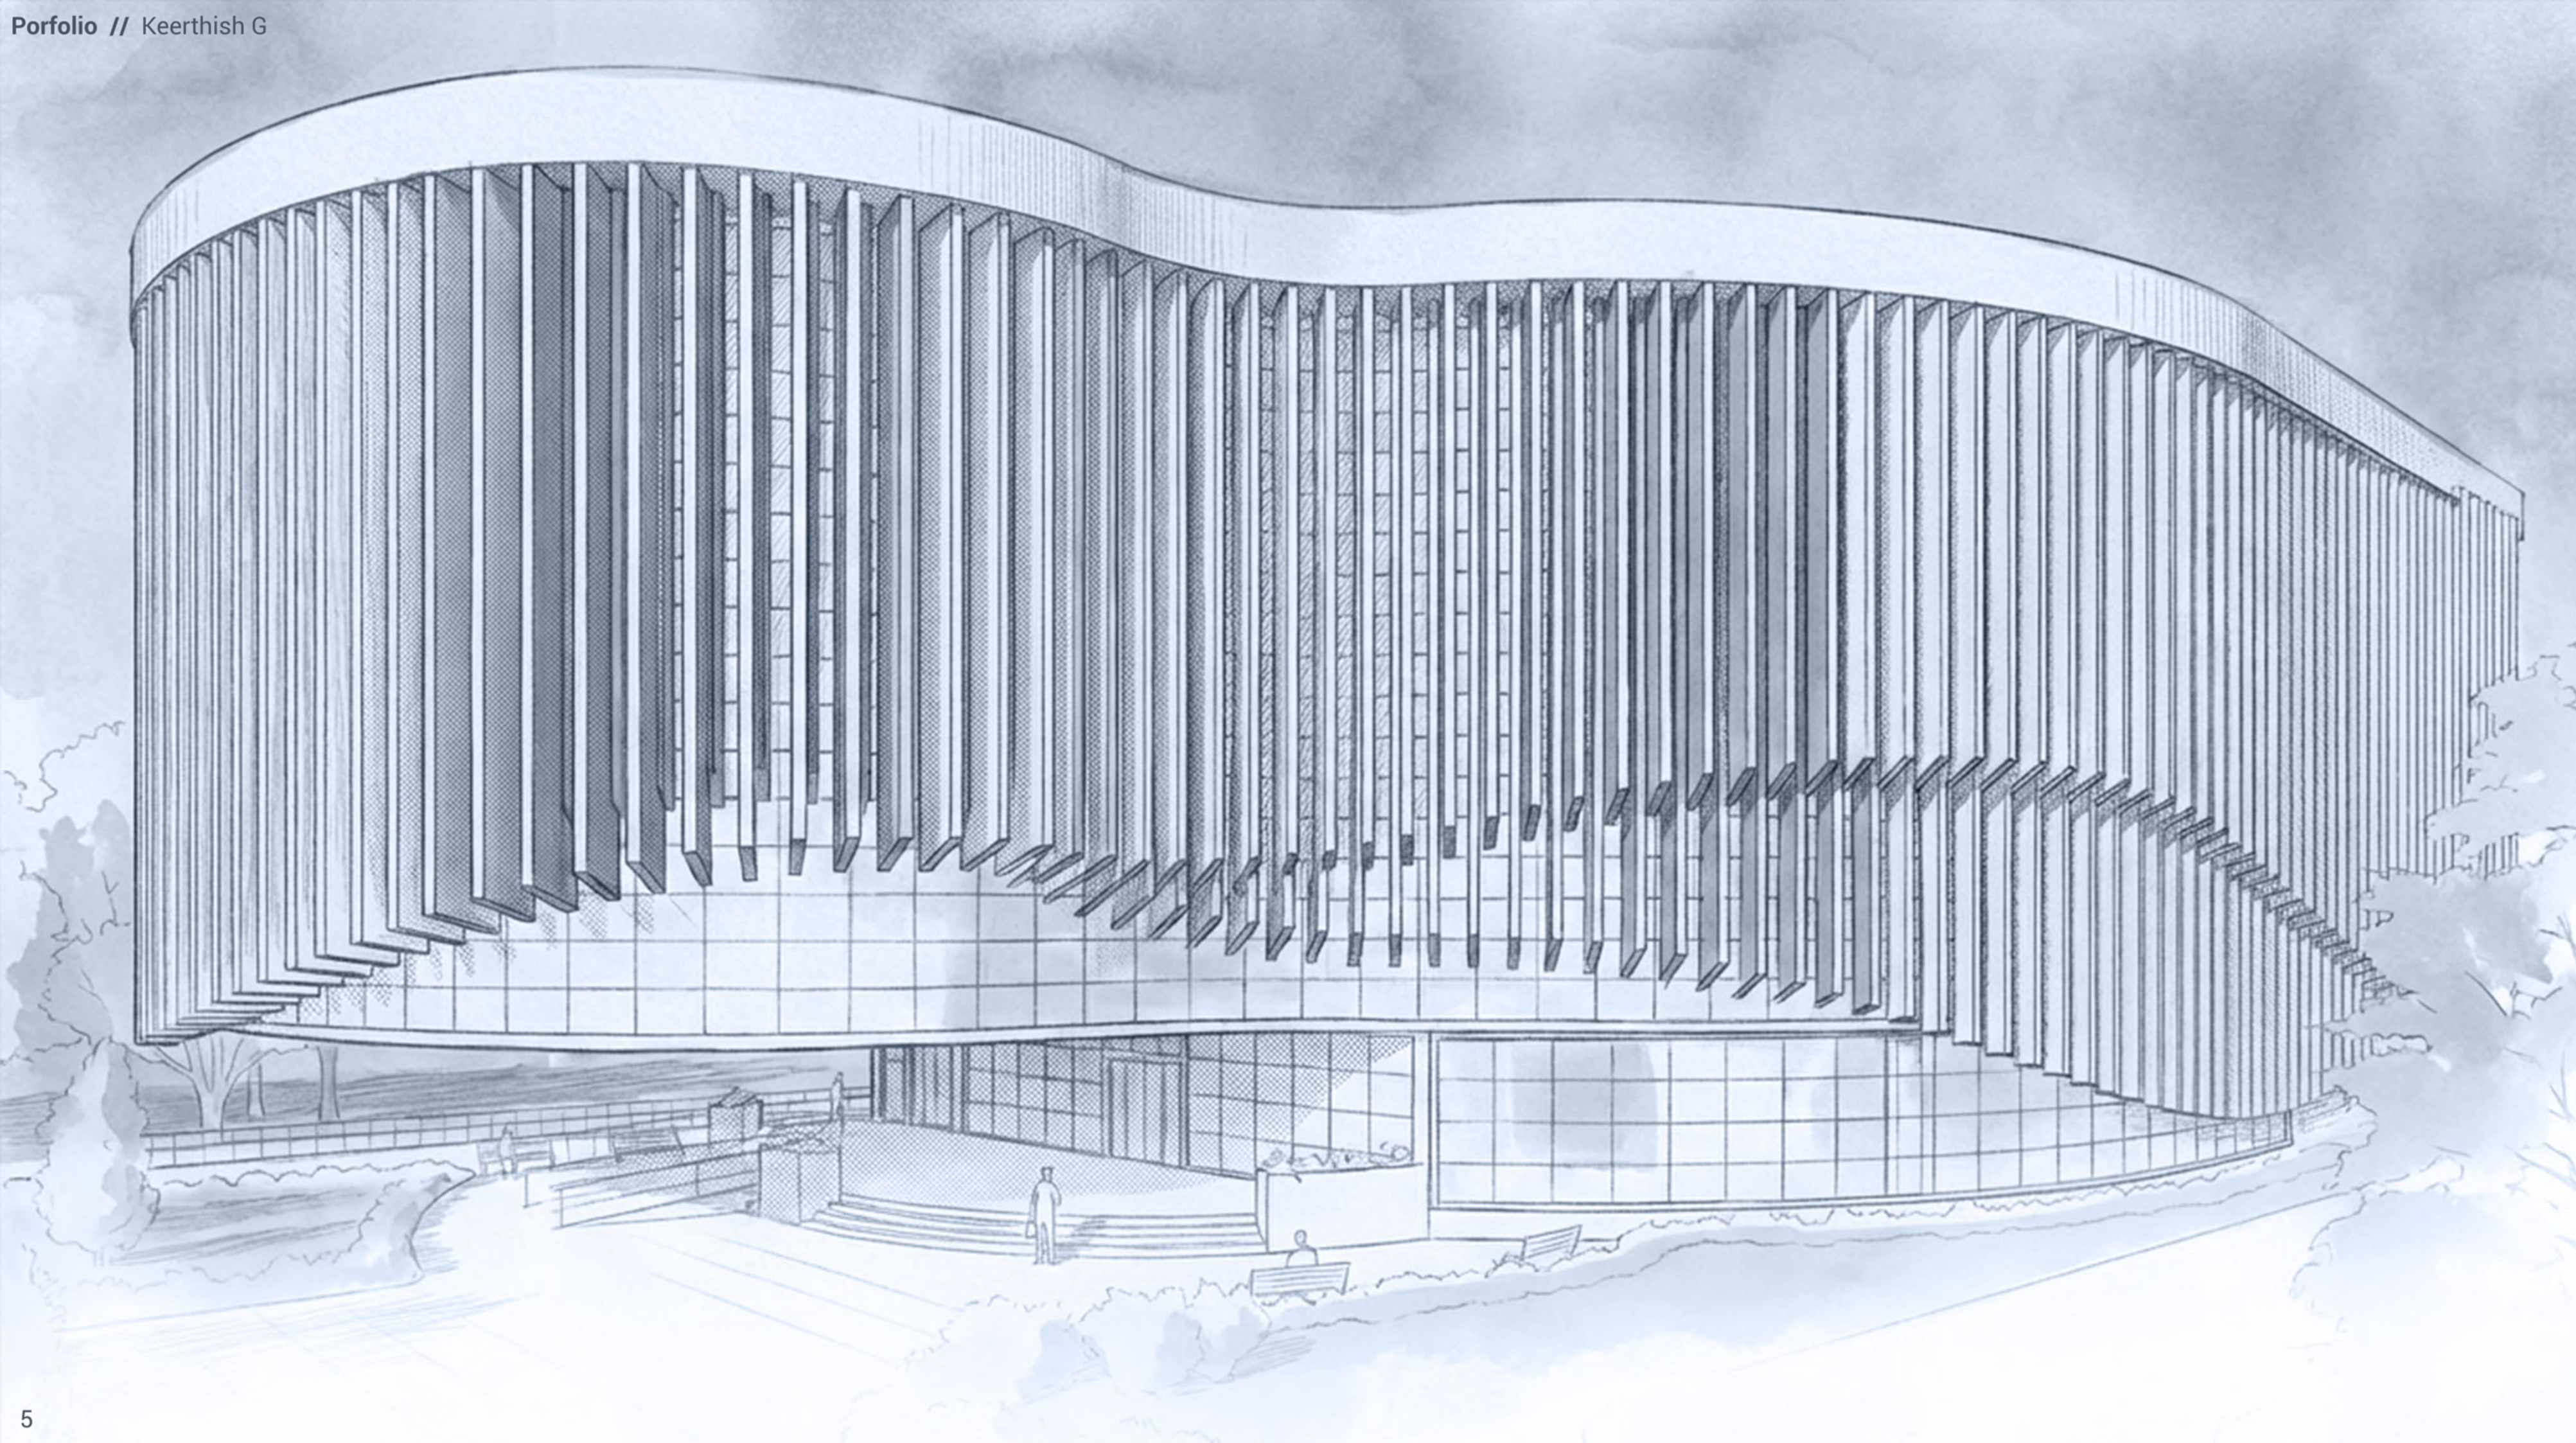

01

CIVIC SQUARE

Project : Civic Centre

Semester : S7

Site : RT Nagar, Bangalore

Site Area : 3885 sqm (0.96 acres)

The proposed Civic Center is envisioned as a vibrant community hub that integrates essential public services with spaces for social, cultural, and recreational engagement. Designed for RT Nagar, the complex brings together a Basic Health Care Block and a multifunctional Club House that includes a function hall, gym, and various recreation facilities. The project aims to create an accessible and inclusive civic landmark that supports everyday well-being, fosters community interaction, and enhances the quality of life for residents through thoughtful architecture and responsive public infrastructure.

CONTEXT

RT Nagar developed as part of the planned growth of Bangalore, with a focus on residential areas. RT Nagar continued to grow as a residential and commercial hub.




There is an existing building on the site, which is BDA Shopping Complex (Government office). The redevelopment of the BDA Shopping


Complex North presents a unique opportunity to create a vibrant mixed-use destination that caters to the evolving needs of the surrounding community.

KINETIC ARCHITECTURE


Kinetic facades merge aesthetics, functionality, and sustainability, redefining architectural innovation. Their ability to adapt to environmental changes not only improves energy performance but also enhances user experience, making them a focal point in modern and future architecture.

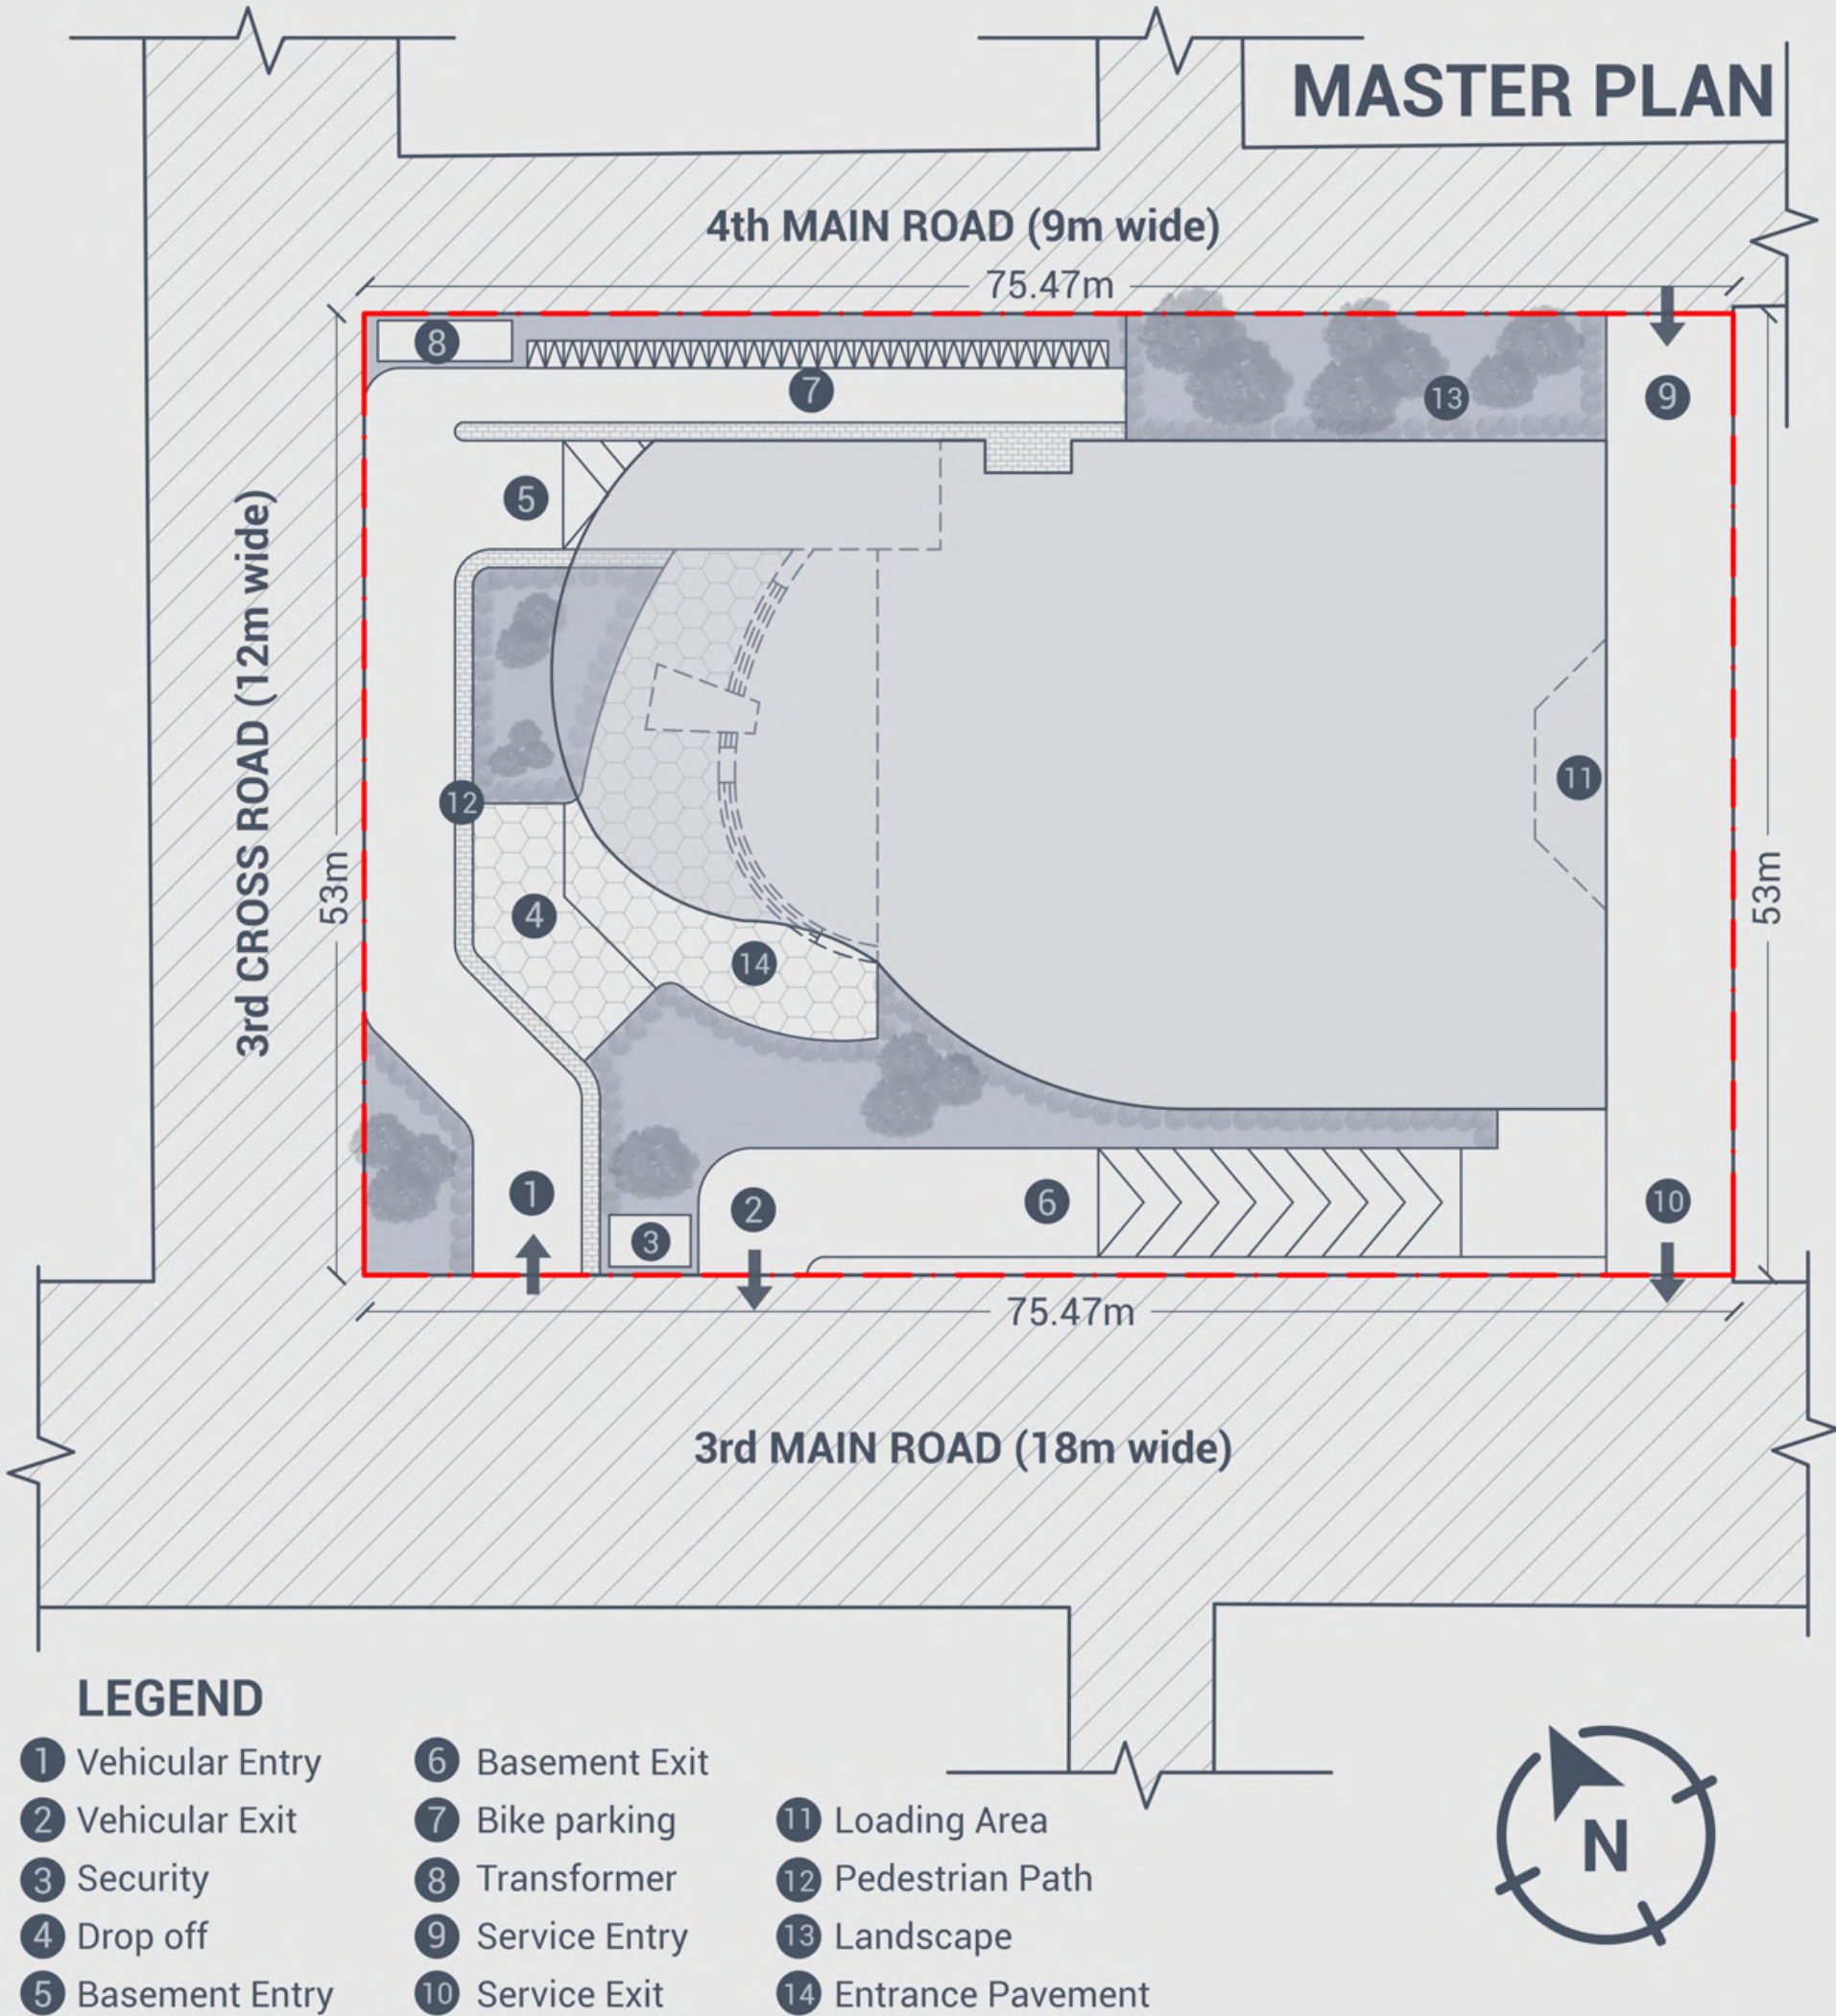


GROUND FLOOR PLAN

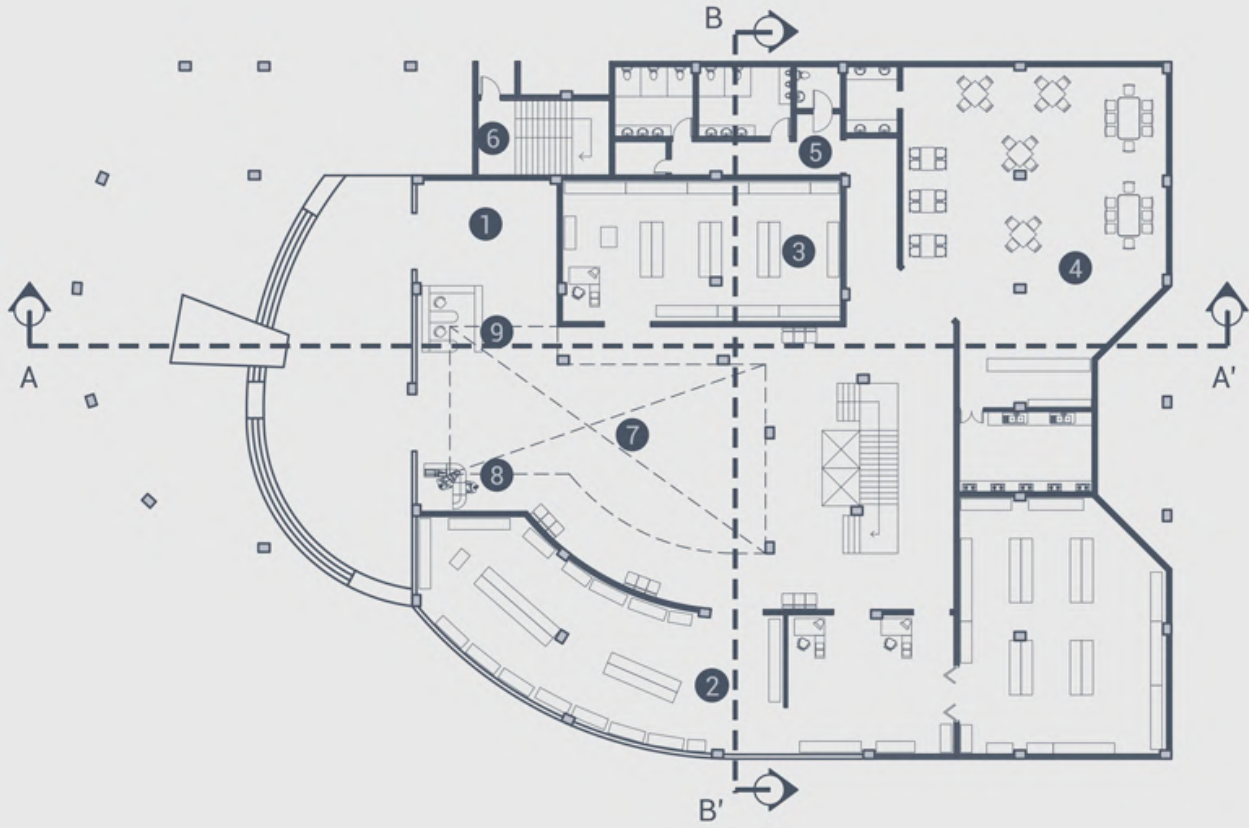


1st FLOOR PLAN

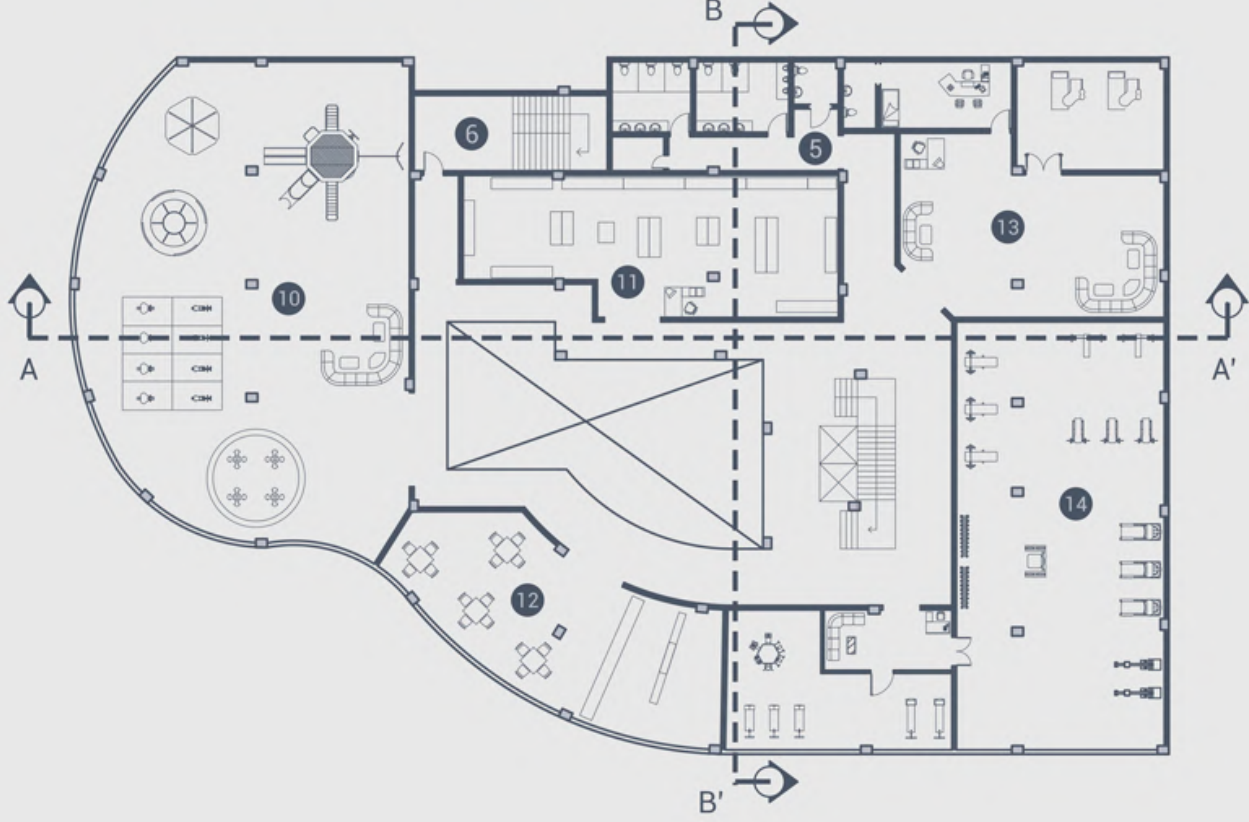

BASEMENT PLAN

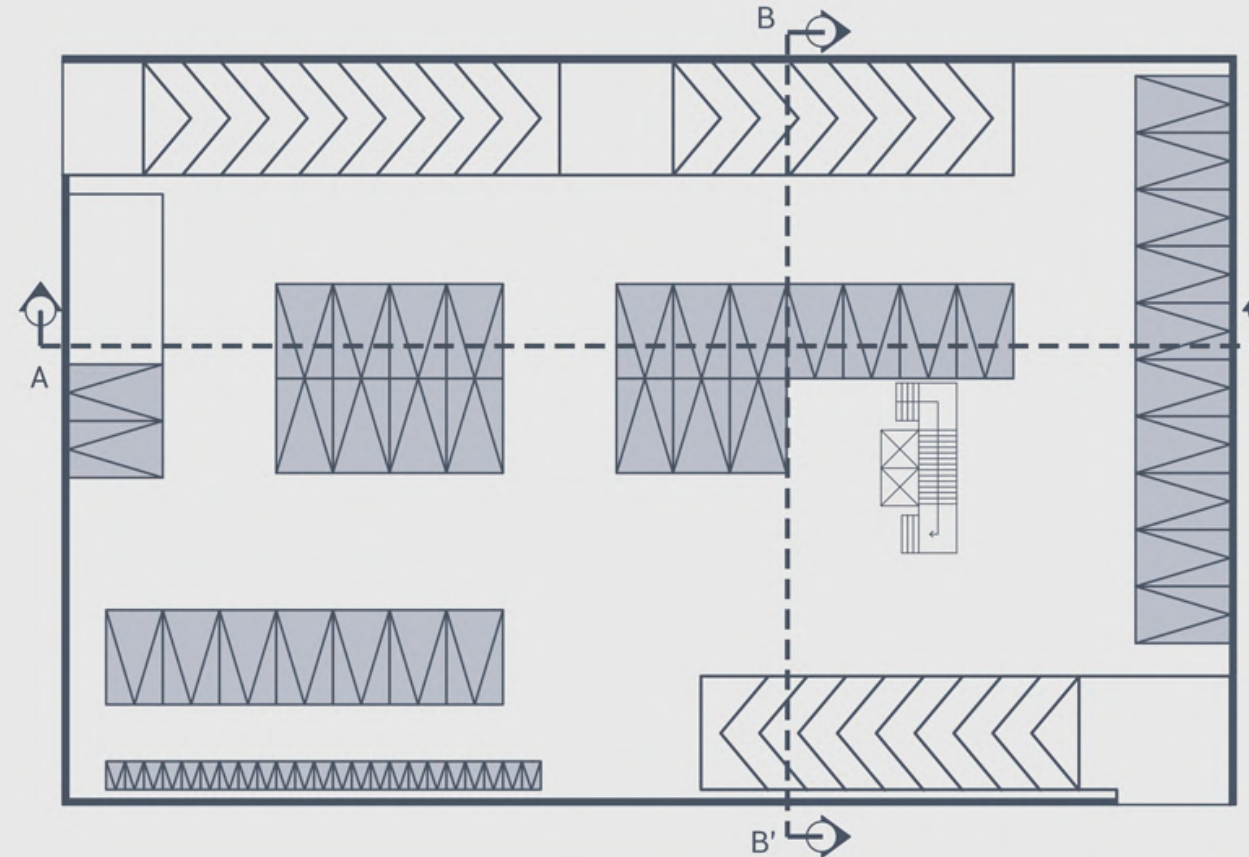

2nd FLOOR PLAN

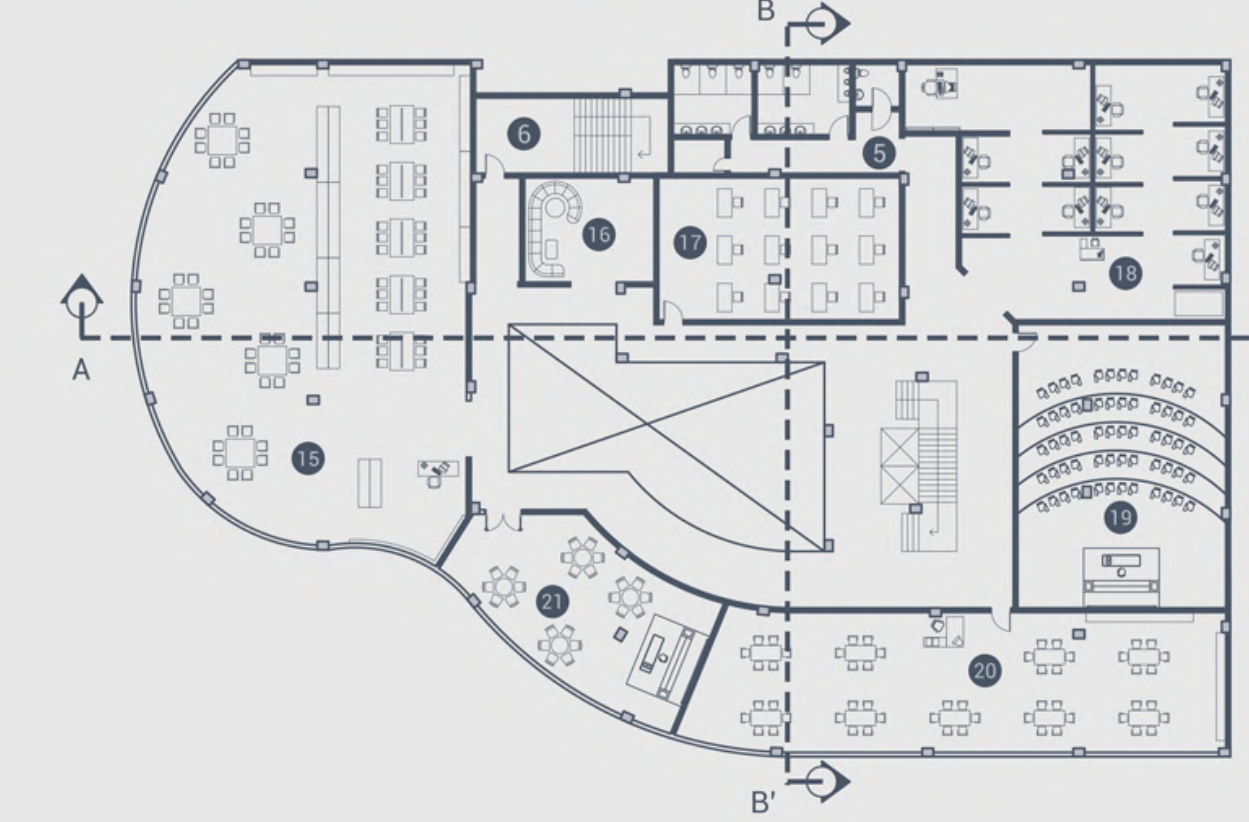


LEGEND


- | | |
|---------------------------|---------------------|
| 1 Entrance | - 60m ² |
| 2 Shopping Mart | - 400m ² |
| 3 Book Store | - 120m ² |
| 4 Restaurant | - 300m ² |
| 5 Toilet | - 70m ² |
| 6 Fire exit | - 30m ² |
| 7 Lobby space | - 220m ² |
| 8 Helpdesk | |
| 9 Lift & stairs | - 40m ² |
| 10 Kids Play Area | - 400m ² |
| 11 Retail Store | - 120m ² |
| 12 Cafe | - 140m ² |
| 13 Health Clinic | - 210m ² |
| 14 Fitness & Gym | - 340m ² |
| 15 Library | - 400m ² |
| 16 Waiting Area | - 120m ² |
| 17 Self Study Area | - 100m ² |
| 18 Cyber Cafe | - 210m ² |
| 19 Coaching Class | - 170m ² |
| 20 Group Study Area | - 210m ² |
| 21 Children Learning Area | - 100m ² |



3rd FLOOR PLAN


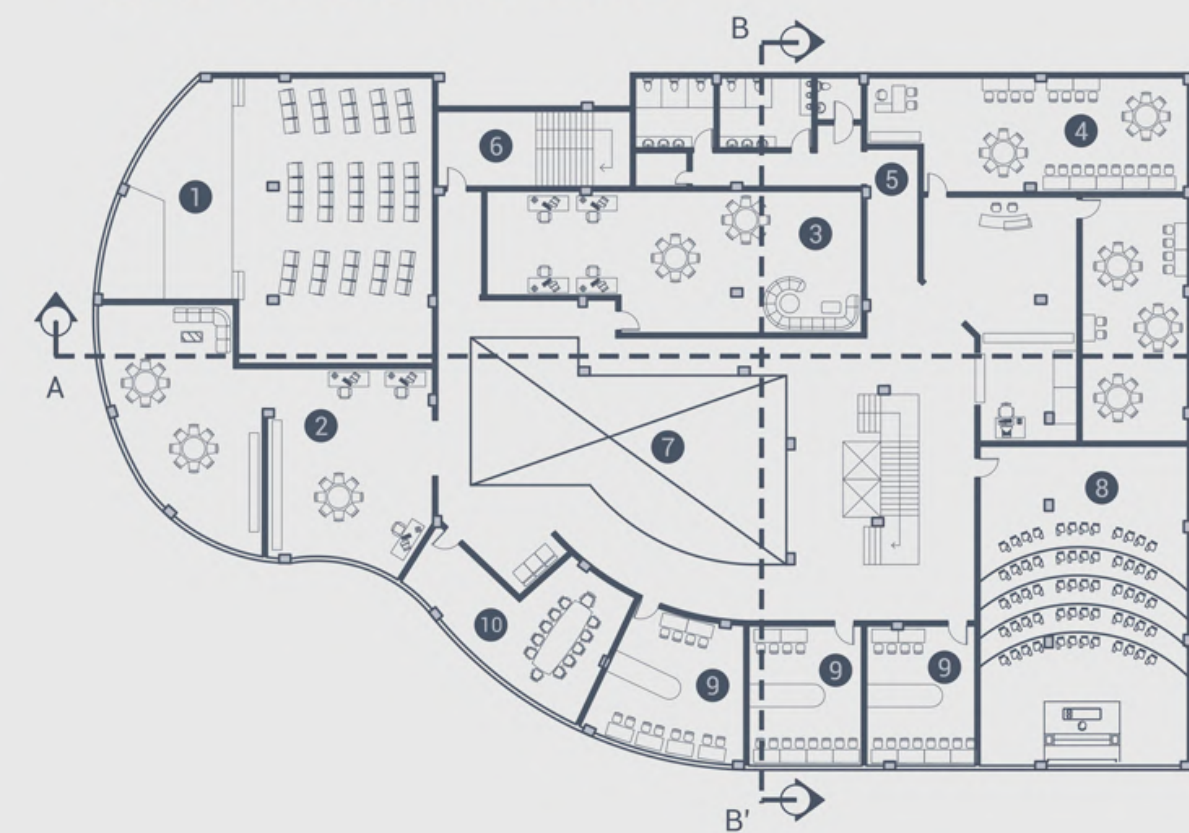


4th FLOOR PLAN

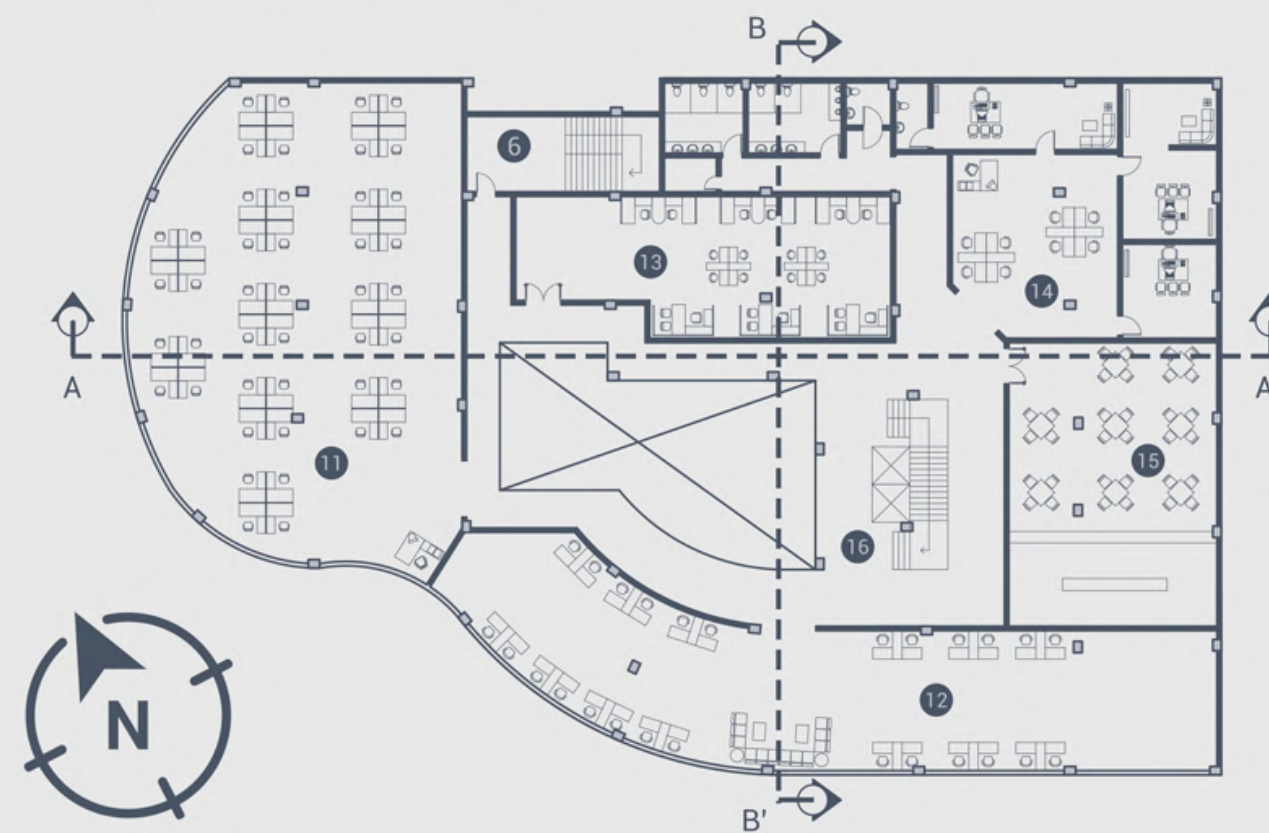

LEGEND

- | | | |
|----|------------------|---------------------|
| 1 | Party Hall | - 220m ² |
| 2 | Studio 1 | - 90m ² |
| 3 | Studio 2 | - 130m ² |
| 4 | Workshop | - 90m ² |
| 5 | Toilet | - 70m ² |
| 6 | Fire exit | - 30m ² |
| 7 | Lobby space | - 220m ² |
| 8 | Job Training | - 200m ² |
| 9 | Workshop | - 50m ² |
| 10 | Meeting Hall | - 80m ² |
| 11 | Co-working Space | - 400m ² |
| 12 | Govt Office | - 320m ² |
| 13 | Co-working Space | - 130m ² |
| 14 | Admin Office | - 200m ² |
| 15 | Canteen | - 170m ² |
| 16 | Lift & stairs | - 40m ² |

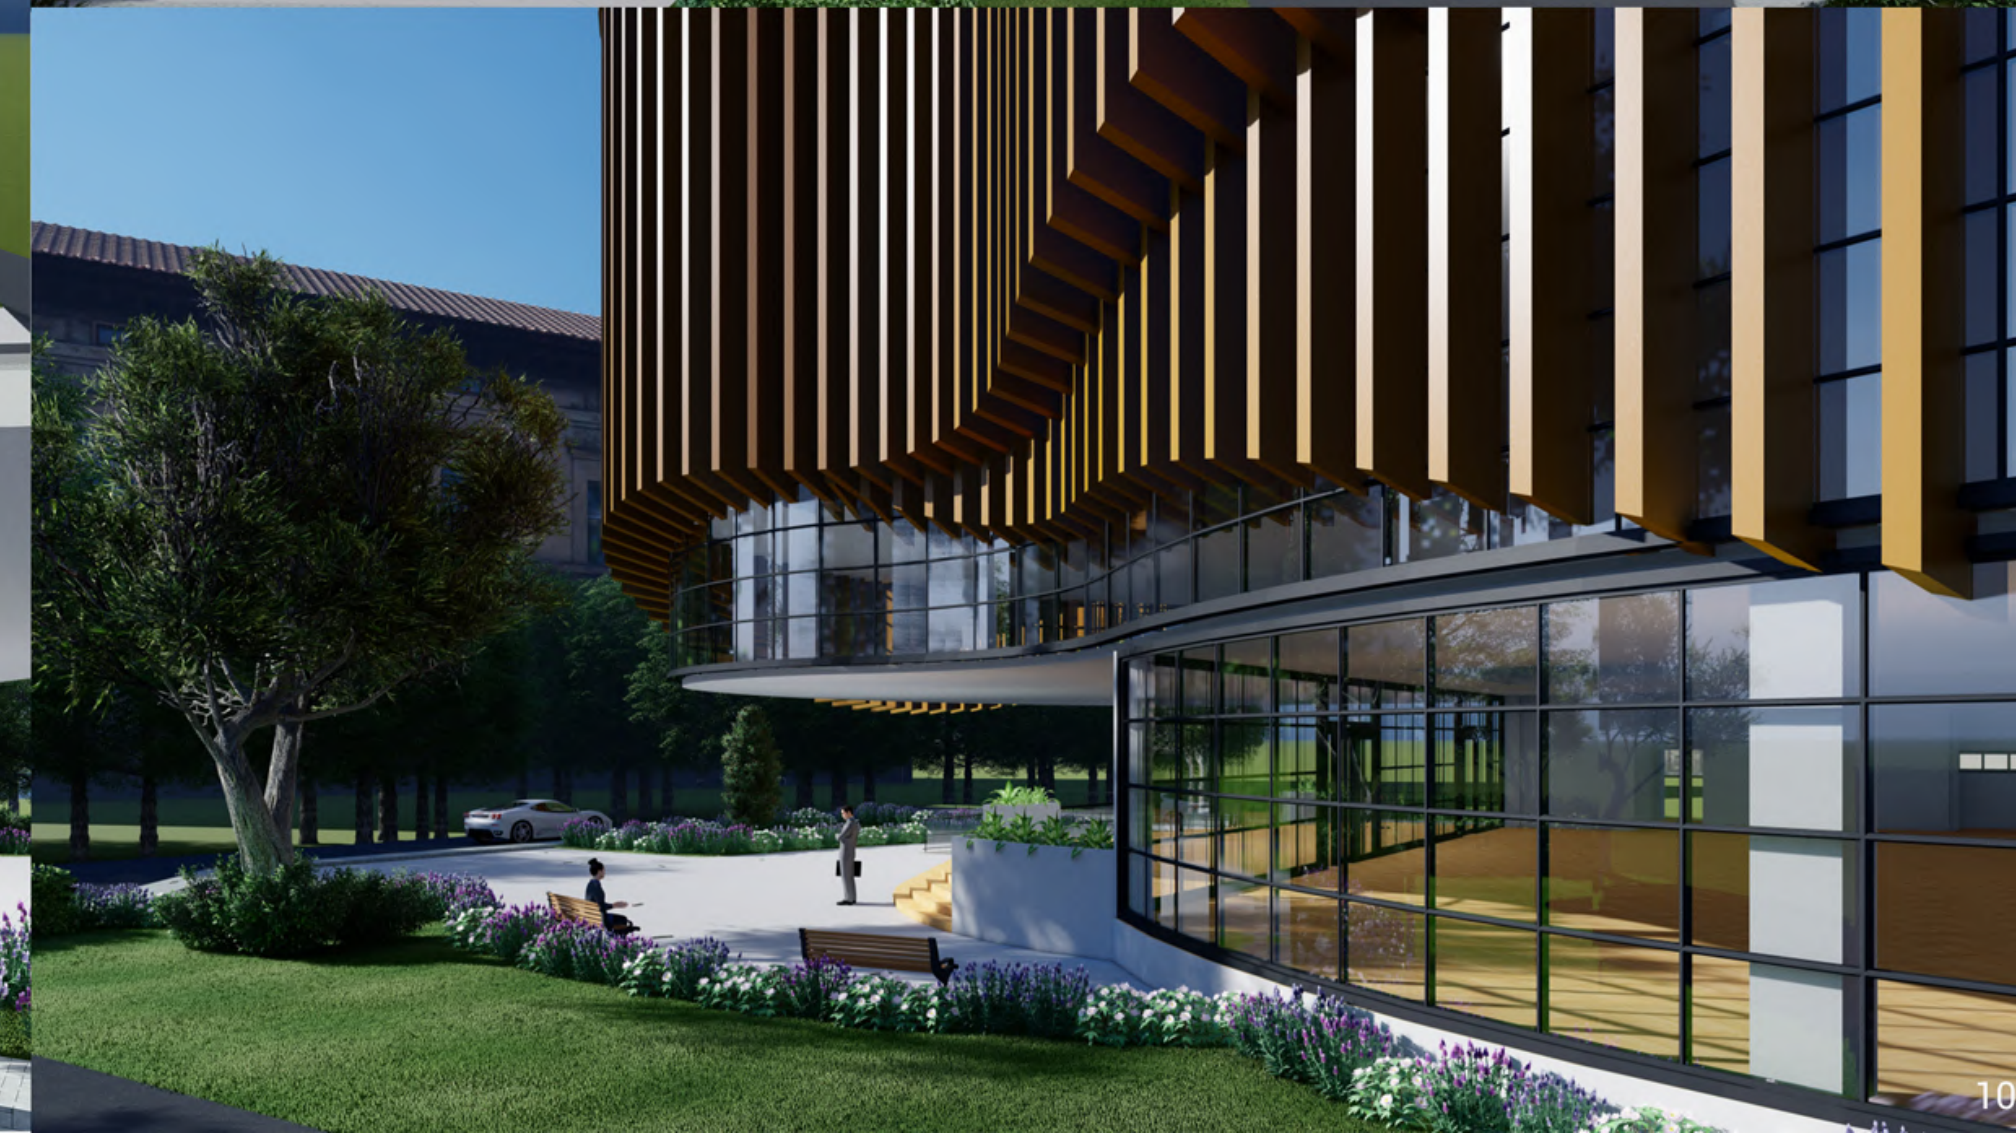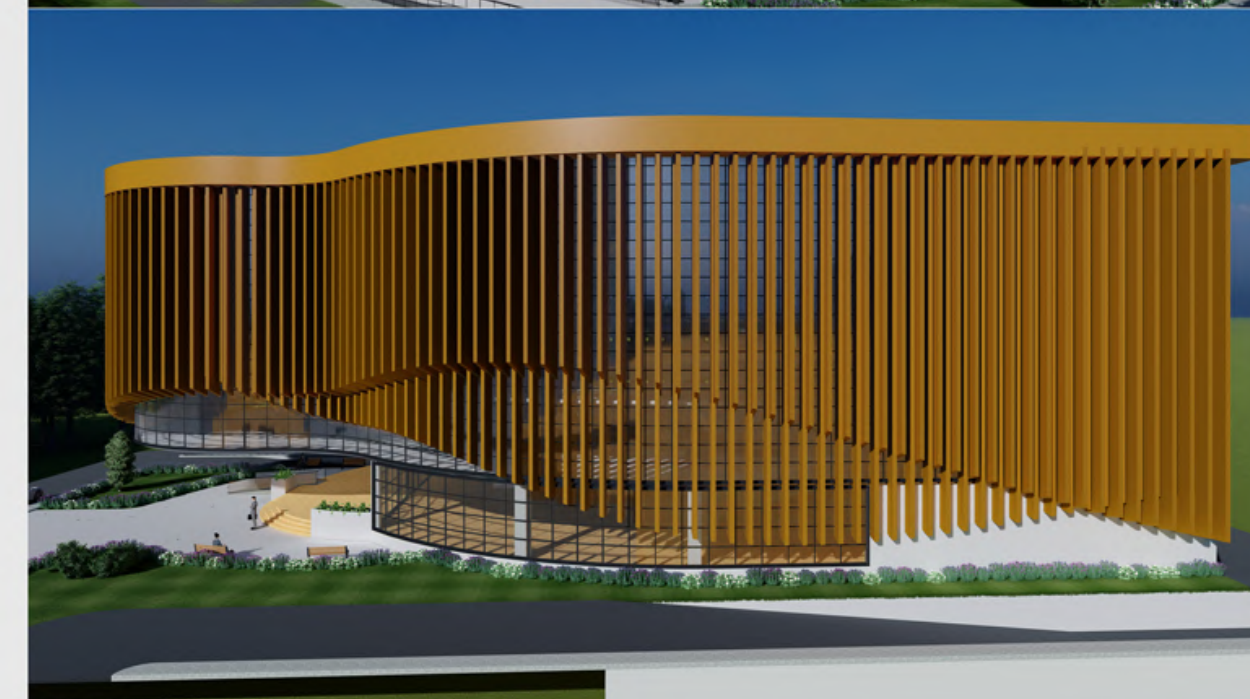



02 LITHOS - MUSEUM

Project : Geology Museum

Semester : S9

Site : Sadahalli, Bangalore

Site Area : 35100 sqm (8.66 acres)

Lithos – Museum of Geology, is conceived as a public educational institution that explores the Earth's geological history through architecture and spatial narrative. The museum integrates exhibition, research, and learning spaces to translate geological processes such as layering, formation, and transformation into an immersive built experience. Envisioned as both a knowledge center and a civic landmark, the project seeks to promote scientific awareness while engaging the public through meaningful architectural expression.

CONTEXT


The project reimagines the abandoned quarries of Sadahalli as a living geological classroom and cultural landmark, conserving exposed rock formations while transforming a hazardous landscape into a safe, accessible public environment. Through phased stabilisation, adaptive exhibition spaces, outdoor geology trails, and ecological restoration using native landscapes and water systems, the proposal aims to enhance geological literacy, support education and research, and create long-term community and ecological value within the constraints of terrain, access, and regulatory frameworks.




BRUTALISM

Brutalism is an architectural style that emphasizes raw materiality, structural honesty, and sculptural massing. Originating in the mid-20th century, the style derives from the French term *béton brut*, meaning raw concrete. Brutalist architecture celebrates unadorned surfaces, exposed construction, and bold geometric forms, making it conceptually aligned with themes of earth, rock, and geological permanence.


FORM DEVELOPEMENT

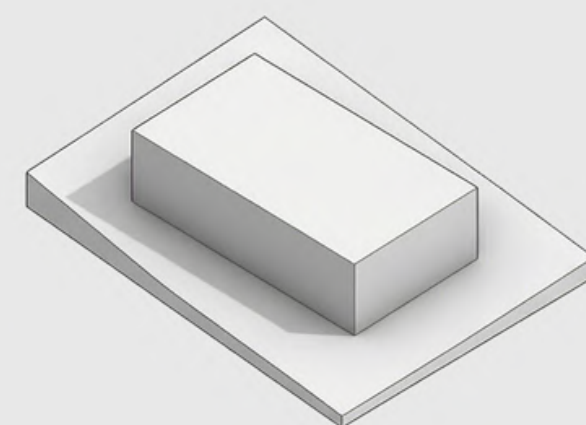


SITE + PRIMARY MASS

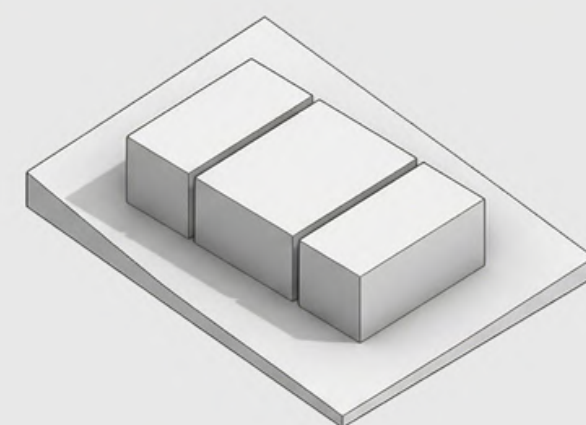


MASS SEGMENTATION

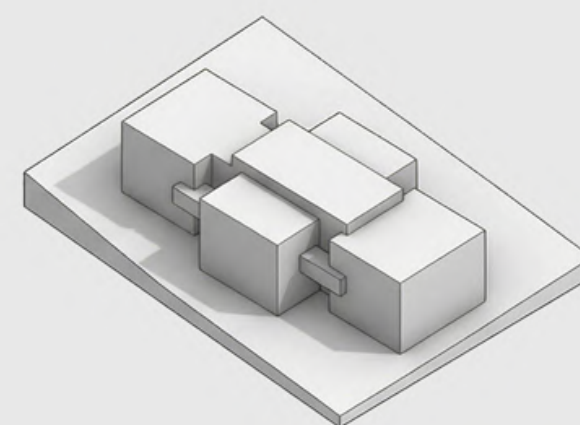


INTERCONNECTED BLOCKS

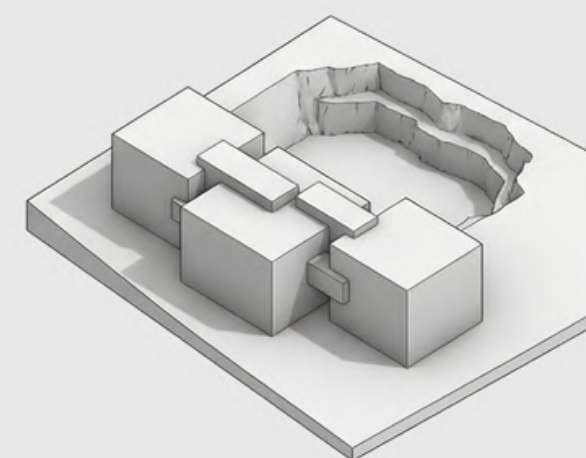

ARTIFICIAL QUARRY FORMATION

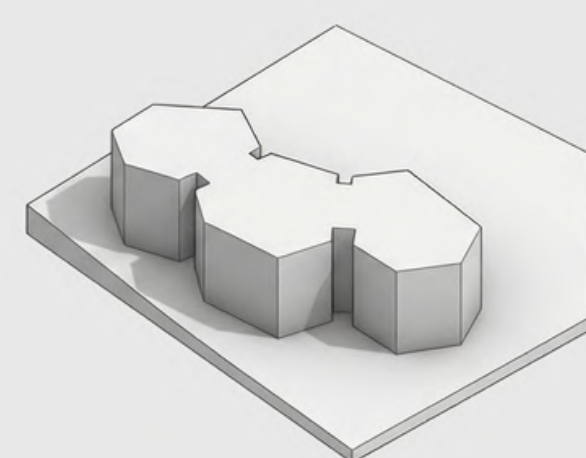


FORMAL REFINEMENT

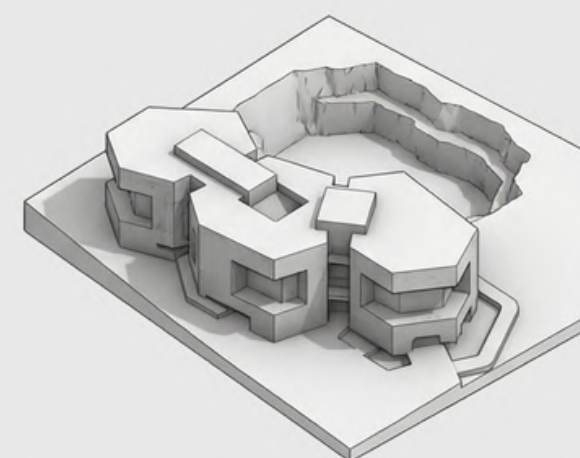

BRUTALIST ARCHITECTURAL ARTICULATION


MASTER PLAN

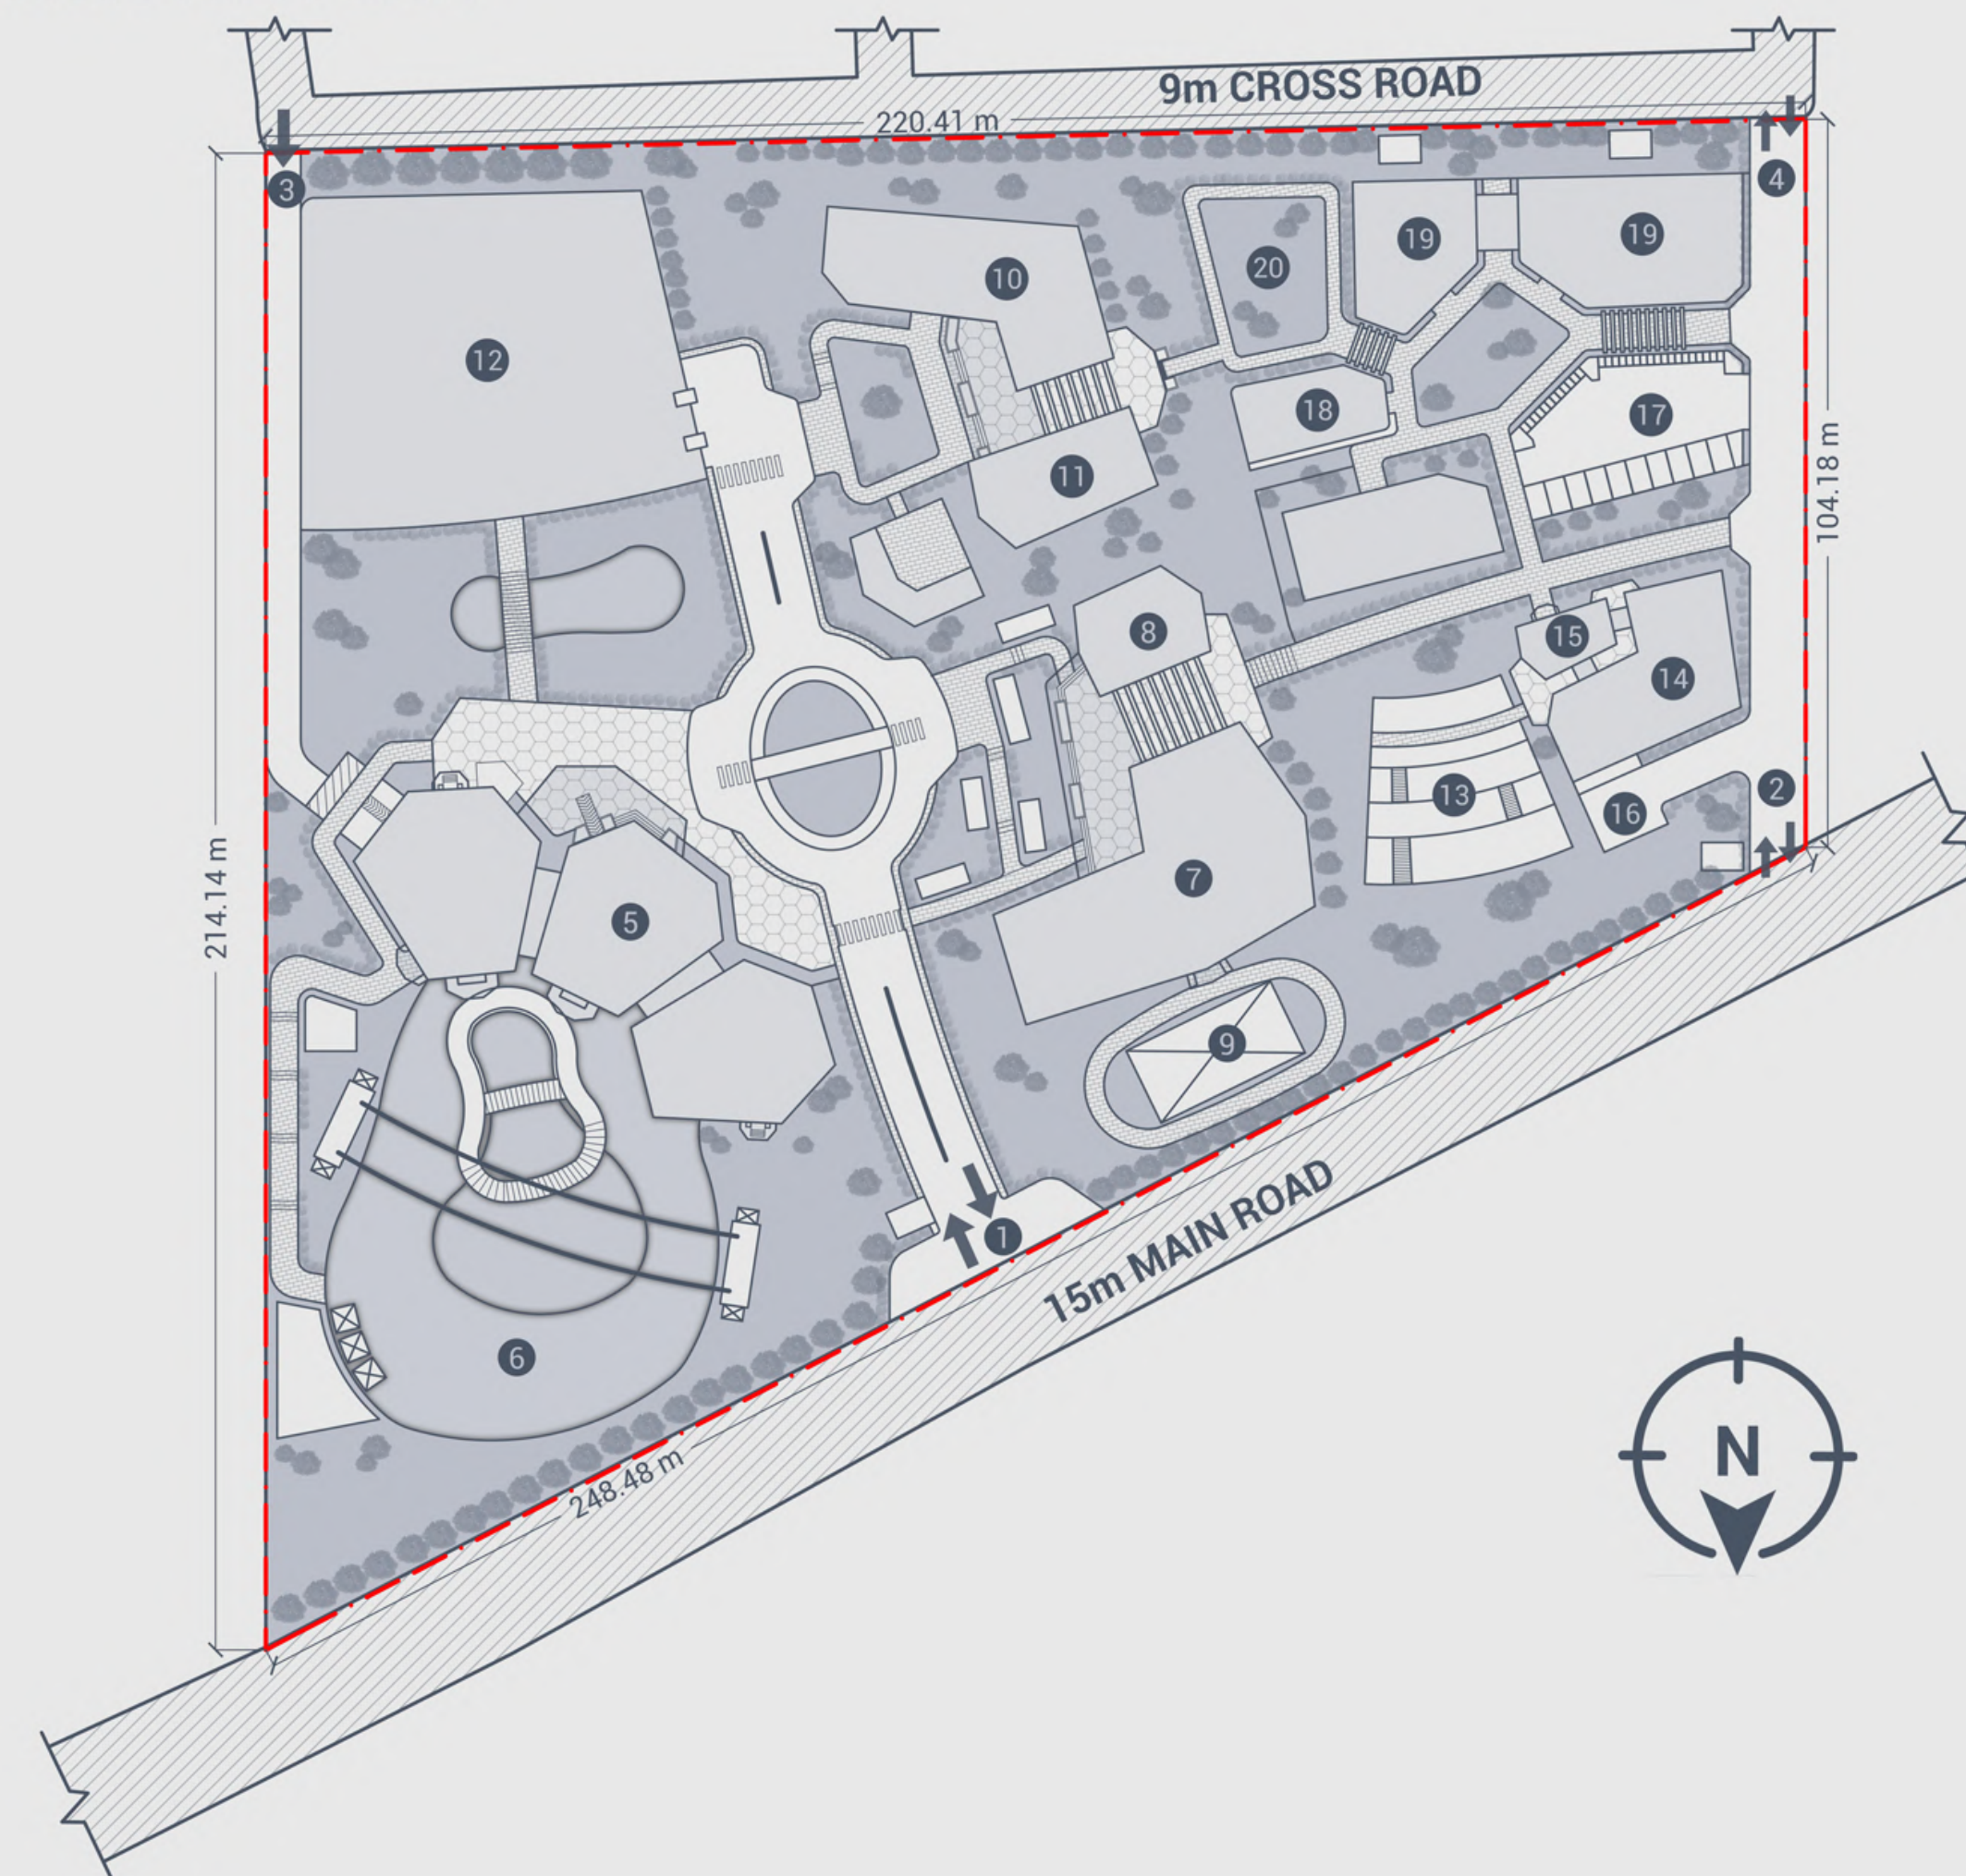


LEGEND

- 1 Public Entry/Exit
- 2 Private Entry/Exit
- 3 Service Entry/Exit
- 4 Residence Entry/Exit
- 5 Museum
- 6 Artificial Quarry
- 7 Immersive Theatre
- 8 Cafe
- 9 Watch Tower
- 10 Learning Centre
- 11 Library
- 12 Parking (MLCP)
- 13 R&D Centre
- 14 Storage
- 15 Sorting & Open Research
- 16 Loading Zone
- 17 Parking
- 18 Residence
- 19 Staff Quarters
- 20 Park

GROUND FLOOR PLAN

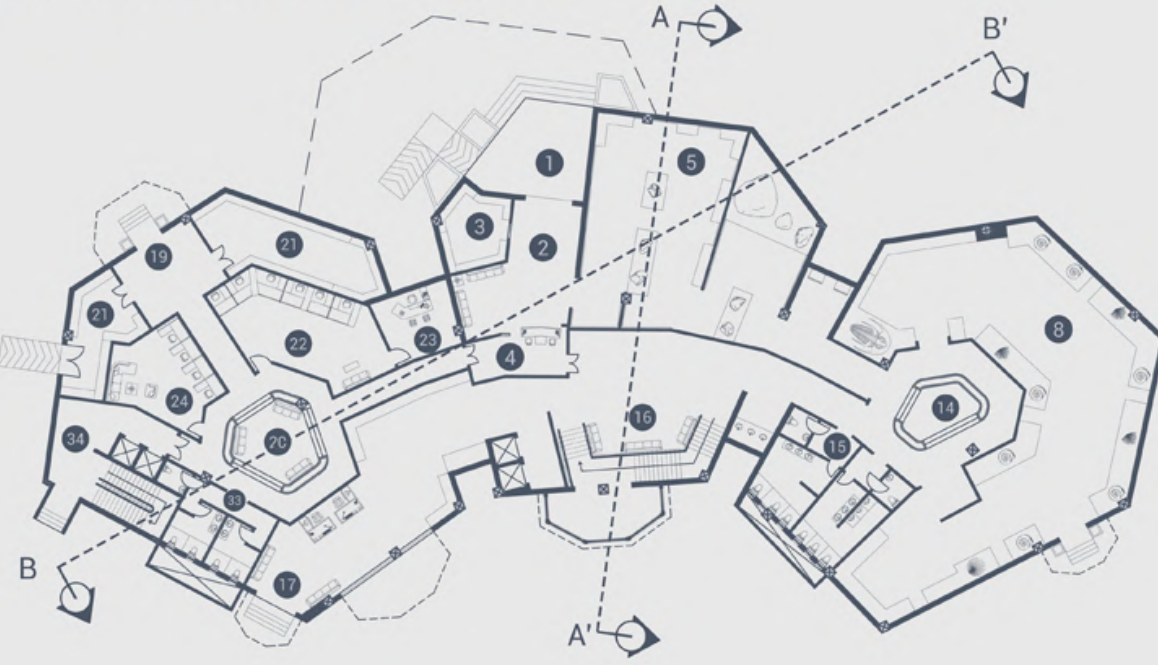


BASEMENT PLAN

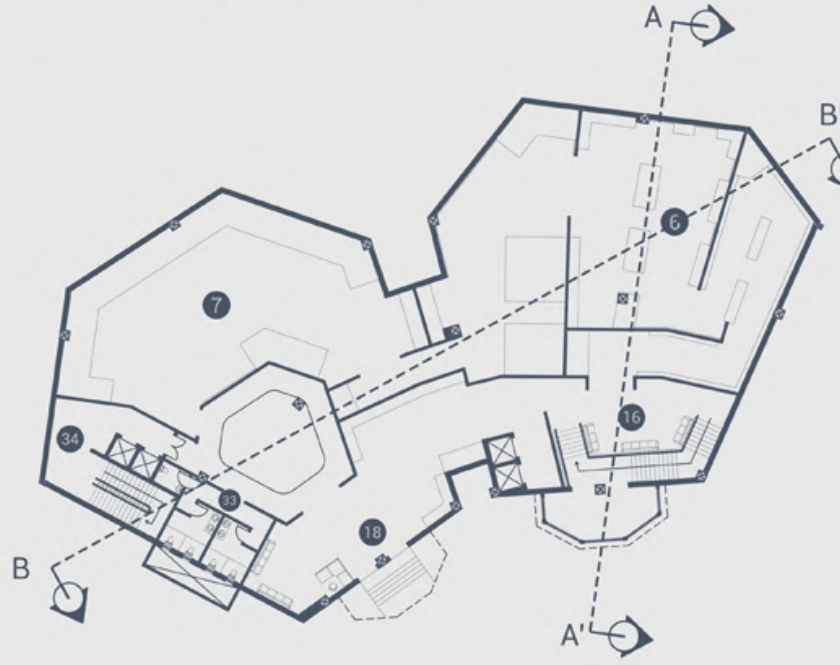


LEGEND

PUBLIC SPACE		ADMIN SPACE	
1	Main Entry	19	Main Entry/Exit
2	Entrance Lobby	20	Lobby Space
3	Luggage Counter	21	Storage
4	Ticketing Counter	22	Accounts
5	Geology & Stone Display	23	Manager
6	Regional Geology	24	Staff Resting
7	Fossil & Mineral Gallery	25	Pantry
8	Fossil & Mineral Display	26	Dining Area
9	Evolution Display	27	Electrical
10	Interactive Zone	28	AHU
11	Gemstone & Crystal Display	29	Conference Room
12	Mining Display	30	Security
13	Temporary Exhibits	31	Staff Office
14	Lobby Space	32	Manager
15	Toilet	33	Toilet
16	Lift Lobby	34	Lift Lobby
17	Main Exit		
18	Exit to Quarry		

1st FLOOR PLAN

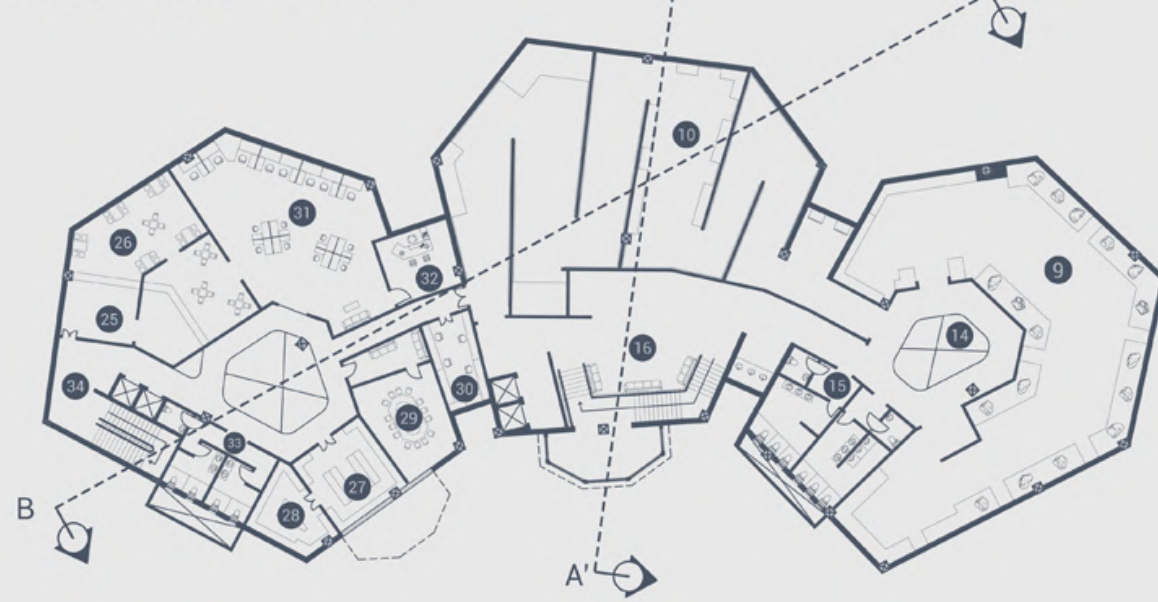

2nd FLOOR PLAN

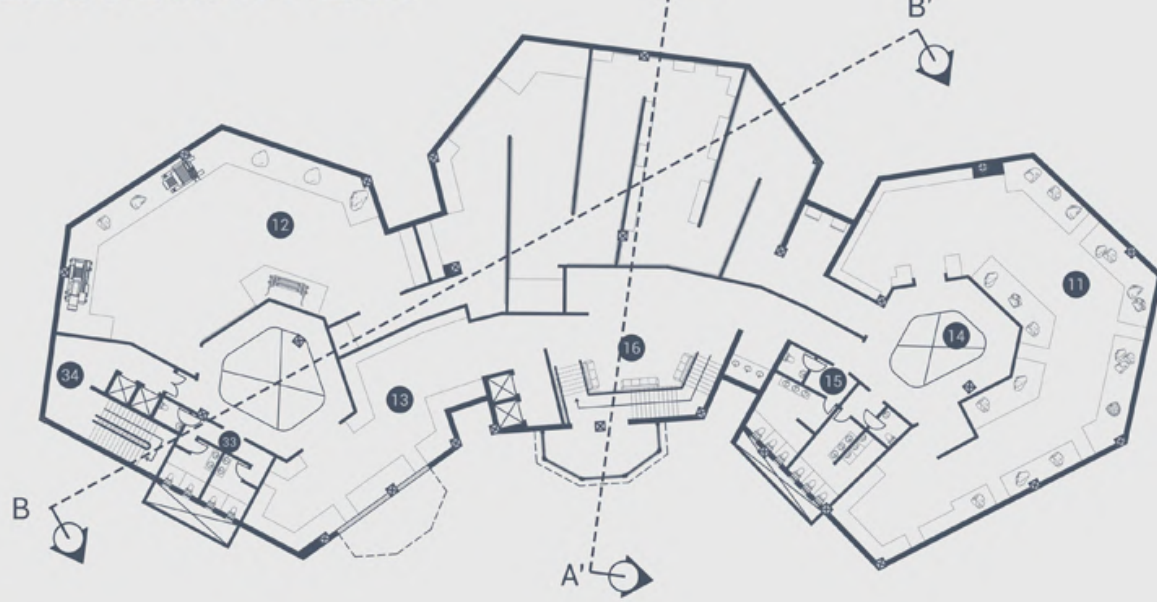


MUSEUM



SECTION AA'

SECTION BB'


GROUND FLOOR PLAN

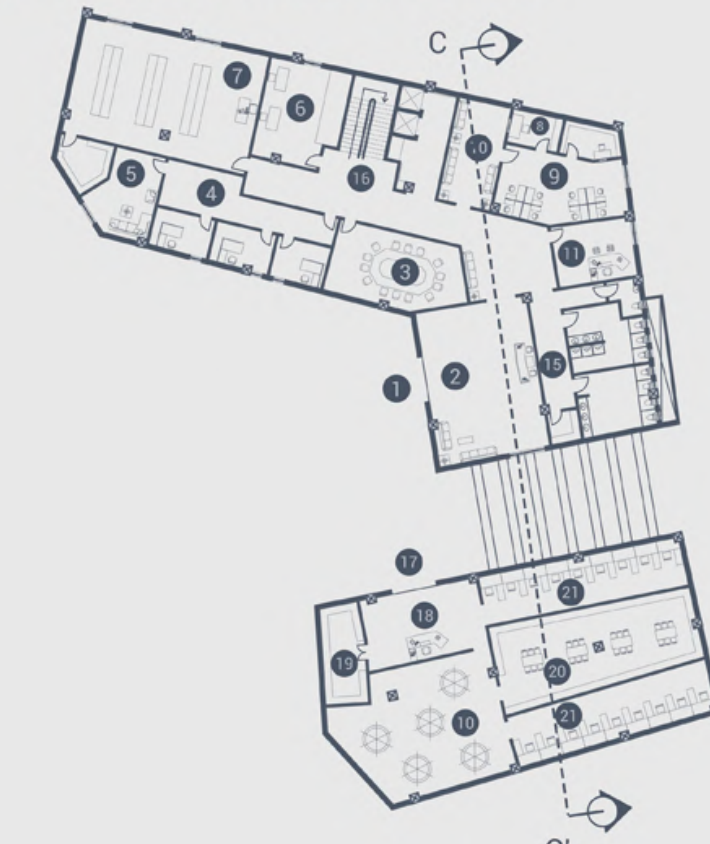

LEGEND

LEARNING CENTRE		LIBRARY	
1	Main Entry	17	Main Entry/Exit
2	Entrance Lobby	18	Entrance Lobby
3	Conference	19	Baggage Counter
4	Trainer's Room	20	Study Area
5	Trainer's Resting	21	Individual Study Area
6	Non-Teaching Staff		
7	Workshop		
8	Admission		
9	Accounts		
10	Waiting Area		
11	HOD Office		
12	Classrooms		
13	AV Room		
14	Store Room		
15	Toilet		
16	Lift Lobby		


GROUND FLOOR PLAN

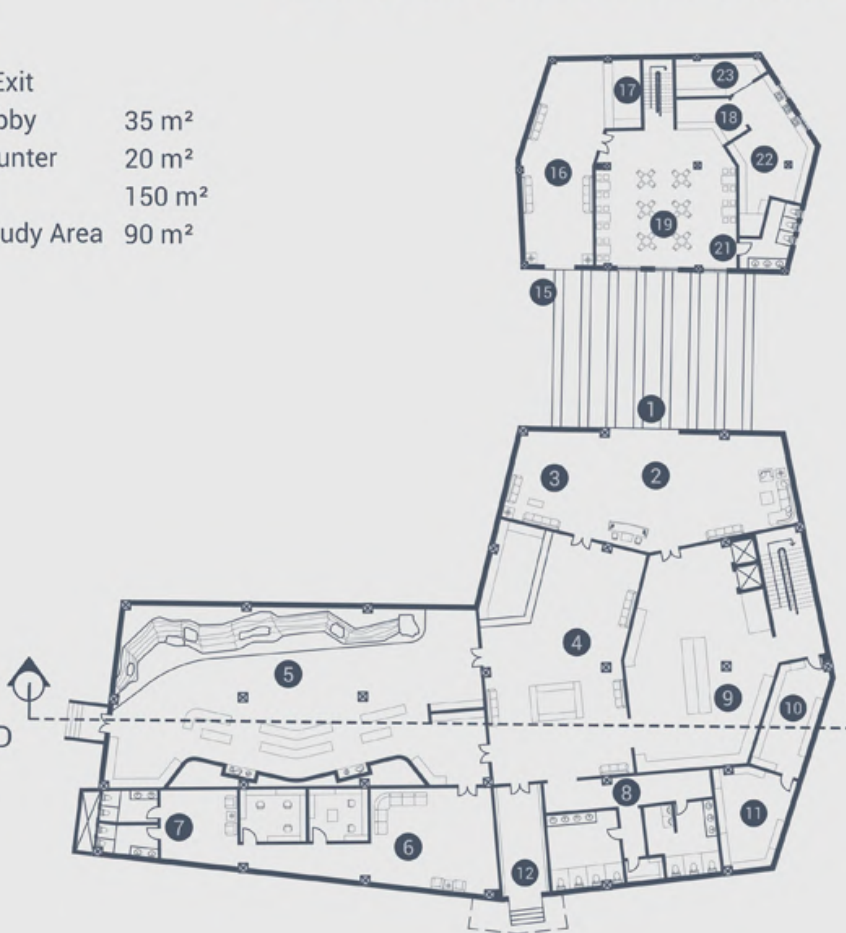

LEGEND

IMMERSIVE THEATRE		CAFE	
1	Main Entry/Exit	15	Main Entry/Exit
2	Entrance Lobby	16	Entrance Lobby
3	Waiting Area	17	Billing Counter
4	Reading Zone	18	Food Counter
5	Diorama Display	19	Dining Space G
6	Back Office	20	Dining Space 1st
7	Toilet 1	21	Toilet
8	Toilet 2	22	Kitchen
9	Exhibits/ Display	23	Storage
10	AHU		
11	Electrical		
12	Exit 2		
13	Seatings		
14	VR Zone		

1st FLOOR PLAN

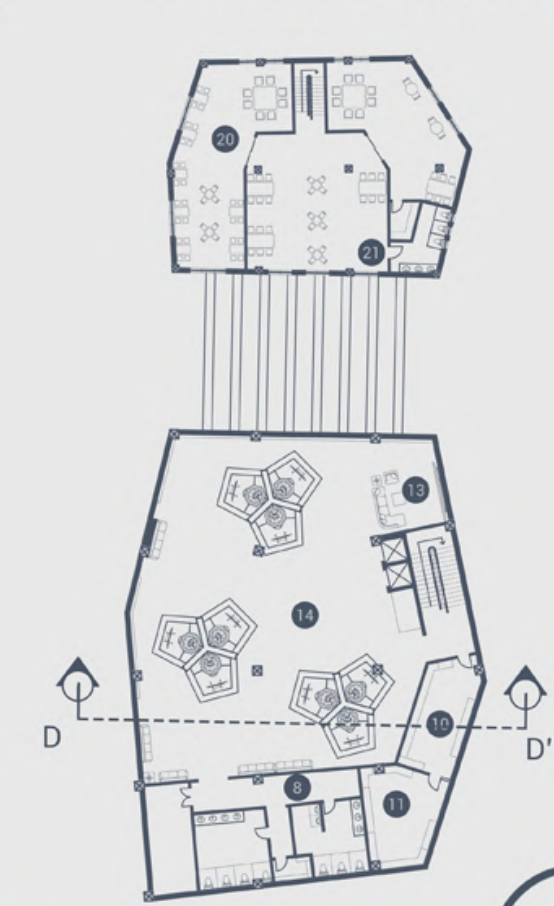

LEARNING CENTRE



IMMERSIVE THEATRE

SECTION CC'

SECTION BB'



MUSEUM ENTRANCE

**LIBRARY
COURTYARD**

DIORAMA DISPLAY



IMMERSIVE THEATRE




03 INTERNSHIP WORK

Company : buildAhome Pvt Ltd

Semester : S10

Address : Fourth Floor, CRN Chambers, 13, Kasturba Rd, Shanthala Nagar, Ashok Nagar, Bengaluru, Karnataka - 560001

Buildahome is a construction firm that focuses on designing and developing residential spaces with a strong emphasis on functionality, aesthetics, and client requirements. During my internship at Buildahome as an Architectural Intern, I gained practical exposure to the various stages of architectural design and execution. The internship provided me with an opportunity to understand real-world design processes, develop technical and software skills, prepare drawings, and observe how architectural ideas are translated into built spaces. It also helped me understand the importance of coordination, site execution, material selection, and communication within a professional architectural practice.

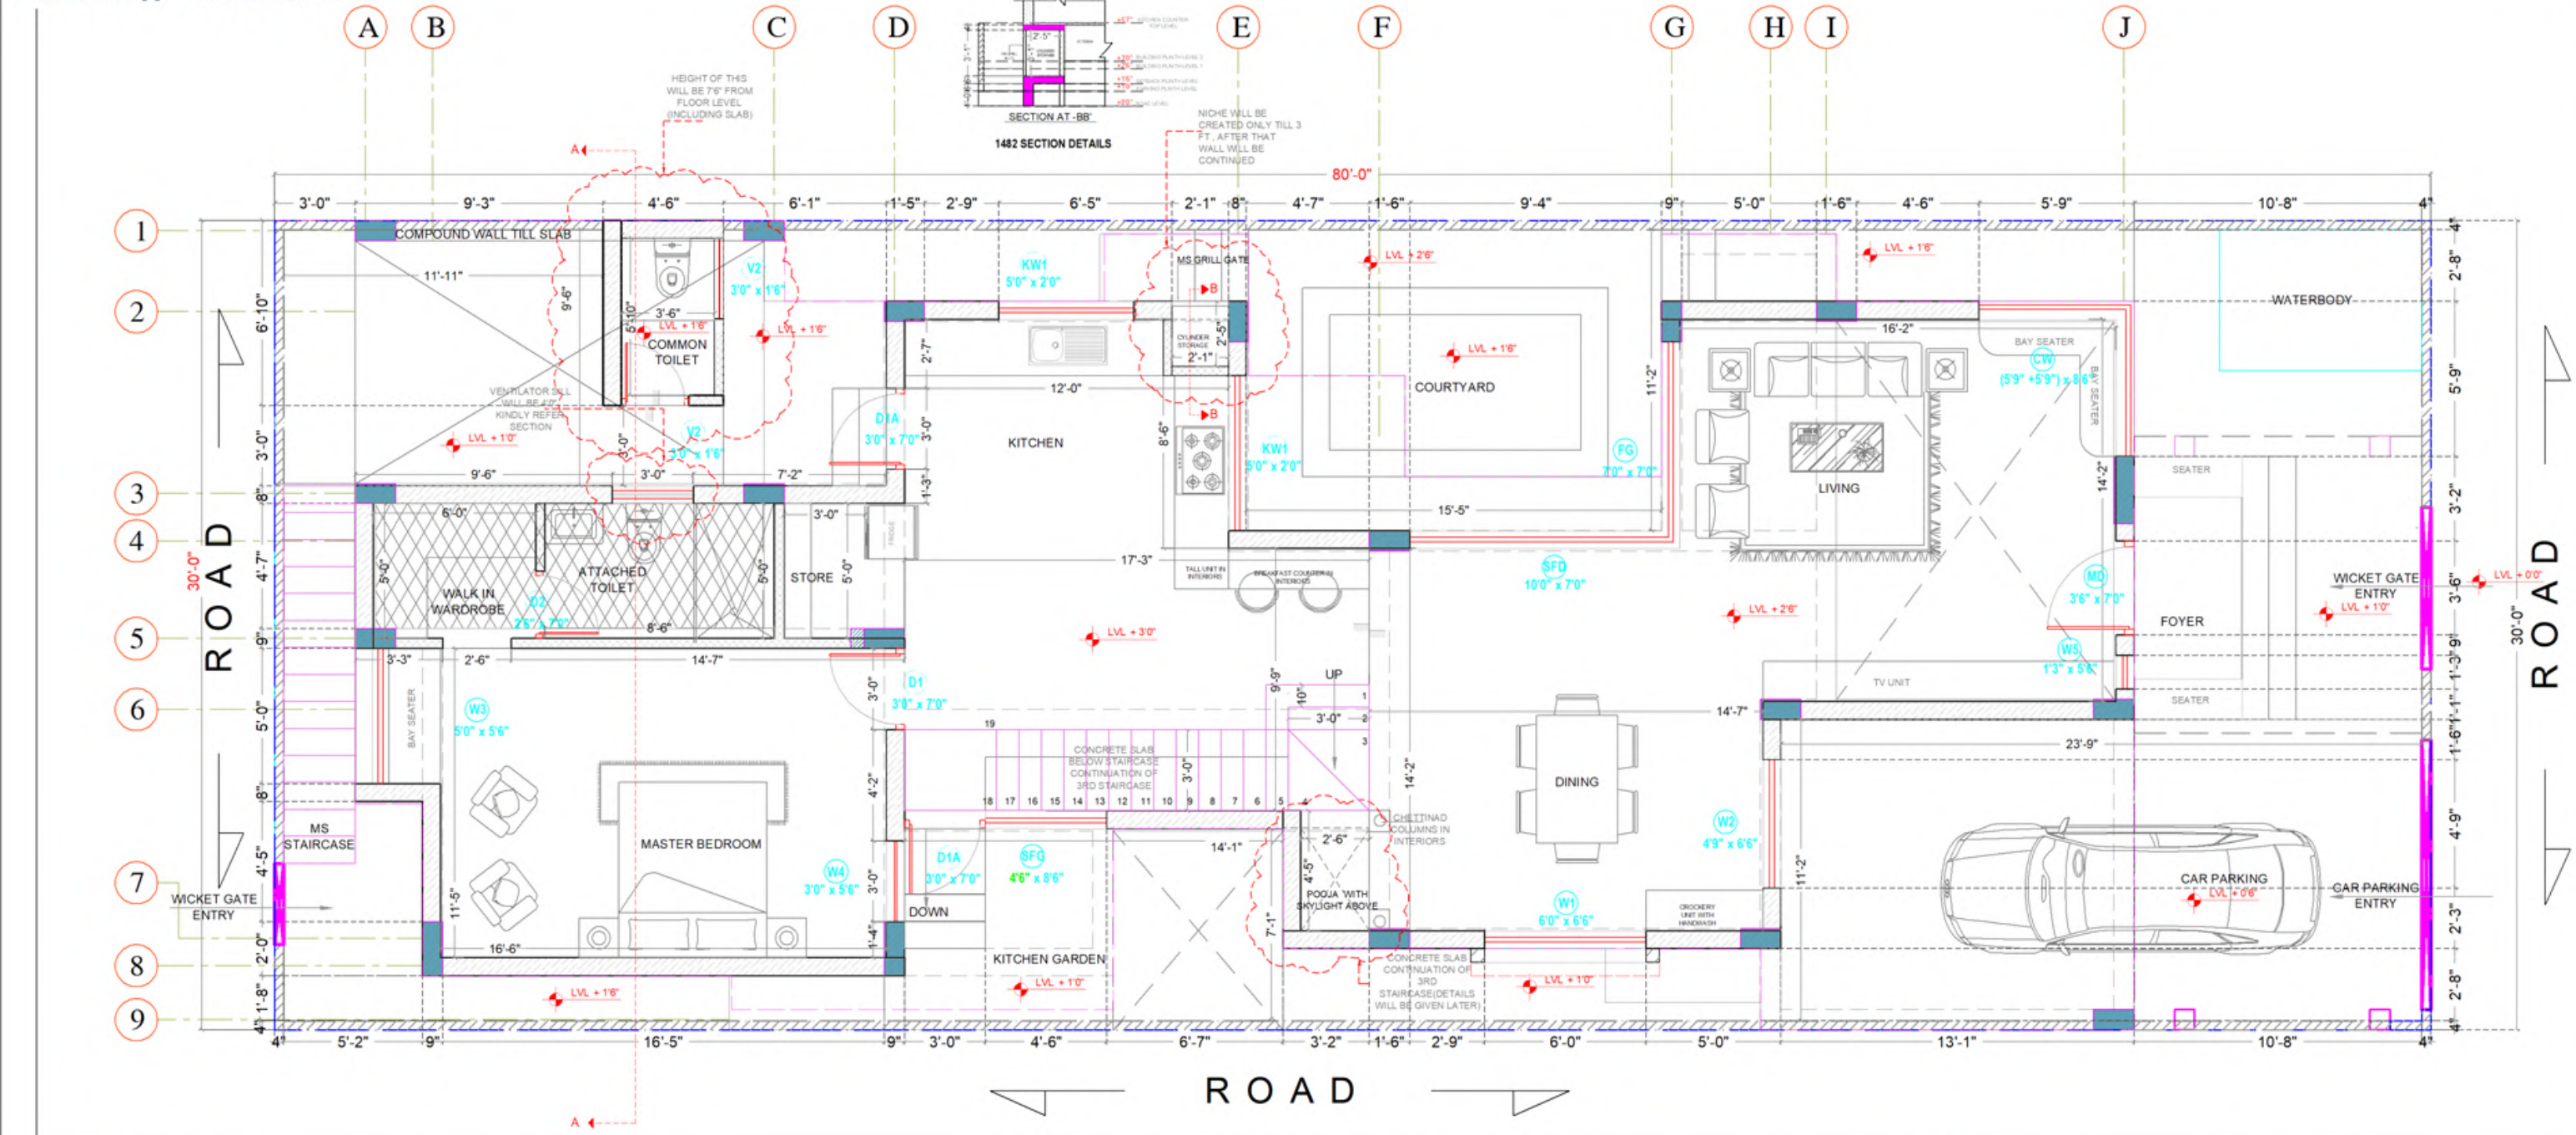

Schedule of Opening - 1482

NAME	SIZE	SILL	DESCRIPTION	FLOOR	NO3
MD	(3'6" X 7'0")	----	Main Door	1st	01
D1	(3'0" X 7'0")	----	Bedroom Door	1st	04
D1A	(3'0" X 7'0")	----	Temple Door	1st	04
D1A+V	(3'0" X 1'3") X 7'0"	----	Bedroom Glass Door with	1st	01
D2	(2'6" X 7'0")	----	Toilet Door	1st	06
SFD	(10'0" X 7'0")	----	Sliding Folding Door	1st	01
FD1	(5'9" X 7'0")	----	French door 1	1st	01
FD2	(3'0" X 7'0")	----	French door 2	1st	01
					19

NAME	SIZE	SILL	DESCRIPTION	FLOOR	NO3
W1	(6'0" X 6'6")	0'-6"	Window 1	1st	01
W2	(4'9" X 6'6")	0'-6"	Window 2	1st	01
W3	(5'0" X 5'6")	1'-6"	Window 3	1st	04
W3A	(5'0" X 3'6")	1'-6"	Window 3	1st	01
W4	(3'0" X 5'6")	1'-6"	Window 4	1st	02
W5	(1'3" X 5'6")	1'-6"	Window 5	1st	03
W6	(2'0" X 5'0")	1'-6"	Window 6	1st	02
SFG	(4'6" X 8'0")	0'-6"	Sliding Folding Glass	1st	02
FG	(7'0" X 7'0")	0'-0"	Fixed Glass	1st	01
CW	(3'0" X 3'0")	3'-6"	Corner Window	1st	01
BW	(8'6" X 5'6")	1'-6"	Bay Window	1st	01
KW1	(5'0" X 2'0")	3'-0"	Kitchen Window 1	1st	02
KW2	(2'0" X 2'0")	3'-0"	Kitchen Window 2	1st	01
V1	(4'6" X 1'6")	7'-0"	Ventilator 1	1st	01
V2	(3'0" X 1'6")	7'-0"	Ventilator 2	1st	01
					29

CLIENT : SUBHASHINI

DRAWING NAME: GROUND FLOOR

GENERAL NOTES :

1. All dimensions are in feet and inches unless otherwise specified.
2. Drawing is not to scale, hence follow the dimensions mentioned.
3. Changes in the drawing should not be made without the notice of the project head and/or architect handling the project.

LEGEND :

- 4" BLOCK WORK - 5' HT Compound wall
- 4" BLOCK WORK - 3' HT Parapet wall
- 6" BLOCK WORK
- 4" BLOCK WORK
- BEAM BOTTOM PROJECTION
- SLAB PROJECTION
- LINEEL PROJECTION
- MS & CNC DESIGN
- 8" BLOCK WORK

The following has been considered w.r.t the floor plans given and the same will be considered for costing unless changed by client, which needs to be intimated to the architect handling the project which will further be intimated to the marketing team.

1. Floor to Floor height : 10'0"
2. Type of internal staircase : FOLDED PLATE STAIRCASE
3. Plinth height (From N.G.L.) : + 2'6"
4. No. of Floors constructed at present : G + 1.5
5. No. of Floors for Structural design : G + 1.5
6. External Wall : 8" Solid Block
7. Internal Wall : 4" Solid Block

NOTE :

THIS DRAWING IS THE EXCLUSIVE PROPERTY OF "BUILDAHOME" .AND THE REPRODUCTION OF ANY PART WITHOUT PRIOR WRITTEN CONSENT FROM THIS OFFICE IS A VIOLATION OF APPLICABLE LAWS.

CONSULTANT: **buildAhome**



ScenicBeauty Homes Pvt Ltd.
Address: Fourth Floor, CRN Chambers, 13, Kasturba Rd, Shanbhala Nagar, Ashok Nagar, Bengaluru, Karnataka 560001
Ph no: +91-7090 0056 00, +91-80-2351 1033
www.buildahome.in
Ph no: +91-7090 0056 00, +91-80-2351 1033
www.buildahome.in

DRAWING NO: BAH/1482/SUBHASHINI/2025/ARCH/WD001/R1

SHEET NO : 001

SCALE : NOT TO SCALE

CHECKED : Ar. VIKAS


DRAWN : KEERTHISH G

DATE : 31-03-2026

ARCHITECTURAL WORKING DRAWING



WORKING DRAWINGS

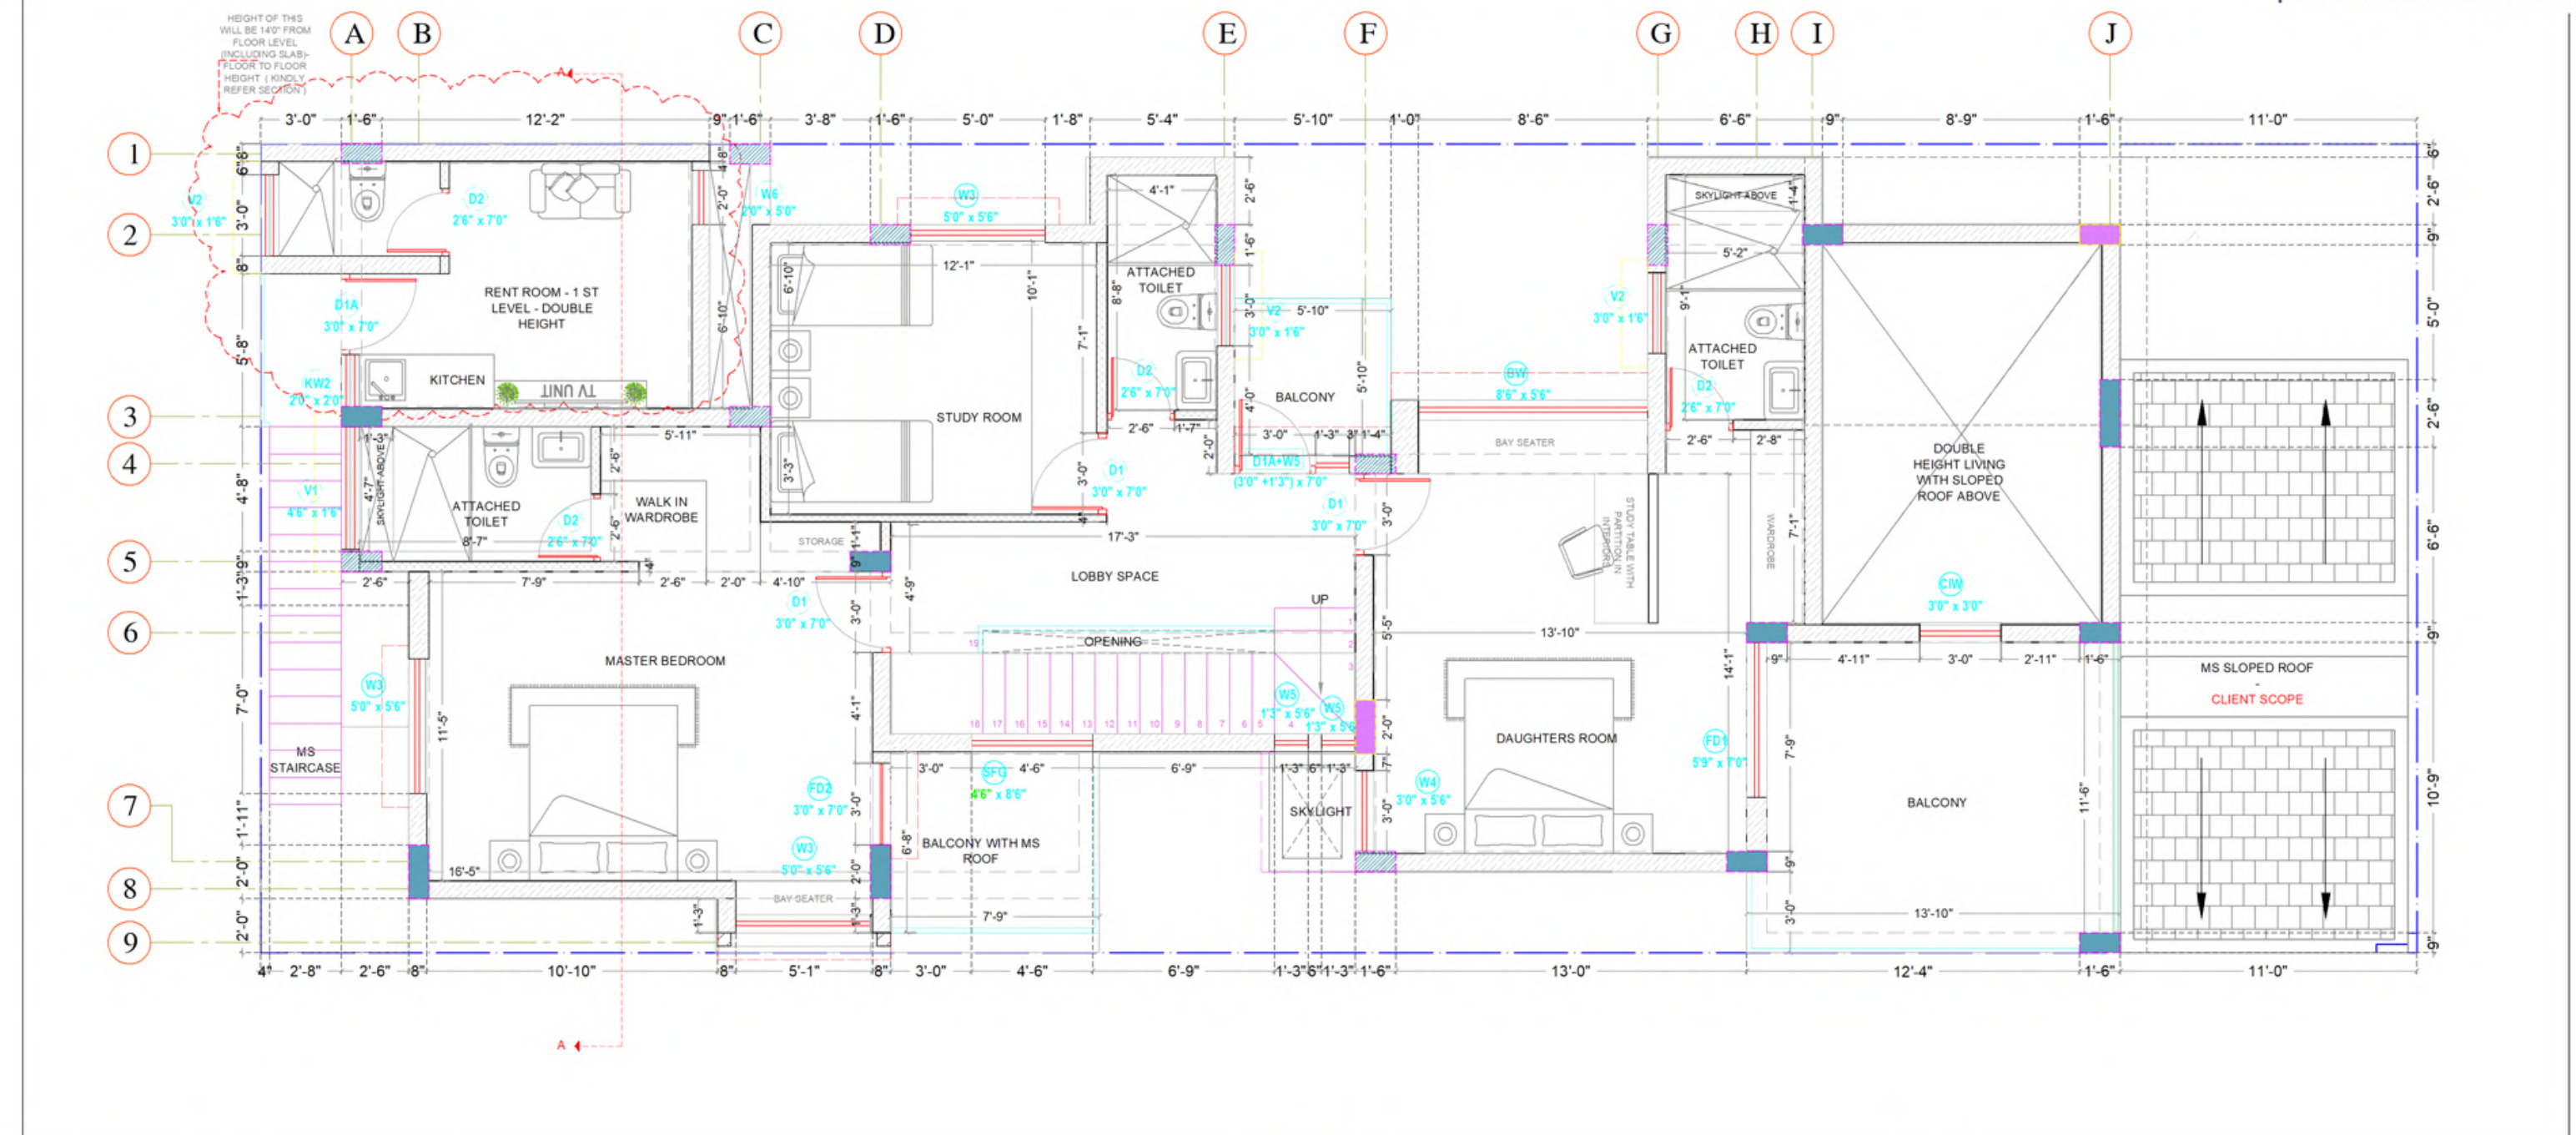

Schedule of Opening - 1482

NAME	SIZE	SILL	DESCRIPTION	FLOOR	NO3
MD	(3'6" X 7'0")	----	Main Door	1st	01
D1	(3'0" X 7'0")	----	Bedroom Door	1st	04
D1A	(3'0" X 7'0")	----	Temple Door	1st	04
D1A+V	(3'0" X 1'3") X 7'0"	----	Bedroom Glass Door with	1st	01
D2	(2'6" X 7'0")	----	Toilet Door	1st	06
SFD	(10'0" X 7'0")	----	Sliding Folding Door	1st	01
FD1	(5'9" X 7'0")	----	French door 1	1st	01
FD2	(3'0" X 7'0")	----	French door 2	1st	01
					19

NAME	SIZE	SILL	DESCRIPTION	FLOOR	NO3
W1	(6'0" X 6'6")	0'-6"	Window 1	1st	01
W2	(4'9" X 6'6")	0'-6"	Window 2	1st	01
W3	(5'0" X 5'6")	1'-6"	Window 3	1st	04
W3A	(5'0" X 3'6")	1'-6"	Window 3	1st	01
W4	(3'0" X 5'6")	1'-6"	Window 4	1st	02
W5	(1'3" X 5'6")	1'-6"	Window 5	1st	03
W6	(2'0" X 5'0")	1'-6"	Window 6	1st	02
SFG	(4'6" X 8'0")	0'-6"	Sliding Folding Glass	1st	02
FG	(7'0" X 7'0")	0'-0"	Fixed Glass	1st	01
CW	(3'0" X 3'0")	3'-6"	Corner Window	1st	01
BW	(8'6" X 5'6")	1'-6"	Bay Window	1st	01
KW1	(5'0" X 2'0")	3'-0"	Kitchen Window 1	1st	02
KW2	(2'0" X 2'0")	3'-0"	Kitchen Window 2	1st	01
V1	(4'6" X 1'6")	7'-0"	Ventilator 1	1st	01
V2	(3'0" X 1'6")	7'-0"	Ventilator 2	1st	01
					29

CLIENT : SUBHASHINI

DRAWING NAME: FIRST FLOOR - 1 ST LEVEL

GENERAL NOTES :

1. All dimensions are in feet and inches unless otherwise specified.
2. Drawing is not to scale, hence follow the dimensions mentioned.
3. Changes in the drawing should not be made without the notice of the project head and/or architect handling the project.

LEGEND :

- 4" BLOCK WORK - 5' HT Compound wall
- 4" BLOCK WORK - 3' HT Parapet wall
- 6" BLOCK WORK
- 4" BLOCK WORK
- BEAM BOTTOM PROJECTION
- SLAB PROJECTION
- LINEEL PROJECTION
- MS & CNC DESIGN
- 8" BLOCK WORK

The following has been considered w.r.t the floor plans given and the same will be considered for costing unless changed by client, which needs to be intimated to the architect handling the project which will further be intimated to the marketing team.

1. Floor to Floor height : 10'0"
2. Type of internal staircase : FOLDED PLATE STAIRCASE
3. Plinth height (From N.G.L.) : + 2'6"
4. No. of Floors constructed at present : G + 1.5
5. No. of Floors for Structural design : G + 1.5
6. External Wall : 8" Solid Block
7. Internal Wall : 4" Solid Block

NOTE :

THIS DRAWING IS THE EXCLUSIVE PROPERTY OF "BUILDAHOME" .AND THE REPRODUCTION OF ANY PART WITHOUT PRIOR WRITTEN CONSENT FROM THIS OFFICE IS A VIOLATION OF APPLICABLE LAWS.

CONSULTANT: **buildAhome**



ScenicBeauty Homes Pvt Ltd.
Address: Fourth Floor, CRN Chambers, 13, Kasturba Rd, Shanbhala Nagar, Ashok Nagar, Bengaluru, Karnataka 560001
Ph no: +91-7090 0056 00, +91-80-2351 1033
www.buildahome.in
Ph no: +91-7090 0056 00, +91-80-2351 1033
www.buildahome.in

DRAWING NO: BAH/1482/SUBHASHINI/2025/ARCH/WD001/R1

SHEET NO : 002

SCALE : NOT TO SCALE



CHECKED : Ar. VIKAS

DRAWN : KEERTHISH G

DATE : 31-03-2026

ARCHITECTURAL WORKING DRAWING



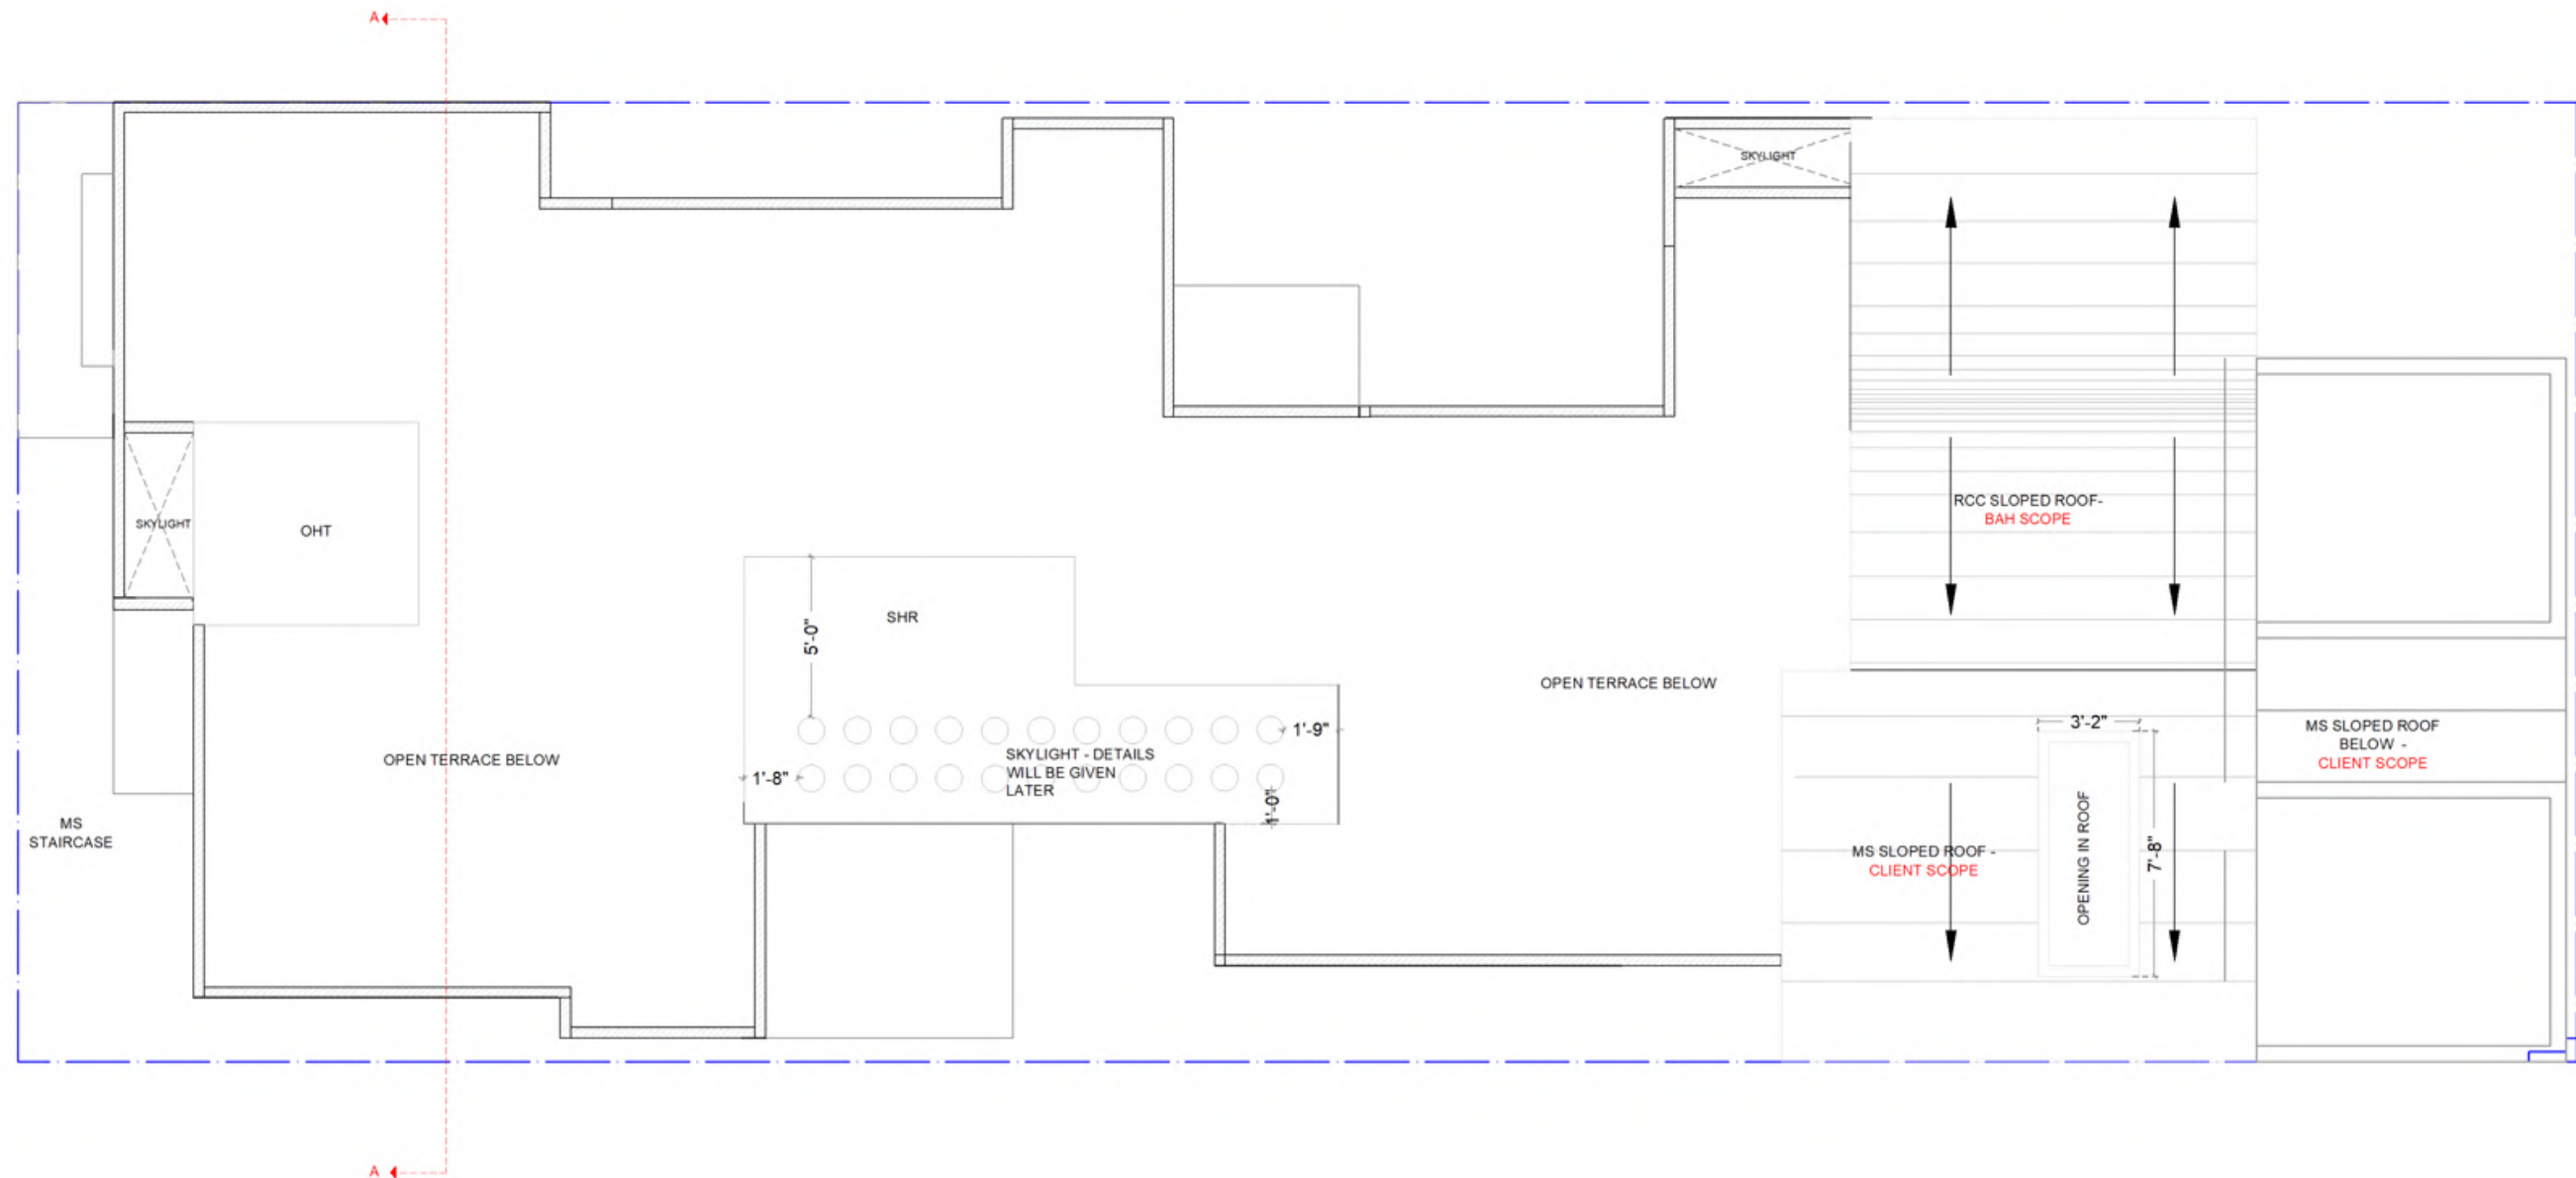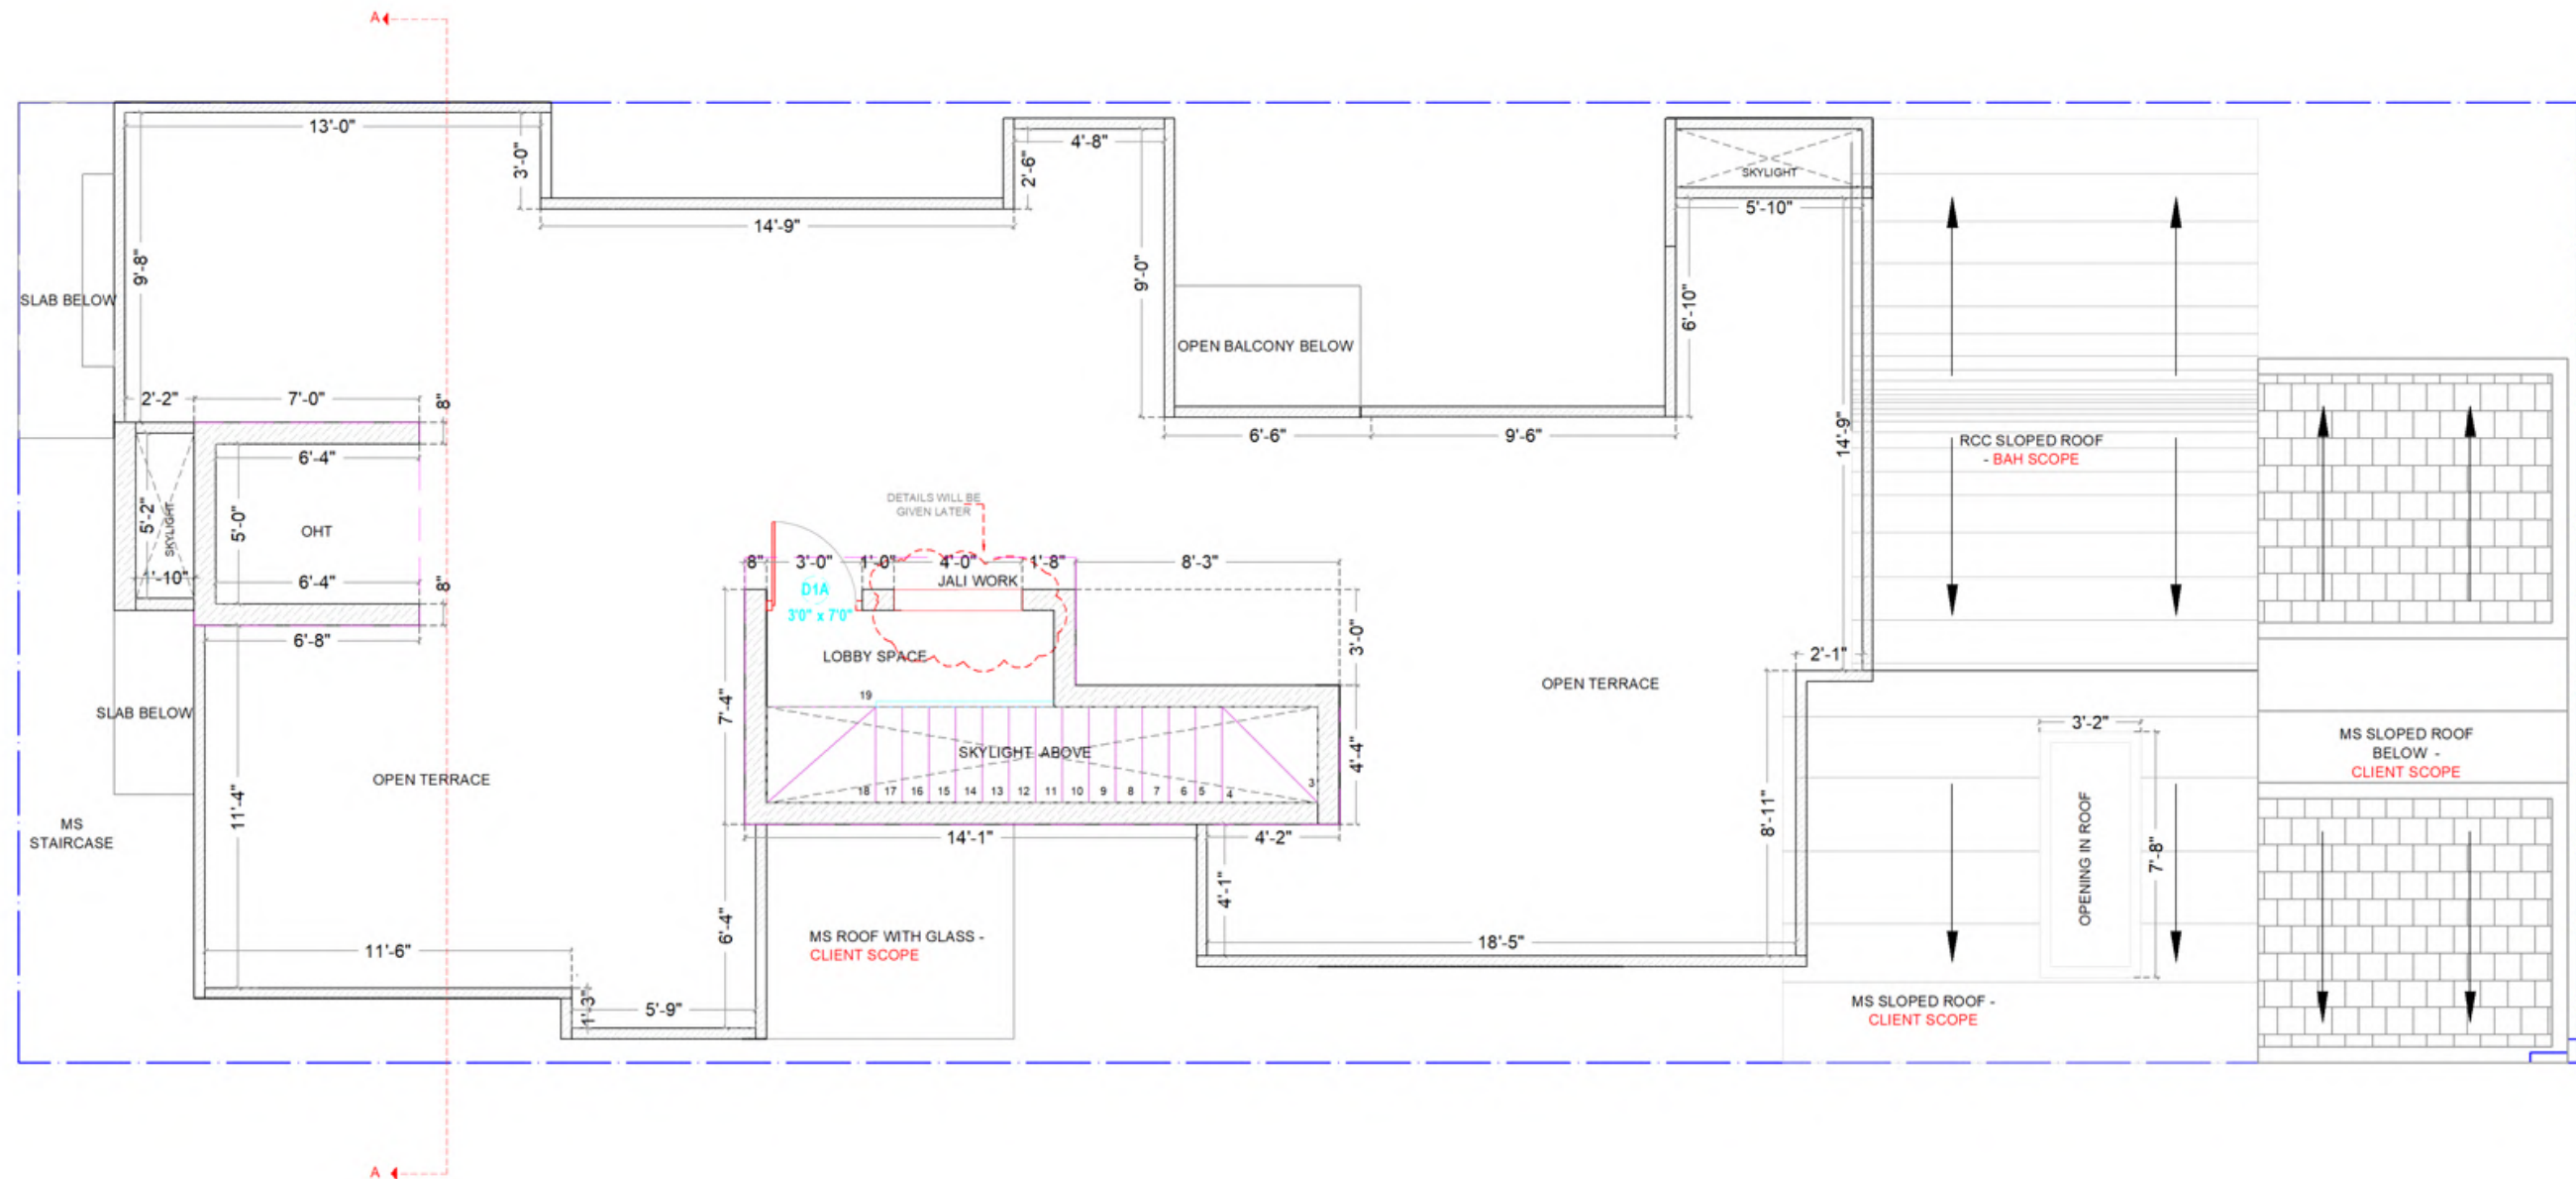

WORKING DRAWINGS

Schedule of Opening - 1482				
NAME	SIZE	SILL	DESCRIPTION	FLOOR NOS
DOORS				
MD	(3'6" X 7'0")	----	Main Door	01
D1	(3'0" X 7'0")	----	Bedroom Door	04
D1A	(3'0" X 7'0")	----	Terrace Door	04
D1A+D2	(10'0" X 13'0")	----	Bedroom Glass Door with Terrace	01
D2	(2'6" X 7'0")	----	Toilet Door	06
SFD	(10'0" X 7'0")	----	Sliding Foldable Door	01
FD1	(5'9" X 7'0")	----	French door 1	01
FD2	(3'0" X 7'0")	----	French door 2	01
WINDOWS				
W1	(6'0" X 6'6")	0'-6"	Window 1	01
W2	(4'9" X 6'6")	0'-6"	Window 2	01
W3	(5'0" X 5'6")	1'-6"	Window 3	04
W3A	(5'0" X 3'6")	1'-6"	Window 3	01
W4	(3'0" X 5'6")	1'-6"	Window 4	02
W5	(1'3" X 5'6")	1'-6"	Window 5	03
W6	(2'0" X 5'0")	1'-6"	Window 6	02
SFG	(4'6" X 8'0")	0'-6"	Sliding Foldable Glass	02
FG	(7'0" X 7'0")	0'-6"	Fixed Glass	01
CW	(3'0" X 3'0")	1'-6"	Corner Window	01
CW	(3'0" X 3'0")	3'-6"	Circular Window	01
BW	(8'6" X 5'6")	1'-6"	Bay Window	01
KW1	(5'0" X 2'0")	3'-0"	Kitchen Window 1	02
KW2	(2'0" X 2'0")	3'-0"	Kitchen Window 2	01
V1	(4'6" X 1'6")	7'-0"	Ventilator 1	01
V2	(3'0" X 1'6")	7'-0"	Ventilator 2	05

CLIENT : SUBHASHINI

DRAWING NAME: TERRACE FLOOR

GENERAL NOTES :

1. All dimensions are in feet and inches unless otherwise specified.
2. Drawing is not to scale, hence follow the dimensions mentioned.
3. Changes in the drawing should not be made without the notice of the project head and/or architect handling the project.

LEGEND :

- 4" BLOCK WORK - 5' HT Compound wall
- 4" BLOCK WORK - 3' HT Parapet wall
- 6" BLOCK WORK
- 4" BLOCK WORK
- BEAM BOTTOM PROJECTION
- SLAB PROJECTION
- LINTEL PROJECTION
- MS & CNC DESIGN
- 8" BLOCK WORK

The following has been considered w.r.t the floor plans given and the same will be considered for costing unless changed by client, which needs to be intimated to the architect handling the project which will further be intimated to the marketing team.

1. Floor to Floor height : 8'0"
2. Type of internal staircase : FOLDED PLATE STAIRCASE
3. Plinth height (From N.G.L) : + 1'6"
4. No. of Floors constructed at present : G + 1.5
5. No. of Floors for Structural design : G + 1.5
6. External Wall : 8" Solid Block
7. Internal Wall : 4" Solid Block

NOTE :

THIS DRAWING IS THE EXCLUSIVE PROPERTY OF "BUILDAHOMES" .AND THE REPRODUCTION OF ANY PART WITHOUT PRIOR WRITTEN CONSENT FROM THIS OFFICE IS A VIOLATION OF APPLICABLE LAWS.

CONSULTANT: **buildAhome**
A Virgo Group Company
ScenicBeauty Homes Pvt Ltd.
Address :Fourth Floor, CRN Chambers, 13, Kasturba Rd, Shanthala Nagar, Ashok Nagar, Bengaluru, Karnataka 560001
Ph no :+91-7090 0056 00, +91-80-2351 1033
www.buildahome.in
Ph no : +91-7090 0056 00 , +91-80-2351 1033
www.buildahome.in

DRAWING NO: BAH/1482/SUBHASHINI/2025/ARCH/WD001/R1

SHEET NO : 003

SCALE : NOT TO SCALE

CHECKED : Ar. VIKAS

DRAWN : KEERTHISH G

DATE : 31-03-2026

ARCHITECTURAL WORKING DRAWING



Schedule of Opening - 1482				
NAME	SIZE	SILL	DESCRIPTION	FLOOR NOS
DOORS				
MD	(3'6" X 7'0")	----	Main Door	01
D1	(3'0" X 7'0")	----	Bedroom Door	04
D1A	(3'0" X 7'0")	----	Terrace Door	04
D1A+D2	(10'0" X 13'0")	----	Bedroom Glass Door with Terrace	01
D2	(2'6" X 7'0")	----	Toilet Door	06
SFD	(10'0" X 7'0")	----	Sliding Foldable Door	01
FD1	(5'9" X 7'0")	----	French door 1	01
FD2	(3'0" X 7'0")	----	French door 2	01
WINDOWS				
W1	(6'0" X 6'6")	0'-6"	Window 1	01
W2	(4'9" X 6'6")	0'-6"	Window 2	01
W3	(5'0" X 5'6")	1'-6"	Window 3	04
W3A	(5'0" X 3'6")	1'-6"	Window 3	01
W4	(3'0" X 5'6")	1'-6"	Window 4	02
W5	(1'3" X 5'6")	1'-6"	Window 5	03
W6	(2'0" X 5'0")	1'-6"	Window 6	02
SFG	(4'6" X 8'0")	0'-6"	Sliding Foldable Glass	02
FG	(7'0" X 7'0")	0'-6"	Fixed Glass	01
CW	(3'0" X 3'0")	1'-6"	Corner Window	01
CW	(3'0" X 3'0")	3'-6"	Circular Window	01
BW	(8'6" X 5'6")	1'-6"	Bay Window	01
KW1	(5'0" X 2'0")	3'-0"	Kitchen Window 1	02
KW2	(2'0" X 2'0")	3'-0"	Kitchen Window 2	01
V1	(4'6" X 1'6")	7'-0"	Ventilator 1	01
V2	(3'0" X 1'6")	7'-0"	Ventilator 2	05

CLIENT : SUBHASHINI

DRAWING NAME: ROOF FLOOR

GENERAL NOTES :

1. All dimensions are in feet and inches unless otherwise specified.
2. Drawing is not to scale, hence follow the dimensions mentioned.
3. Changes in the drawing should not be made without the notice of the project head and/or architect handling the project.

LEGEND :

- 4" BLOCK WORK - 5' HT Compound wall
- 4" BLOCK WORK - 3' HT Parapet wall
- 6" BLOCK WORK
- 4" BLOCK WORK
- SILL PROJECTION
- BEAM BOTTOM PROJECTION
- SLAB PROJECTION
- LINTEL PROJECTION
- MS & CNC DESIGN
- 8" BLOCK WORK

The following has been considered w.r.t the floor plans given and the same will be considered for costing unless changed by client, which needs to be intimated to the architect handling the project which will further be intimated to the marketing team.

1. Floor to Floor height : 8'0"
2. Type of internal staircase : FOLDED PLATE STAIRCASE
3. Plinth height (From N.G.L) : + 1'6"
4. No. of Floors constructed at present : G + 1.5
5. No. of Floors for Structural design : G + 1.5
6. External Wall : 8" Solid Block
7. Internal Wall : 4" Solid Block

NOTE :

THIS DRAWING IS THE EXCLUSIVE PROPERTY OF "BUILDAHOMES" .AND THE REPRODUCTION OF ANY PART WITHOUT PRIOR WRITTEN CONSENT FROM THIS OFFICE IS A VIOLATION OF APPLICABLE LAWS.

CONSULTANT: **buildAhome**
A Virgo Group Company
ScenicBeauty Homes Pvt Ltd.
Address :Fourth Floor, CRN Chambers, 13, Kasturba Rd, Shanthala Nagar, Ashok Nagar, Bengaluru, Karnataka 560001
Ph no :+91-7090 0056 00, +91-80-2351 1033
www.buildahome.in
Ph no : +91-7090 0056 00 , +91-80-2351 1033
www.buildahome.in

DRAWING NO: BAH/1482/SUBHASHINI/2025/ARCH/WD001/R1

SHEET NO : 004

SCALE : NOT TO SCALE

CHECKED : Ar. VIKAS

DRAWN : KEERTHISH G

DATE : 31-03-2026

ARCHITECTURAL WORKING DRAWING







GROUND FLOOR
INTERIOR VIEWS




FIRST FLOOR
INTERIOR VIEWS

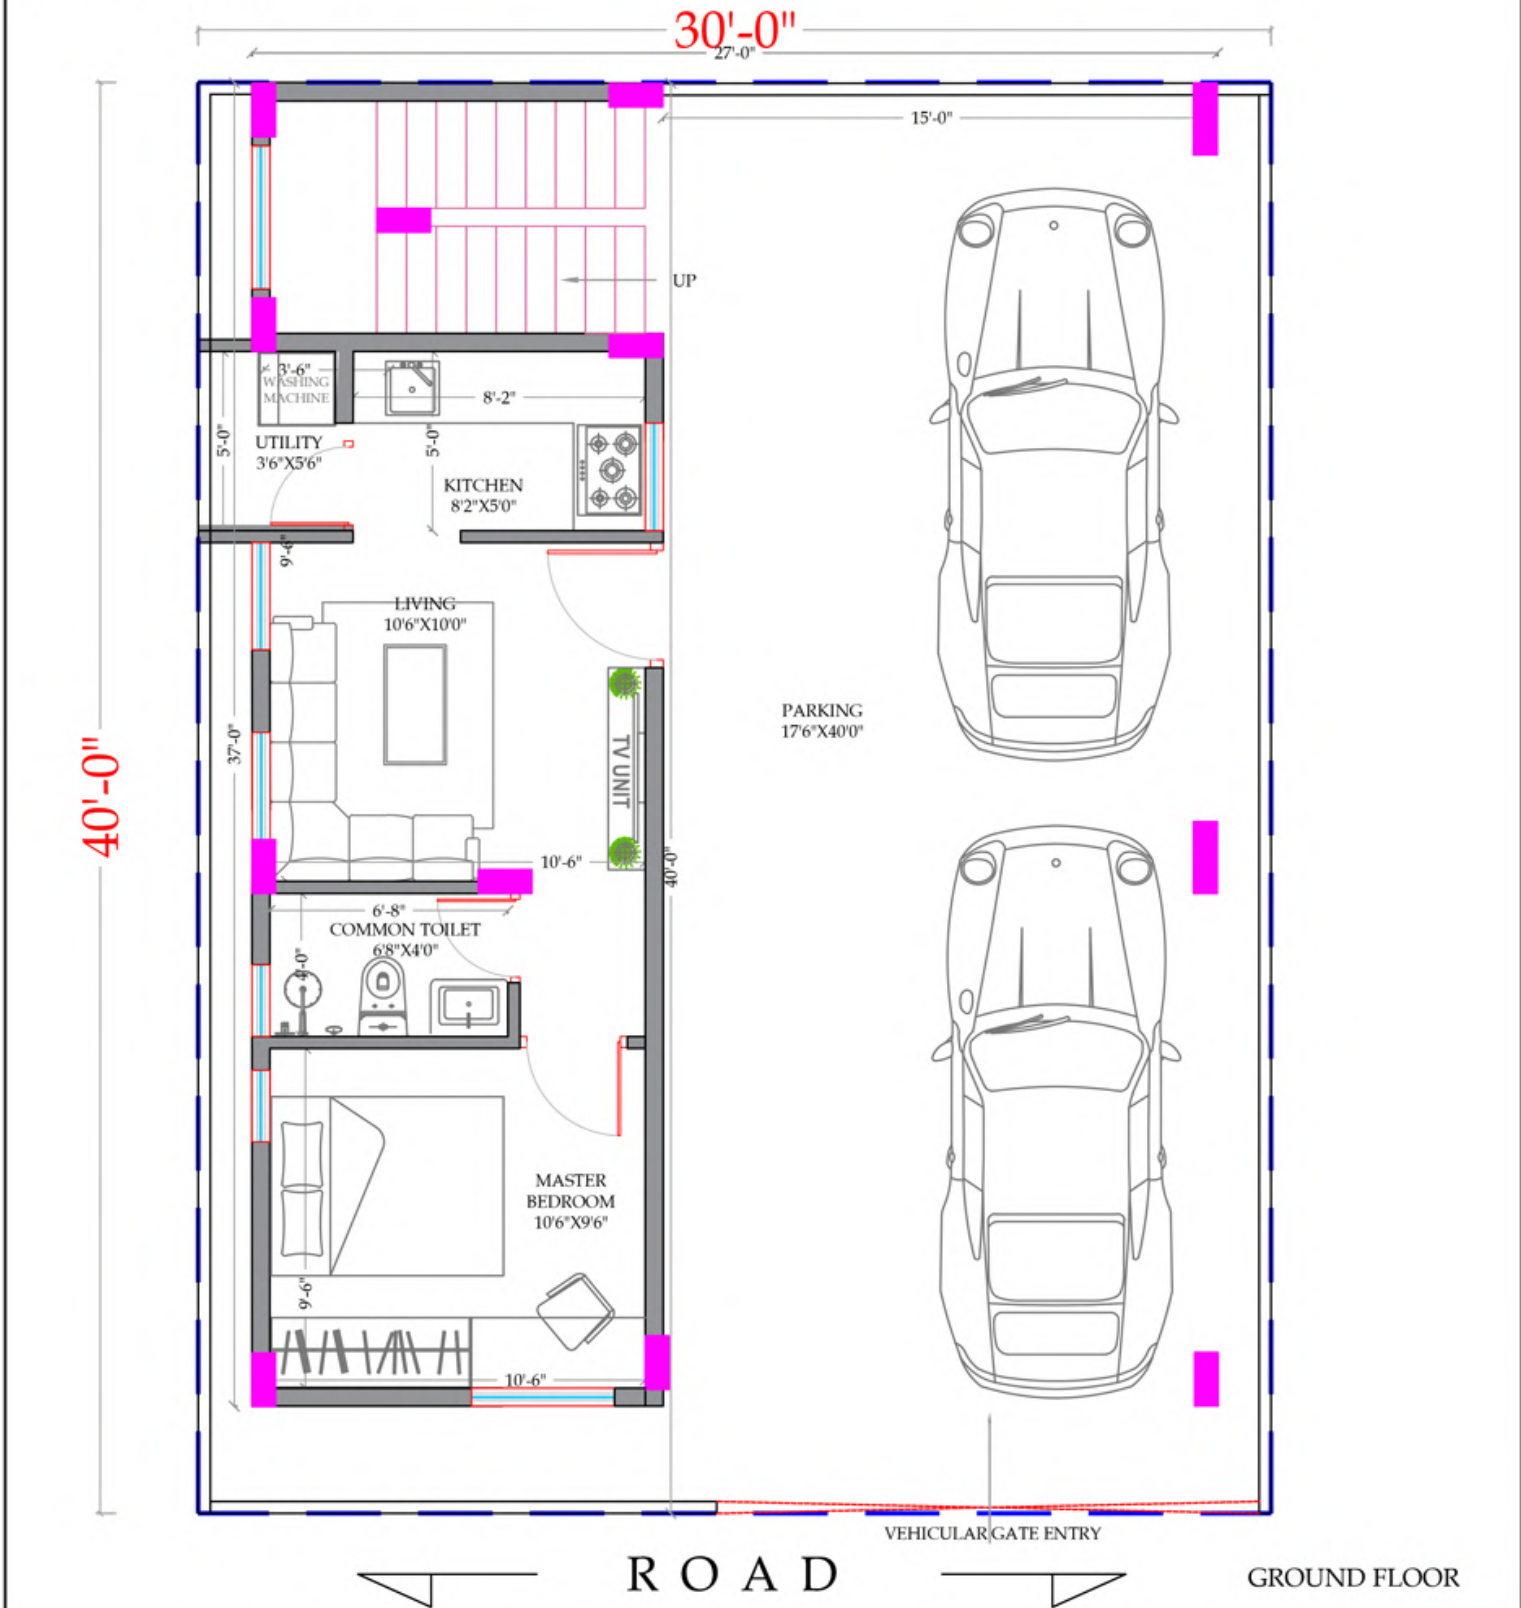


NOTE The following has been considered w.r.t the floor plans given and the same will be considered for costing unless changed by client, which needs to be intimated to the architect handling the project which will further be intimated to the marketing team. 1. Floor to Floor height : 10' (includes slab) 2. Type of internal staircase : -- 3. Type of external staircase : Waist Slab 4. Plinth height (From N.G.L.) : +1'6" 5. No. of Floors constructed at present : G + 3.5 6. No. of Floors for Structural design : G + 3.5 7. External Wall : 6" SOLID BLOCK 8. Internal Wall : 4" SOLID BLOCK *If the relevant regulatory requirements or norms(Government rules) are not going to be met by the plan with respect to the building's setback. The client will be liable for any ensuing problems. *In case the dimensions and angle may change while it is being marked with a grid during execution.	PROPOSED RESIDENCE FOR : MR. PRAMOD .DP			SHEET NO.	N W E S	
	PROJECT NO.: 1693			DATE :15-04-2026		
	OPTION NO. 01			SCALE : N.T.S		
				LOCATION :		
	Date	Revision NO	Reasons	 buildAhome A Virgo Group Company Scenic Beauty Homes Pvt Ltd Address : Fourth Floor, CRN Chambers, 13, Kasturba Rd, Shanthala Nagar, Ashok Nagar, Bengaluru, Karnataka 560001 Ph no : +91-7090 0056 00 , +91-80-2351 1033 www.buildahome.in		
	04-04-2026	R-1	PROPOSED FLOOR PLANS			
	08-04-2026	R-2	Revision in Third floor and terrace floor, Bedroom is added in terrace floor			
	15-04-2026	R-3	Door position of toilet is interchanged and parallel wardrobe is added, columns are positioned			
	DESIGNED BY : Ar. SORNA					
	CHECKED BY : Ar. VIKAS					

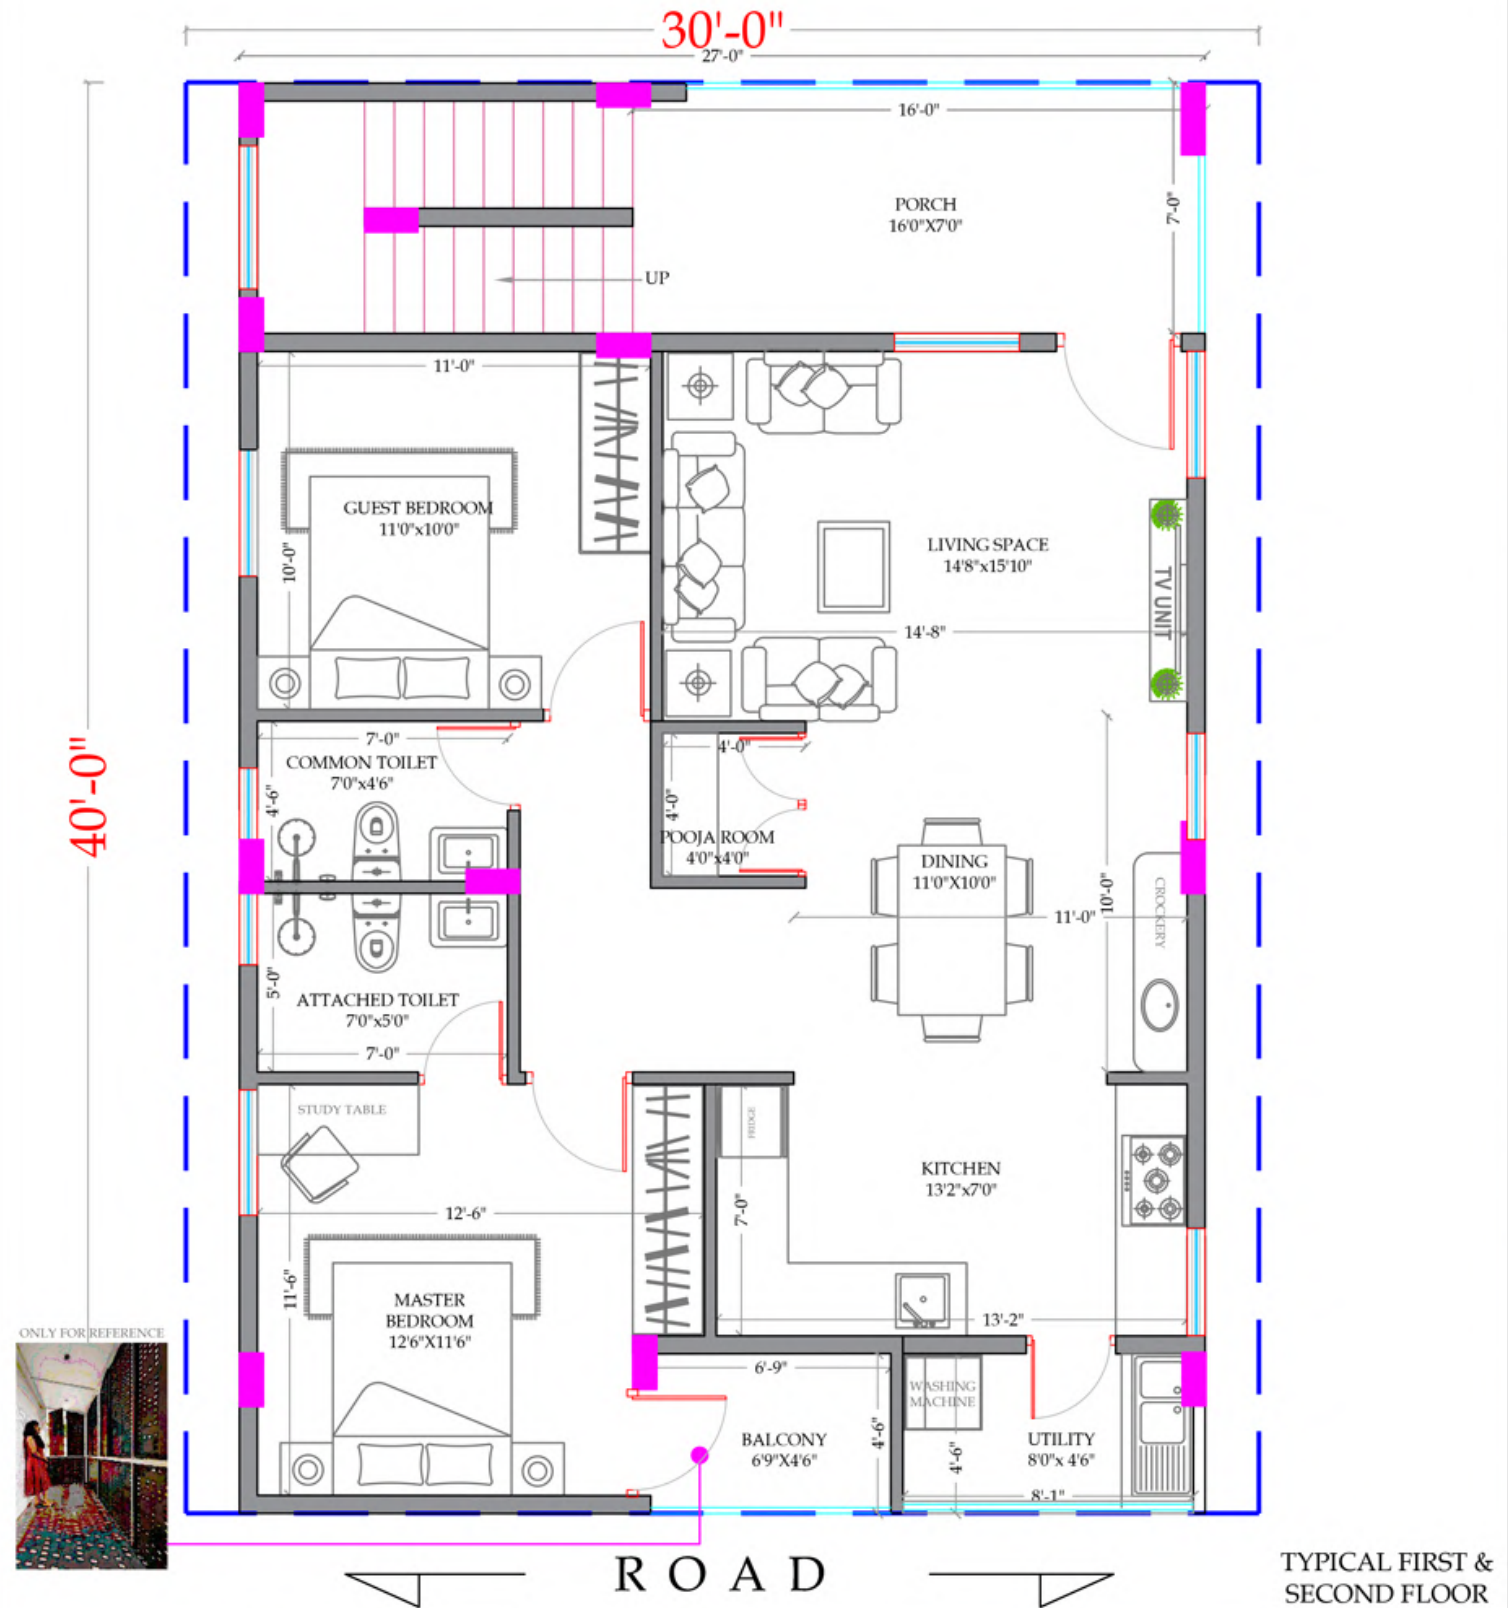


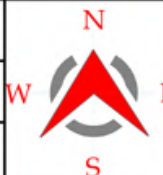NOTE The following has been considered w.r.t the floor plans given and the same will be considered for costing unless changed by client, which needs to be intimated to the architect handling the project which will further be intimated to the marketing team. 1. Floor to Floor height : 10' (includes slab) 2. Type of internal staircase : -- 3. Type of external staircase : Waist Slab 4. Plinth height (From N.G.L.) : +1'6" 5. No. of Floors constructed at present : G + 3.5 6. No. of Floors for Structural design : G + 3.5 7. External Wall : 6" SOLID BLOCK 8. Internal Wall : 4" SOLID BLOCK "If the relevant regulatory requirements or norms(Government rules) are not going to be met by the plan with respect to the building's setback. The client will be liable for any ensuing problems." "The site's dimensions and angle may change while it is being marked with a grid during execution."	PROPOSED RESIDENCE FOR : MR. PRAMOD .DP PROJECT NO.: 1693 OPTION NO. 01 <table><tr><th>Date</th><th>Revision NO</th><th>Reasons</th></tr><tr><td>04-04-2026</td><td>R-1</td><td>PROPOSED FLOOR PLANS</td></tr><tr><td>08-04-2026</td><td>R-2</td><td>Revision in Third floor and terrace floor, Bedroom is added in terrace floor</td></tr><tr><td>15-04-2026</td><td>R-3</td><td>Door position of toilet is interchanged and parallel wardrobe is added,columns are positioned</td></tr><tr><td colspan="3">DESIGNED BY : Ar. SORNA</td></tr><tr><td colspan="3">CHECKED BY : Ar. VIKAS</td></tr></table>			Date	Revision NO	Reasons	04-04-2026	R-1	PROPOSED FLOOR PLANS	08-04-2026	R-2	Revision in Third floor and terrace floor, Bedroom is added in terrace floor	15-04-2026	R-3	Door position of toilet is interchanged and parallel wardrobe is added,columns are positioned	DESIGNED BY : Ar. SORNA			CHECKED BY : Ar. VIKAS			SHEET NO. DATE :15-04-2026 SCALE : N.T.S LOCATION :  buildAhome A Virgo Group Company Scenic Beauty Homes Pvt Ltd. Address : Fourth Floor, CRN Chambers, 13, Kasturba Rd, Shanthala Nagar, Ashok Nagar, Bengaluru, Karnataka 560001 Ph no : +91-7090 0056 00 , +91-80-2351 1033 www.buildahome.in 
	Date	Revision NO	Reasons																			
	04-04-2026	R-1	PROPOSED FLOOR PLANS																			
	08-04-2026	R-2	Revision in Third floor and terrace floor, Bedroom is added in terrace floor																			
	15-04-2026	R-3	Door position of toilet is interchanged and parallel wardrobe is added,columns are positioned																			
	DESIGNED BY : Ar. SORNA																					
	CHECKED BY : Ar. VIKAS																					

/// FLOOR PLANS

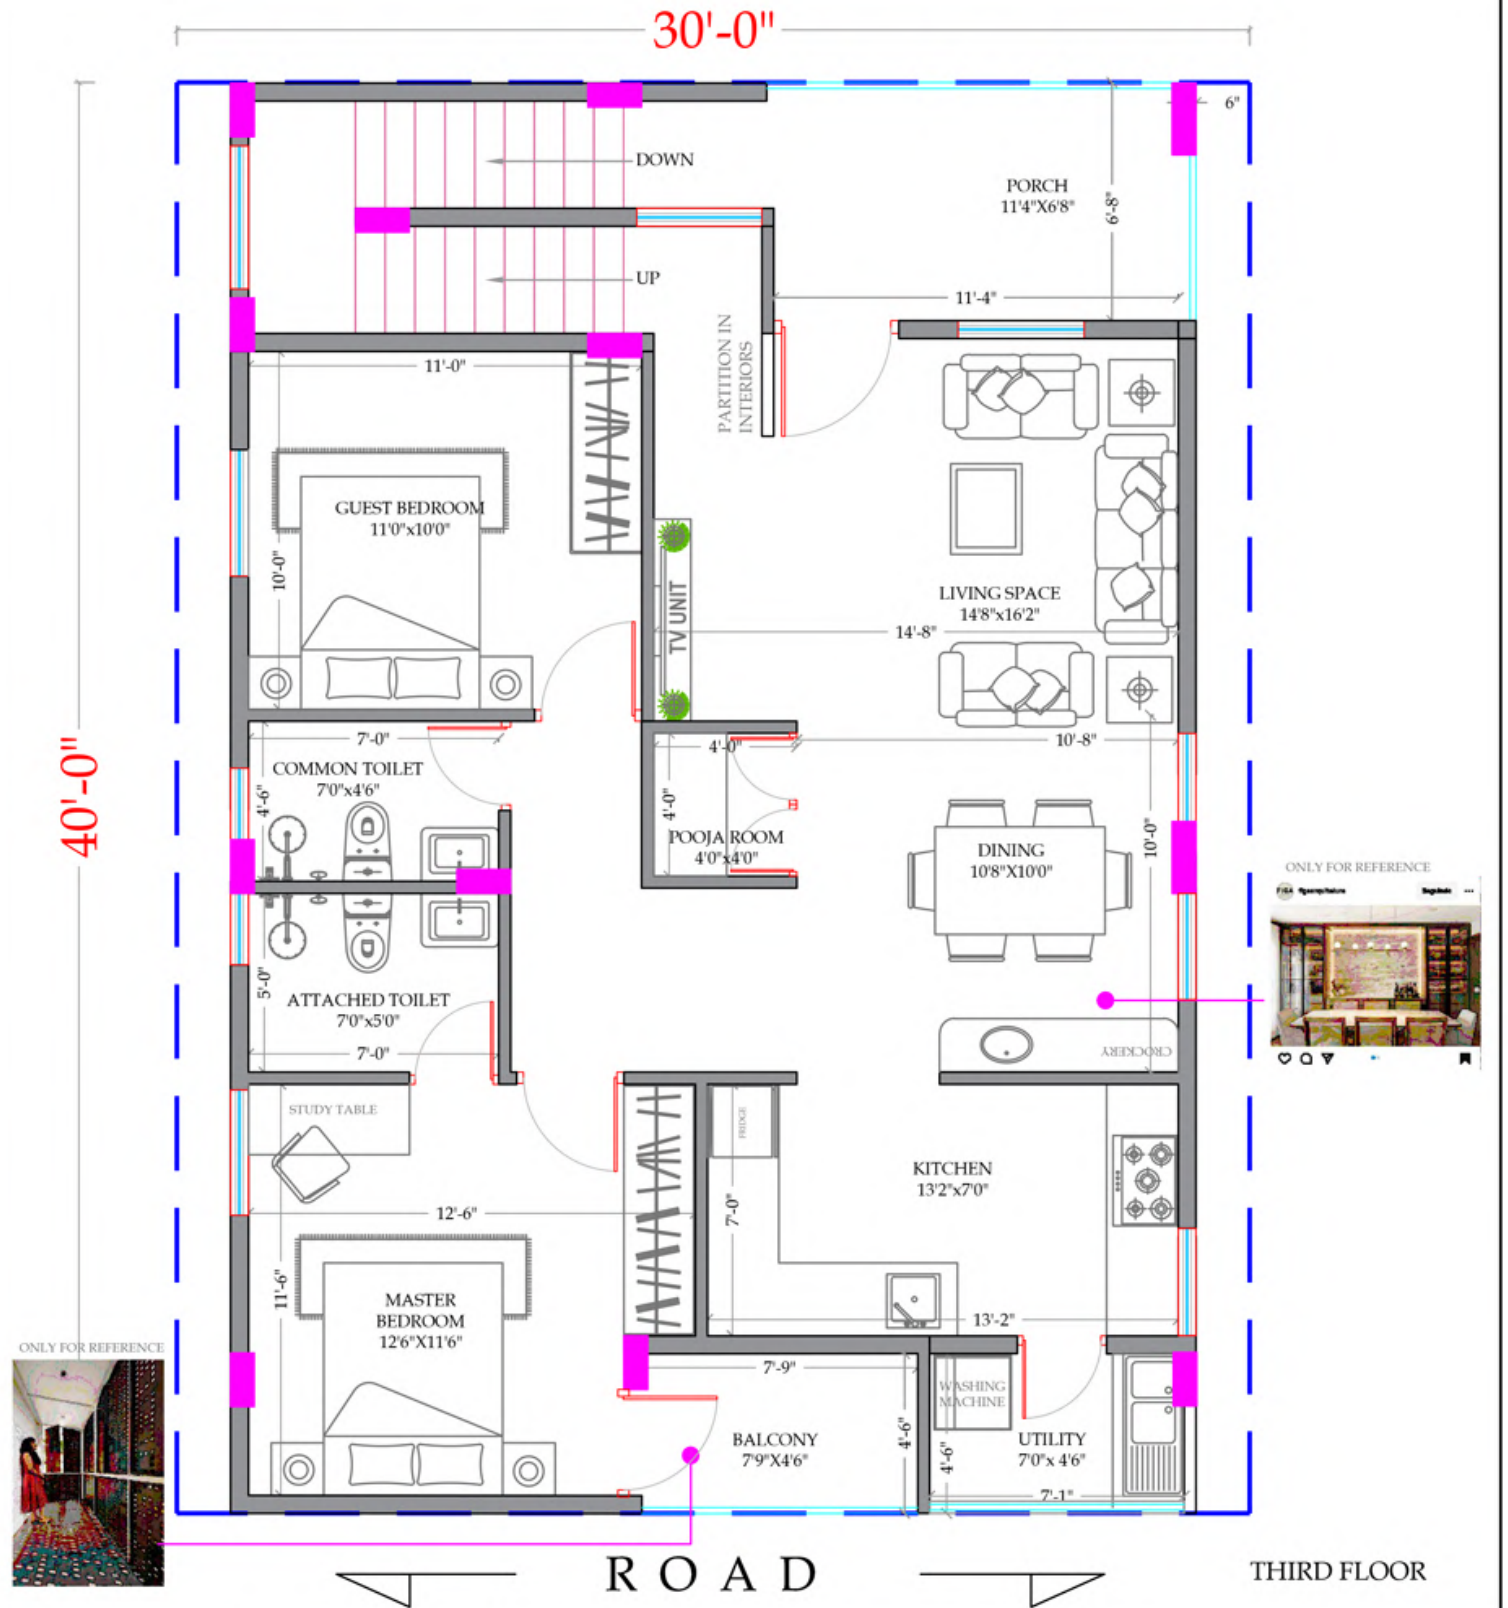

NOTE The following has been considered w.r.t the floor plans given and the same will be considered for costing unless changed by client, which needs to be intimated to the architect handling the project which will further be intimated to the marketing team. 1. Floor to Floor height : 10' (includes slab) 2. Type of internal staircase : -- 3. Type of external staircase : Waist Slab 4. Plinth height (From N.G.L.) : +1'6" 5. No. of Floors constructed at present : G + 3.5 6. No. of Floors for Structural design : G + 3.5 7. External Wall : 6" SOLID BLOCK 8. Internal Wall : 4" SOLID BLOCK If the relevant regulatory requirements or norms(Government rules) are not going to be met by the plan with respect to the building's setback. The client will be liable for any ensuing problems. The site's dimensions and angle may change while it is being marked with a grid during execution.	PROPOSED RESIDENCE FOR : MR. PRAMOD .DP PROJECT NO.: 1693 OPTION NO. 01 <table><thead><tr><th>Date</th><th>Revision NO</th><th>Reasons</th></tr></thead><tbody><tr><td>04-04-2026</td><td>R-1</td><td>PROPOSED FLOOR PLANS</td></tr><tr><td>08-04-2026</td><td>R-2</td><td>Revision in Third floor and terrace floor, Bedroom is added in terrace floor</td></tr><tr><td>15-04-2026</td><td>R-3</td><td>Door position of toilet is interchanged and parallel wardrobe is added, columns are positioned</td></tr><tr><td colspan="3">DESIGNED BY : Ar. SORNA</td></tr><tr><td colspan="3">CHECKED BY : Ar. VIKAS</td></tr></tbody></table>			Date	Revision NO	Reasons	04-04-2026	R-1	PROPOSED FLOOR PLANS	08-04-2026	R-2	Revision in Third floor and terrace floor, Bedroom is added in terrace floor	15-04-2026	R-3	Door position of toilet is interchanged and parallel wardrobe is added, columns are positioned	DESIGNED BY : Ar. SORNA			CHECKED BY : Ar. VIKAS			SHEET NO. DATE :15-04-2026 SCALE : N.T.S LOCATION :  buildAhome A Virgo Group Company Scenic Beauty Homes Pvt Ltd. Address : Fourth Floor, CRN Chambers, 13, Kasturba Rd, Shanthala Nagar, Ashok Nagar, Bengaluru, Karnataka 560001 Ph no : +91-7090 0056 00 , +91-80-2351 1033 www.buildahome.in	N W E S
	Date	Revision NO	Reasons																				
	04-04-2026	R-1	PROPOSED FLOOR PLANS																				
	08-04-2026	R-2	Revision in Third floor and terrace floor, Bedroom is added in terrace floor																				
	15-04-2026	R-3	Door position of toilet is interchanged and parallel wardrobe is added, columns are positioned																				
	DESIGNED BY : Ar. SORNA																						
CHECKED BY : Ar. VIKAS																							

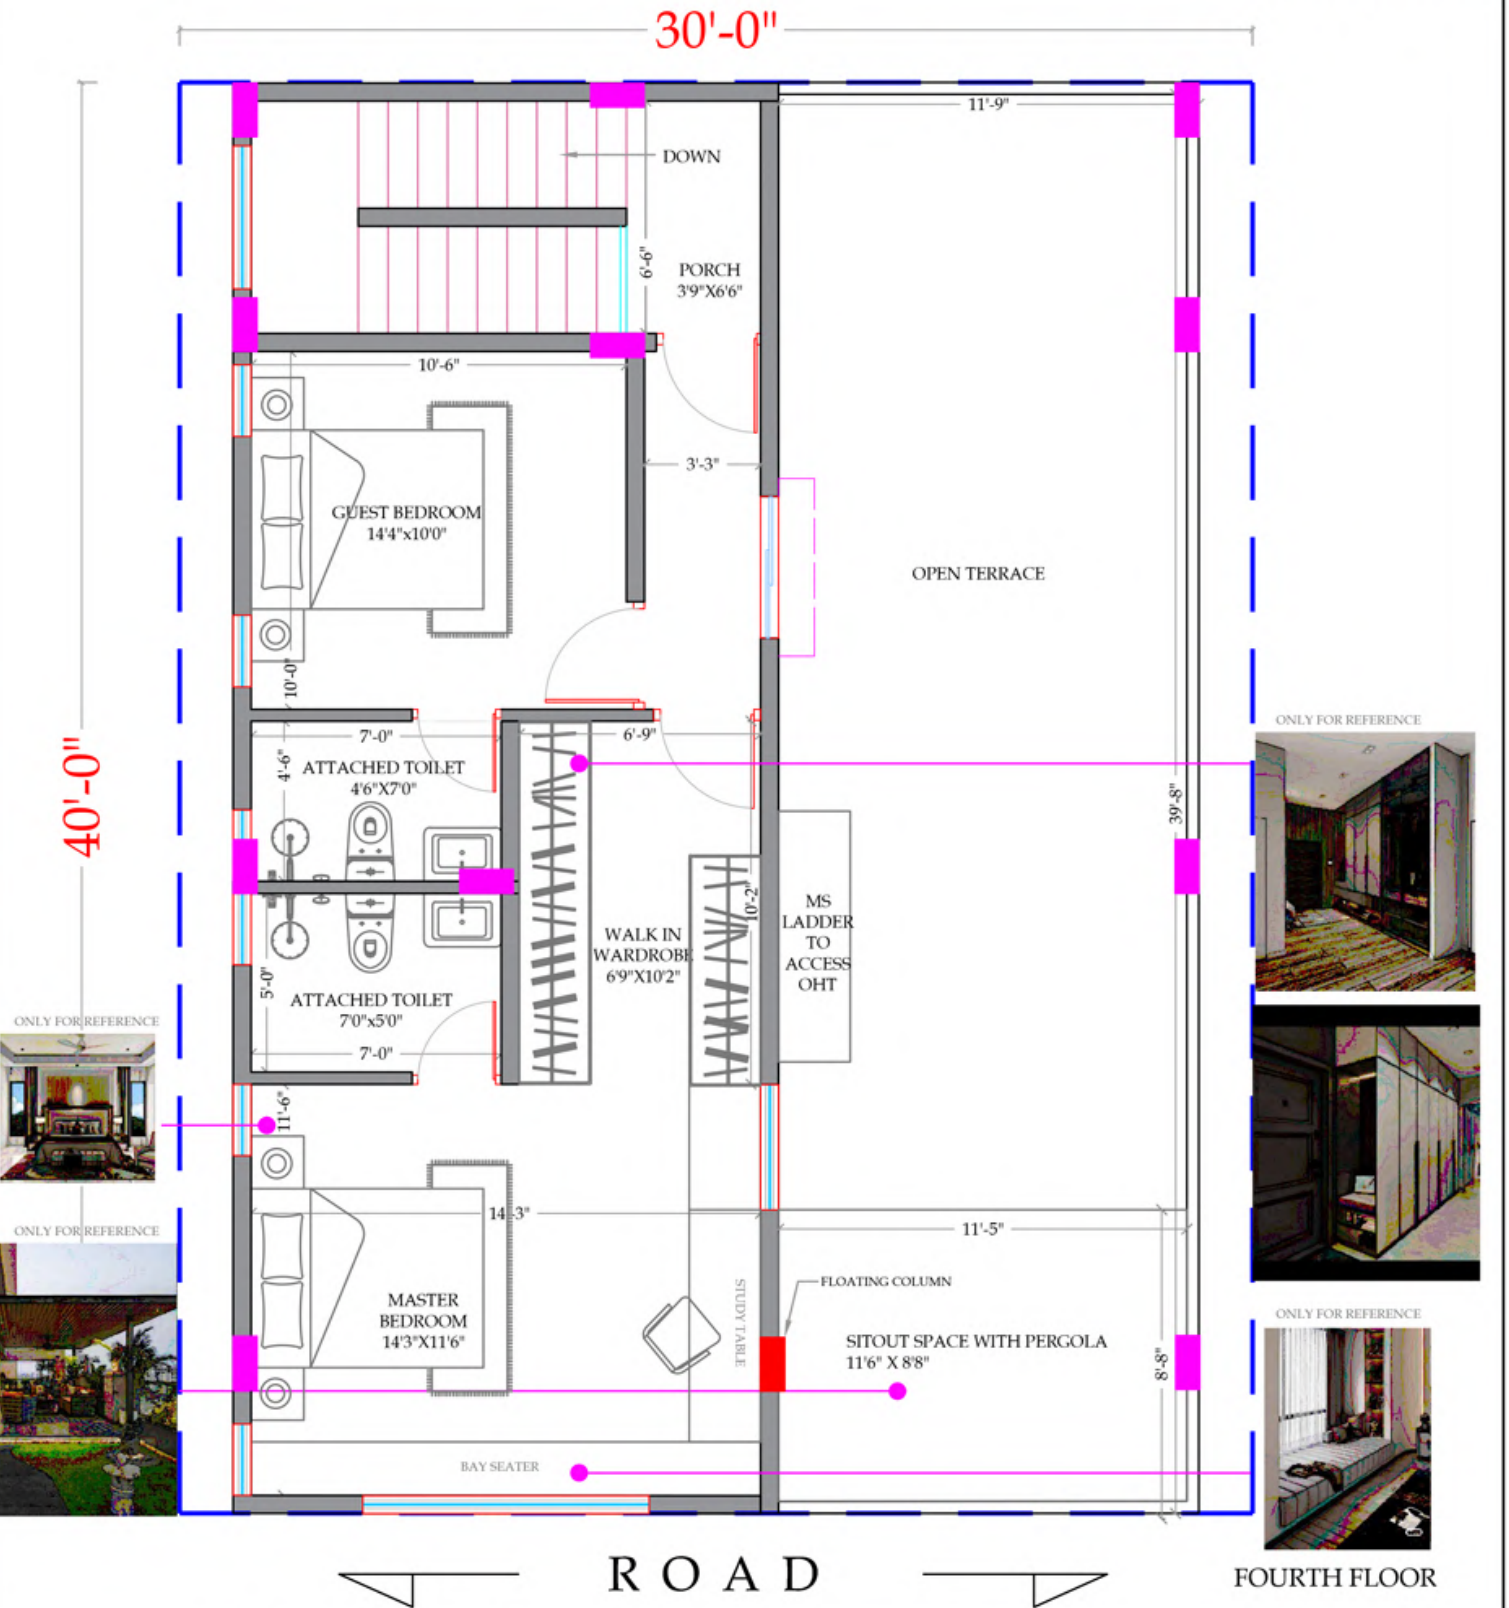

NOTE The following has been considered w.r.t the floor plans given and the same will be considered for costing unless changed by client, which needs to be intimated to the architect handling the project which will further be intimated to the marketing team. 1. Floor to Floor height : 10' (includes slab) 2. Type of internal staircase : -- 3. Type of external staircase : Waist Slab 4. Plinth height (From N.G.L.) : +1'6" 5. No. of Floors constructed at present : G + 3.5 6. No. of Floors for Structural design : G + 3.5 7. External Wall : 6" SOLID BLOCK 8. Internal Wall : 4" SOLID BLOCK If the relevant regulatory requirements or norms(Government rules) are not going to be met by the plan with respect to the building's setback. The client will be liable for any ensuing problems. The site's dimensions and angle may change while it is being marked with a grid during execution.	PROPOSED RESIDENCE FOR : MR. PRAMOD .DP PROJECT NO.: 1693 OPTION NO. 01 <table><tr><th>Date</th><th>Revision NO</th><th>Reasons</th></tr><tr><td>04-04-2026</td><td>R-1</td><td>PROPOSED FLOOR PLANS</td></tr><tr><td>08-04-2026</td><td>R-2</td><td>Revision in Third floor and terrace floor, Bedroom is added in terrace floor</td></tr><tr><td>15-04-2026</td><td>R-3</td><td>Door position of toilet is interchanged and parallel wardrobe is added, columns are positioned</td></tr><tr><td colspan="3">DESIGNED BY : Ar. SORNA</td></tr><tr><td colspan="3">CHECKED BY : Ar. VIKAS</td></tr></table>			Date	Revision NO	Reasons	04-04-2026	R-1	PROPOSED FLOOR PLANS	08-04-2026	R-2	Revision in Third floor and terrace floor, Bedroom is added in terrace floor	15-04-2026	R-3	Door position of toilet is interchanged and parallel wardrobe is added, columns are positioned	DESIGNED BY : Ar. SORNA			CHECKED BY : Ar. VIKAS			SHEET NO. DATE :15-04-2026 SCALE : N.T.S LOCATION :  buildAhome A Virgo Group Company Scenic Beauty Homes Pvt Ltd. Address : Fourth Floor, CRN Chambers, 13, Kasturba Rd, Shanthala Nagar, Ashok Nagar, Bengaluru, Karnataka 560001	N W E S 
	Date	Revision NO	Reasons																				
	04-04-2026	R-1	PROPOSED FLOOR PLANS																				
	08-04-2026	R-2	Revision in Third floor and terrace floor, Bedroom is added in terrace floor																				
	15-04-2026	R-3	Door position of toilet is interchanged and parallel wardrobe is added, columns are positioned																				
	DESIGNED BY : Ar. SORNA																						
	CHECKED BY : Ar. VIKAS																						
				Ph no : +91-7090 0056 00 , +91-80-2351 1033 www.buildahome.in																			

Area Statement of Mr.PRAMOD (1693) residence :
(The Premium Package)

BUILDING USE- RENTAL + SELF USE
Location - BANGLORE

FLOOR SPECIFICATIONS: G+3.5+OHT

Ground Floor -PARKING ,1BHK - LIVING , KITCHEN , UTILITY,
COMMON TOILET 1 BEDROOM , EXTERNAL STAIRCASE

First Floor -EXTERNAL STAIRCASE ,PORCH,LIVING, DINING,
KITCHEN, UTILITY, 1 BEDROOM WITH ATTACHED
TOILET, 1 BEDROOM WITH COMMON TOILET , BALCONY

Second Floor - EXTERNAL STAIRCASE ,PORCH,LIVING, DINING, KITCHEN,
UTILITY, 1 BEDROOM WITH ATTACHED TOILET, 1
BEDROOM WITH COMMON TOILET , BALCONY

Third Floor - EXTERNAL STAIRCASE TURNING TO INTERNAL
STAIRCASE ,PORCH,LIVING, DINING, KITCHEN,
UTILITY, 1 BEDROOM WITH ATTACHED TOILET, 1
BEDROOM WITH COMMON TOILET , BALCONY

Terrace Floor -STAIRCASE HEAD ROOM, 1 BEDROOM WITH ATTACHED
TOILET, 1 MASTER BEDROOM WITH WALK IN WARDROBE
AND ATTACHED TOILET, OPEN TERRACE , MS PERGOLA

STRUCTURAL DESIGN : G+3.5

Walls- 6" SOLID BLOCKS (external walls)

4" SOLID BLOCKS (internal walls)

AREA SPECIFICATION-FLOOR WISE:

1.Site Area - 1200 sq.ft

2. GF BUA : 434 sq.ft

a.Parking : 620 sq.ft

b. Setback : 146 sq.ft

3. Gf slab area : 1094 sqft (Excluding Sill & lintel projection)

4. FF slab area : 1084 sqft (Excluding Sill & lintel projection)

a. FF Sill projections : 2 sqft

b. FF Lintel projections : 2 sqft

5. SF slab area : 1084 sqft (Excluding Sill & lintel projection)

a. SF Sill projections : 1 sqft

b. SF Lintel projections : 1 sqft

6. TF slab area : 1084 sqft (Excluding Sill & lintel projection)

a. TF Sill projections : 2 sqft

b. TF Lintel projections : 2 sqft

7. Te.F slab area : 620 sqft

a. Te.F Sill projections : 2 sqft

b. Te.F Lintel projections : 2 sqft

7. OHT : Not required

8. Parapet wall - 174'0" Rft

9. Ug sump - as per proposal

PLINTH & FLOOR TO FLOOR HEIGHT SPECIFICATIONS:

10. Plinth ht +1'6" lvl from F.G.L - As per package

a-Site @ -6'0" From Road level (Site needs to be levelled)

b. Plinth ht +2'0" lvl from N.G.L

11. Floor to floor ht - 10'0"(Includes Slab)- As per package

PLUMBING SPECIFICATIONS:

-Kitchen - 04 Nos

-Toilets - 1 (GF) + 2 (FF) + 2(SF) + 2(TF) +2(Te.F)

Plumbing services- WEST & East

OPENING SPECIFICATIONS :

1. % OF OPENINGS: 29.18% (AS PER PACKAGE 20%)

2. TOTAL AREA OF OPENINGS -1256.75 sqft

DOORS :

a.Main Door : 693 sqft

b. Pooja Door : 98 sqft

c. Internal Door : 73.5sqft

WINDOWS :

a.Windows : 563.75 sqft

b.Ventilators : 536.75 sqft

c. Ventilators : 27 sqft

TYPE OF DOORS -Wood

TYPE OF WINDOWS - UPVC

COMPOUND WALL SPECIFICATIONS:

a.5 ft compound wall at South, North ,West &East

b.Ms gate : 15'0" RFT (1 No) 5'0" HEIGHT(VEHICULAR GATE)

OTHER SPECIFICATIONS:

1.MS ladder - 1 no. (access OHT)

2.(i)Type of external staircase - Waist slab staircase

(ii)Type of internal staircase - Waist slab staircase

3.Gas line provision - Not yet decided.

ELEVATION :

1.MS PERGOLA - 93 SQ.FT (REMOVED)

2.UTILITY - MS GRILLS - 152 SQ.FT

3.PAINT WITH GROOVES - 194 SQ.FT (Elevation surface area)

4.ROTATABLE VERTICAL FINS - (10 SQ FT EACH)- 4 NOS -

40 SQ.FT

5.FOLDING & MOVABLE VERTICAL FINS - 50 SQ.FT - 1 NOS

6.GLASS HANDRAIL - 7'9" RFT

7.MS RAILING - 18'6" RFT

1693 - SCHEDULE OF OPENINGS

SCHEDULE OF OPENING : DOORS

NAME	SIZE	SILL	DESCRIPTION	Floor					TeF	NO'S
				GF	FF	SF	TF			
MD	(3'6"x7'0")	----	MAIN DOOR	01	01	01	01	-	04	
PD	(3'6"x7'0")	----	POOJA DOOR	-	01	01	01	-	03	
D1	(3'0"x7'0")	----	BEDROOM DOOR	01	02	02	02	02	09	
D1-A	(3'0"x7'0")	----	BALCONY DOOR DOOR WITH THRESHOLD	-	01	01	01	-	03	
D2	(2'9"x7'0")	----	UTILITY DOOR DOOR WITH THRESHOLD	01	01	01	01	-	04	
D3	(2'6"x7'0")	----	TOILET DOOR	01	02	02	02	02	09	
SD	(5'0"x7'0")	----	TERRACE SLIDING DOOR	-	-	-	-	01	01	
TOTAL DOORS =										33

SCHEDULE OF OPENING : WINDOWS

									TeF	NO'S
				GF	FF	SF	TF			
W1	(8'0"x5'6")	1'-6"	WINDOW	-	-	-	-	01	01	
W2	(4'0"x4'6")	2'-6"	WINDOW	01	04	04	04	01	14	
W3	(3'0"x4'6")	2'-6"	WINDOW	01	01	01	02	-	05	
W4	(2'0"x4'6")	2'-6"	WINDOW	01	-	-	-	04	05	
W5	(1'6"x4'6")	2'-6"	WINDOW	-	01	01	01	-	03	
KW	(3'0"x4'0")	3'-0"	KITCHEN WINDOW	01	01	01	01	-	04	
SW	(4'0"x3'0")	7'-0"	STAIRCASE WINDOW	01	01	01	01	01	05	
V	(2'0"x1'6")	7'-0"	VENTILATOR	01	02	02	02	02	09	
TOTAL WINDOWS =										46



1693 - MR.PRAMOD .DP & FAMILY						
SL.NO	PARTICULARS	X	Y	X*Y	NO.	TOTAL
1	MD	3.5	7	24.5	4	98
2	PD	3.5	7	24.5	3	73.5
3	D1	3	7	21	9	189
4	D1-A	3	7	21	3	63
5	D2	2.75	7	19.25	4	77
6	D3	2.5	7	17.5	9	157.5
7	SD	5	7	35	1	35
					33	
						521.5
1	W1	8	5.5	44	1	44
2	W2	4	4.5	18	14	252
3	W3	3	4.5	13.5	5	67.5
4	W4	2	4.5	9	5	45
5	W5	1.5	4.5	6.75	3	20.25
6	KW	3	4	12	4	48
7	SW	4	3	12	5	60
8	V	2	1.5	3	9	27
					46	
						1256.75
TOTAL AREA OF OPENING						1256.75
% OF OPENING						29.18602
20% OF OPENING ACCORDING TO PACKAGE						861.2
DIFFERENCE						395.55

CLIENT NAME: PRAMOD DP

CHECKED : Ar. VIKAS

DESIGNED : KEERTHISH G

DATE : 29-04-2026

AREA STATEMENT & ELEVATION



buildAhome
A Village Group Company
Scenic Beauty Homes Pvt
Ltd.
Address : Fourth Floor, CRN Chambers,
13, Kasturba Rd, Shanthala Nagar,
Ashok Nagar,
Bengaluru, Karnataka 560001

// AREA STATEMENT & ELEVATIONS



OPTION - 1



OPTION - 2



31



NOTE :

THIS DRAWING IS THE EXCLUSIVE PROPERTY OF
"BUILDAHOME" ,AND THE REPRODUCTION OF ANY PART WITHOUT PRIOR
WRITTEN CONSENT FROM THIS OFFICE IS A VIOLATION OF APPLICABLE LAW

NOTE




DRAWING NAME : SECOND FLOOR & TERRACE FLOOR




NOTE :

THIS DRAWING IS THE EXCLUSIVE PROPERTY OF
"BUILDAHOMES" AND THE REPRODUCTION OF ANY PART WITHOUT PRIOR
WRITTEN CONSENT FROM THIS OFFICE IS A VIOLATION OF APPLICABLE


NOTE :

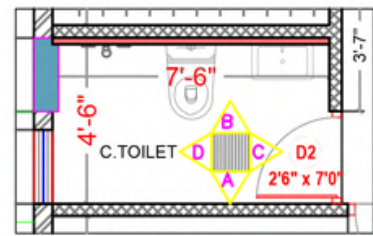

PLAN

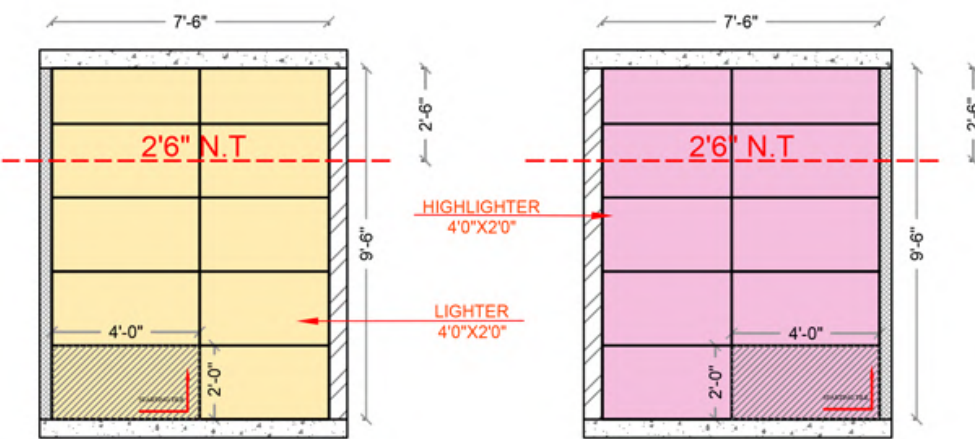

A WALL ELEVATION B WALL ELEVATION

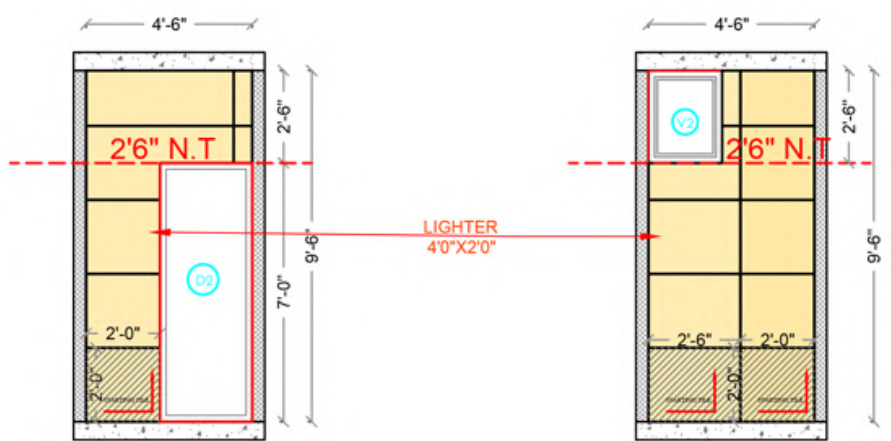

C WALL ELEVATION D WALL ELEVATION


CONSTRUCTION NOTE :

The following has been considered w.r.t the floor plans given and the same will be considered for costing unless changed by client, which needs to be intimated to the architect handling the project which will further be intimated to the marketing team.

1. Floor to Floor height : 10'0" (includes slab)
2. Type of internal staircase : WAIST SLAB STAIRCASE
3. Type of external staircase : WAIST SLAB STAIRCASE
4. Plinth height (From N.G.L.) : + 1'6"
5. No. of Floors constructed at present : G +2.5
6. No. of Floors for Structural design :As built
7. External Wall : 6" BRICK WALL.
8. Internal Wall : 4" BRICK WALL.

WALL TILE DETAILS:1384

LEGENDS :

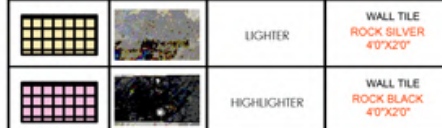

CONSULTANT:
buildAhome
A Virgo Group Company
Scenic Beauty Homes Pvt Ltd.
Address : 552, 7th Main Road, AGS Layout,
Dollars Colony, R.M.V. 2nd Stage,
Bengaluru, Karnataka 560094
Ph no : +91-7090 0056 00, +91-80-2351 1033
www.buildahome.in

DRAWING NO:


SHEET NO 001
SCALE NOT TO SCALE
CHECKED THIRUMOORTH
DRAWN KEERTHISH G
DATE 14-07-2026

ARCHITECTURAL DRAWING


NOTE :
THIS DRAWING IS THE EXCLUSIVE PROPERTY OF "BUILD-AHOME" AND THE REPRODUCTION OF ANY PART WITHOUT PRIOR WRITTEN CONSENT FROM THIS OFFICE IS A VIOLATION OF APPLICABLE LAWS.

CLIENT NAME : RAJANIKANTH @ BANGALORE
DRAWING NAME: GROUND FLOOR C.TOILET WALL TILE DETAILS


1. All dimensions are in feet and inches unless otherwise specified.
2. Drawing is not to scale, hence follow the dimensions mentioned.
3.Changes in the drawing should not be made without the notice of the project head and/or architect handling the project.

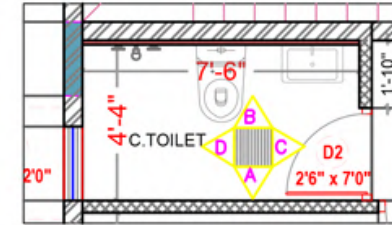

PLAN

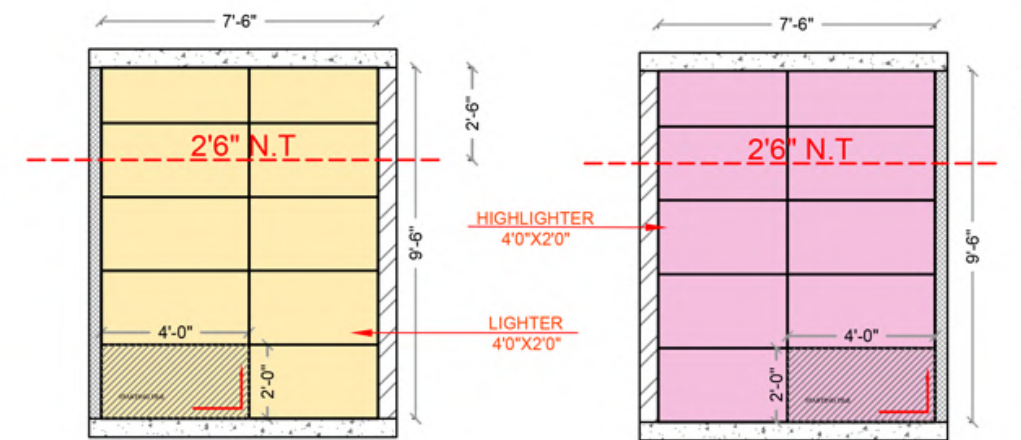

A WALL ELEVATION B WALL ELEVATION

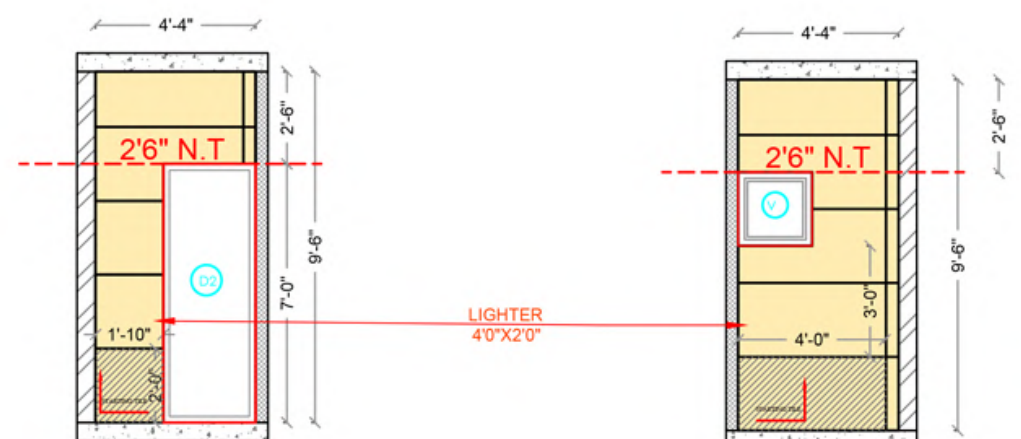

C WALL ELEVATION D WALL ELEVATION


CONSTRUCTION NOTE :

The following has been considered w.r.t the floor plans given and the same will be considered for costing unless changed by client, which needs to be intimated to the architect handling the project which will further be intimated to the marketing team.

1. Floor to Floor height : 10'0" (includes slab)
2. Type of internal staircase : WAIST SLAB STAIRCASE
3. Type of external staircase : WAIST SLAB STAIRCASE
4. Plinth height (From N.G.L.) : + 1'6"
5. No. of Floors constructed at present : G +2.5
6. No. of Floors for Structural design :As built
7. External Wall : 6" BRICK WALL.
8. Internal Wall : 4" BRICK WALL.

WALL TILE DETAILS:1384

LEGENDS :

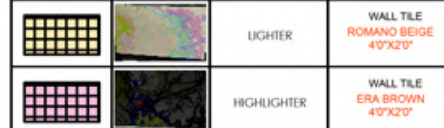

CONSULTANT:
buildAhome
A Virgo Group Company
Scenic Beauty Homes Pvt Ltd.
Address : 552, 7th Main Road, AGS Layout,
Dollars Colony, R.M.V. 2nd Stage,
Bengaluru, Karnataka 560094
Ph no : +91-7090 0056 00, +91-80-2351 1033
www.buildahome.in

DRAWING NO:


SHEET NO 002
SCALE NOT TO SCALE
CHECKED THIRUMOORTH
DRAWN KEERTHISH G
DATE 14-07-2026

ARCHITECTURAL DRAWING


NOTE :
THIS DRAWING IS THE EXCLUSIVE PROPERTY OF "BUILD-AHOME" AND THE REPRODUCTION OF ANY PART WITHOUT PRIOR WRITTEN CONSENT FROM THIS OFFICE IS A VIOLATION OF APPLICABLE LAWS.

CLIENT NAME : RAJANIKANTH @ BANGALORE
DRAWING NAME: FIRST FLOOR C.TOILET WALL TILE DETAILS


1. All dimensions are in feet and inches unless otherwise specified.
2. Drawing is not to scale, hence follow the dimensions mentioned.
3.Changes in the drawing should not be made without the notice of the project head and/or architect handling the project.

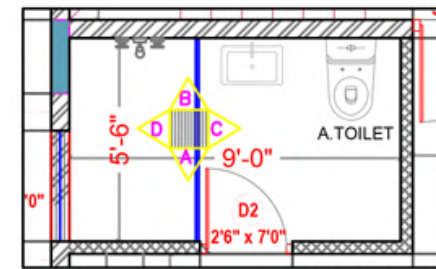

PLAN

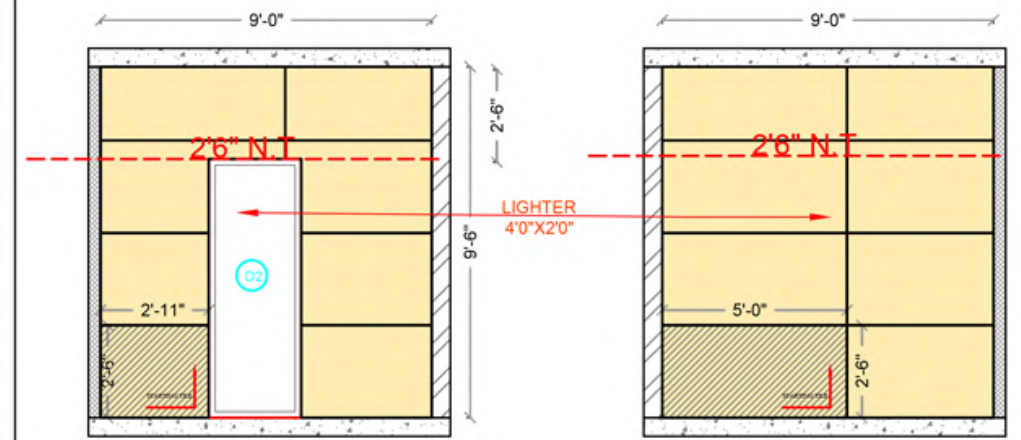

A WALL ELEVATION B WALL ELEVATION

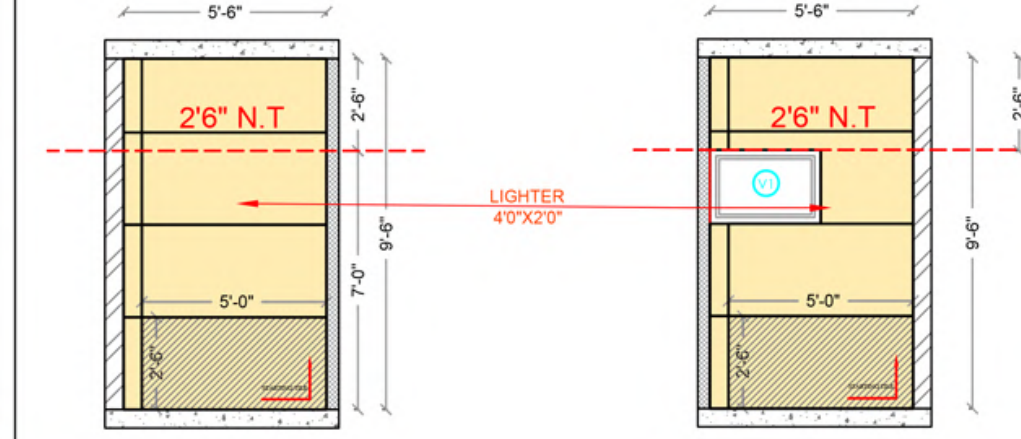

C WALL ELEVATION D WALL ELEVATION

CONSTRUCTION NOTE :

The following has been considered w.r.t the floor plans given and the same will be considered for costing unless changed by client, which needs to be intimated to the architect handling the project which will further be intimated to the marketing team.

1. Floor to Floor height : 10'0" (includes slab)
2. Type of internal staircase : WAIST SLAB STAIRCASE
3. Type of external staircase : WAIST SLAB STAIRCASE
4. Plinth height (From N.G.L.) : + 1'6"
5. No. of Floors constructed at present : G +2.5
6. No. of Floors for Structural design :As built
7. External Wall : 6" BRICK WALL.
8. Internal Wall : 4" BRICK WALL.

WALL TILE DETAILS:1384

LEGENDS :



CONSULTANT:
buildAhome
A Virgo Group Company
Scenic Beauty Homes Pvt Ltd.
Address : 552, 7th Main Road, AGS Layout,
Dollars Colony, R.M.V. 2nd Stage,
Bengaluru, Karnataka 560094
Ph no : +91-7090 0056 00, +91-80-2351 1033
www.buildahome.in

DRAWING NO:


SHEET NO 003
SCALE NOT TO SCALE
CHECKED THIRUMOORTH
DRAWN KEERTHISH G
DATE 14-07-2026

ARCHITECTURAL DRAWING


NOTE :
THIS DRAWING IS THE EXCLUSIVE PROPERTY OF "BUILD-AHOME" AND THE REPRODUCTION OF ANY PART WITHOUT PRIOR WRITTEN CONSENT FROM THIS OFFICE IS A VIOLATION OF APPLICABLE LAWS.

CLIENT NAME : RAJANIKANTH @ BANGALORE
DRAWING NAME: SECOND FLOOR MASTER BEDROOM A.TOILET WALL TILE DETAILS


1. All dimensions are in feet and inches unless otherwise specified.
2. Drawing is not to scale, hence follow the dimensions mentioned.
3.Changes in the drawing should not be made without the notice of the project head and/or architect handling the project.

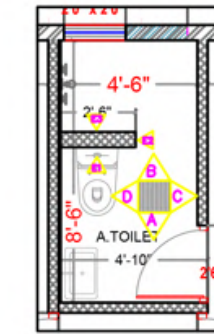

PLAN

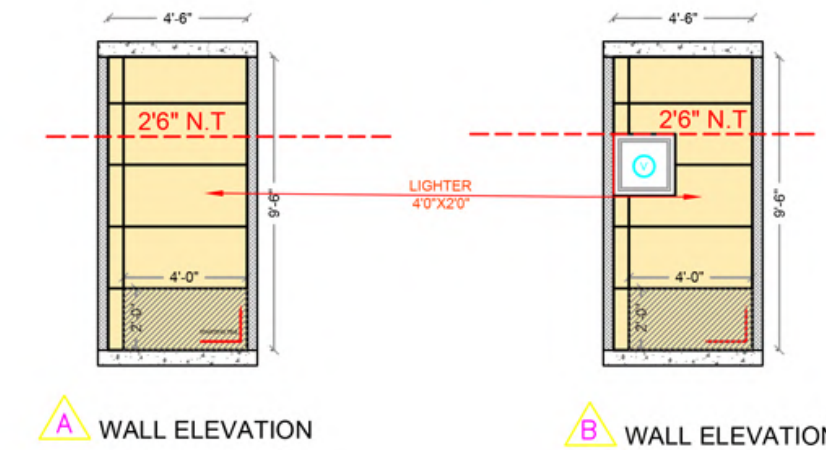

A WALL ELEVATION B WALL ELEVATION

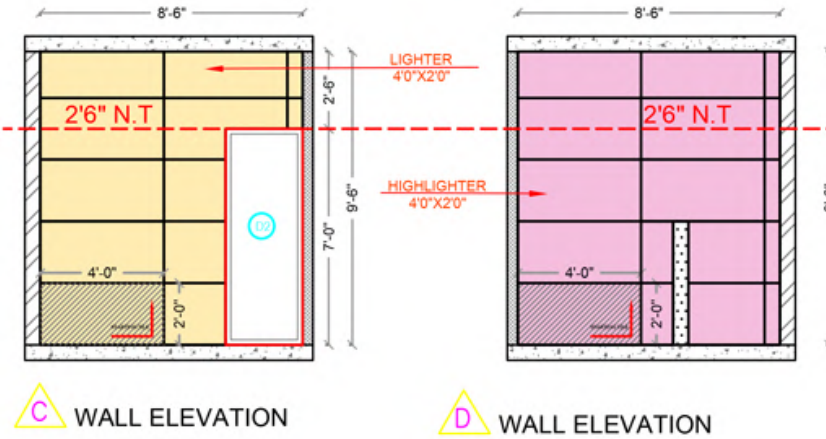

C WALL ELEVATION D WALL ELEVATION



E1 WALL ELEVATION E2 WALL ELEVATION


CONSTRUCTION NOTE :

The following has been considered w.r.t the floor plans given and the same will be considered for costing unless changed by client, which needs to be intimated to the architect handling the project which will further be intimated to the marketing team.

1. Floor to Floor height : 10'0" (includes slab)
2. Type of internal staircase : WAIST SLAB STAIRCASE
3. Type of external staircase : WAIST SLAB STAIRCASE
4. Plinth height (From N.G.L.) : + 1'6"
5. No. of Floors constructed at present : G +2.5
6. No. of Floors for Structural design :As built
7. External Wall : 6" BRICK WALL.
8. Internal Wall : 4" BRICK WALL.

WALL TILE DETAILS:1384

LEGENDS :

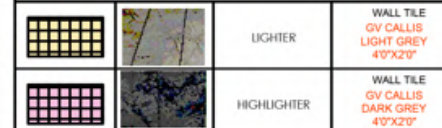

CONSULTANT:
buildAhome
A Virgo Group Company
Scenic Beauty Homes Pvt Ltd.
Address : 552, 7th Main Road, AGS Layout,
Dollars Colony, R.M.V. 2nd Stage,
Bengaluru, Karnataka 560094
Ph no : +91-7090 0056 00, +91-80-2351 1033
www.buildahome.in

DRAWING NO:

SHEET NO 002
SCALE NOT TO SCALE
CHECKED THIRUMOORTH
DRAWN KEERTHISH G
DATE 14-07-2026

ARCHITECTURAL DRAWING

NOTE :
THIS DRAWING IS THE EXCLUSIVE PROPERTY OF "BUILD-AHOME" AND THE REPRODUCTION OF ANY PART WITHOUT PRIOR WRITTEN CONSENT FROM THIS OFFICE IS A VIOLATION OF APPLICABLE LAWS.

CLIENT NAME : RAJANIKANTH @ BANGALORE
DRAWING NAME: SECOND FLOOR SON'S BEDROOM A.TOILET WALL TILE DETAILS

1. All dimensions are in feet and inches unless otherwise specified.
2. Drawing is not to scale, hence follow the dimensions mentioned.
3.Changes in the drawing should not be made without the notice of the project head and/or architect handling the project.

/// TILE DRAWING

PLEASE NOTE :
The following has been considered w.r.t the floor plans given and the same will be considered for costing unless changed by client, which needs to be intimated to the architect handling the project which will further be intimated to the marketing team.

1. Floor to Floor height : 10' (includes slab)
2. Type of internal staircase : Waist Slab
3. Type of external staircase : -
4. Plinth height (From N.G.L) : +2'0"
5. No: of Floors constructed at present : G+1
6. No: of Floors for Structural design : G+1
7. External Wall : 6" ,SOLID BLOCK
8. Internal Wall : 4" ,SOLID BLOCK

LEGEND :	
	8" SOLID BLOCK WORK
	6" SOLID BLOCK WORK
	4" SOLID BLOCK WORK
	4" SOLID BLOCK WORK-5' HT
	4" THK SOLIDBLOCK PARAPET WALL - 3' HT
	BEAM BOTTOM PROJECTION
	SLAB PROJECTION
	MS SECTION
	SILL PROJECTION
	EXPOSED BEAMS

CLIENT NAME : MRS.SHILPA		
DRAWING NAME: 2D ELEVATION		
REVISIONS :		
NAME	DESCRIPTION	DATE
R1	ELEVATION DRAWING	20-05-2026
R2		
R3		
R4		






buildAhome
A Virgo Group Company
Scenic Beauty Homes Pvt Ltd.
Address : Fourth Floor, CRN Chambers, 13, Kasturba Rd, Shanthala Nagar, Ashok Nagar, Bengaluru, Karnataka 560001

DRAWING NO:
BAH/2025/1449ARCH/LVL1/001/--/-----/R0

SHEET NO : 001		
SCALE : NOT TO SCALE		
CHECKED : Ar. VIKAS		
DESIGNED : Ar. SORNA		
DRAWN : KEERTHISH G		
DATE : 20-05-2026		
ARCHITECTURAL DRAWING		
NOTE : THIS DRAWING IS THE EXCLUSIVE PROPERTY OF "BUILDHOME" AND THE REPRODUCTION OF ANY PART WITHOUT PRIOR WRITTEN CONSENT FROM THIS OFFICE IS A VIOLATION OF APPLICABLE LAWS.		

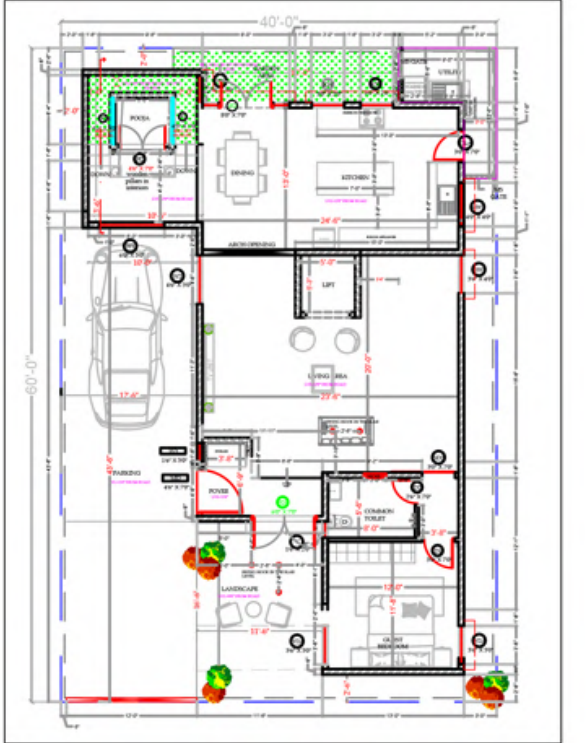


WEST ELEVATION


 HPL CLADDING
 TILE CLADDING
 GLASS HANDRAIL

// 2D ELEVATION & WINDOW DETAILS


W- 8'0"X5'0" NO'S-01
SILL LEVEL @ 2'0"

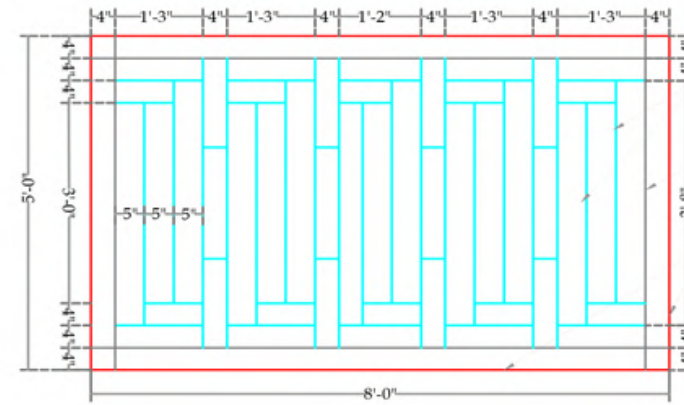


W1 - 6'0"X5'0" NO'S-02
SILL LEVEL @ 2'0"

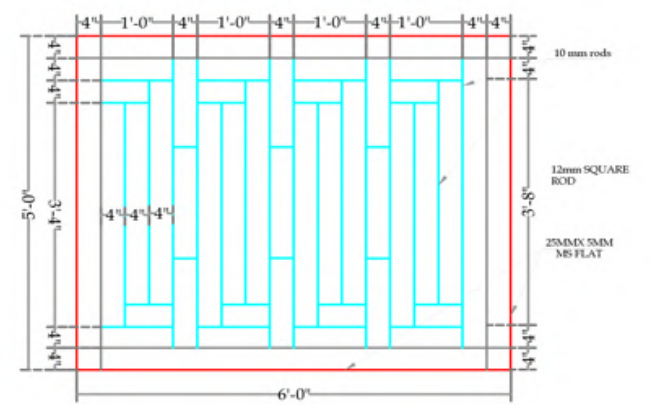


W2 - 4'6"X5'0" NO'S-02
SILL LEVEL @ 2'0"

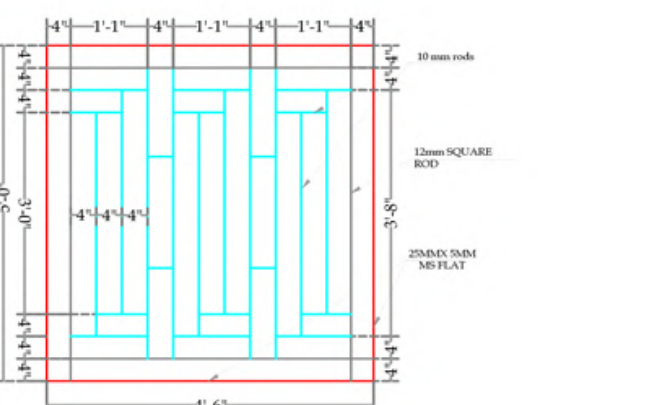


W2A - 4'0"X5'0" NO'S-02
SILL LEVEL @ 2'0"

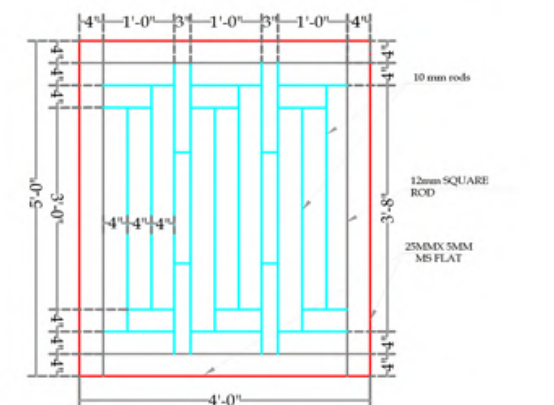


W3 - 3'0"X5'0" NO'S-05
SILL LEVEL @ 2'0"

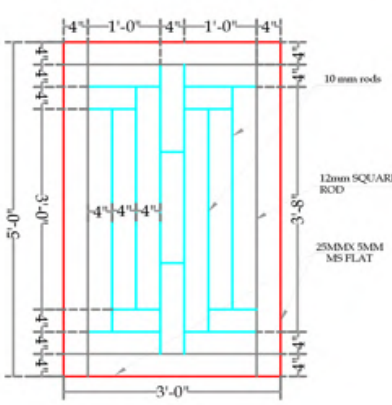


W4 - 2'6"X5'0" NO'S-01
SILL LEVEL @ 2'0"

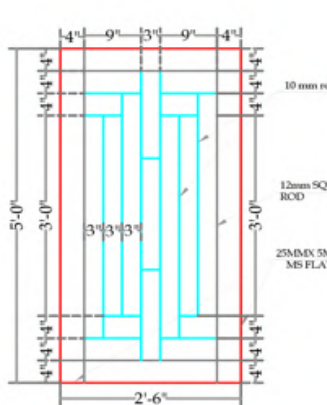


W5 - 1'6"X5'0" NO'S-01
SILL LEVEL @ 2'0"

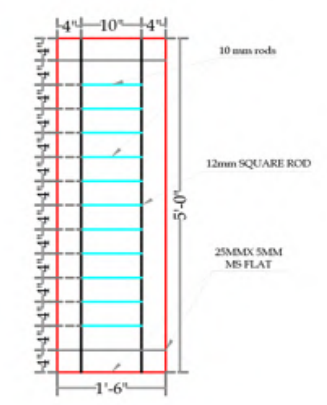


FG - 4'3"X5'0" NO'S-02
SILL LEVEL @ 2'0"

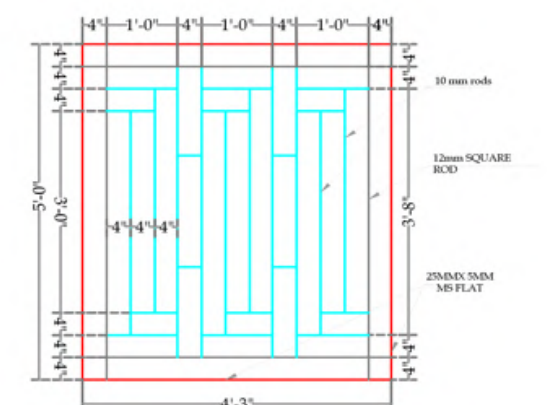


SW - 3'6"X4'0" NO'S-03
SILL LEVEL @ 3'0"

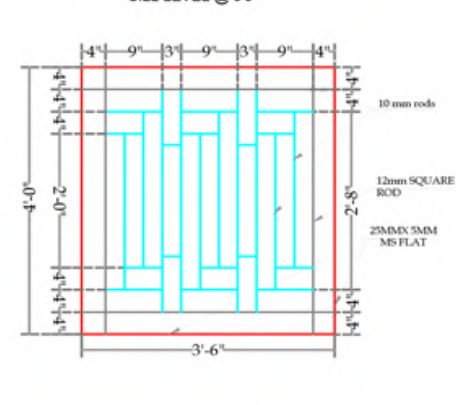


KW - 3'0"X2'0" NO'S-02
SILL LEVEL @ 3'0"

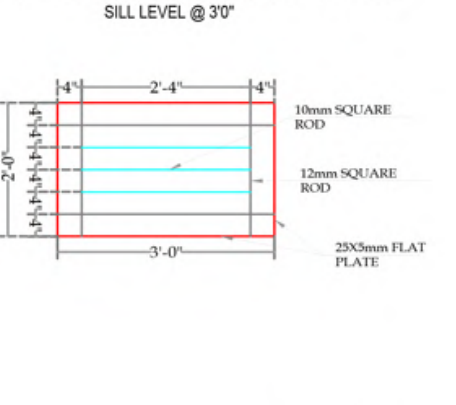


KW1 - 4'0"X4'0" NO'S-01
SILL LEVEL @ 3'0"

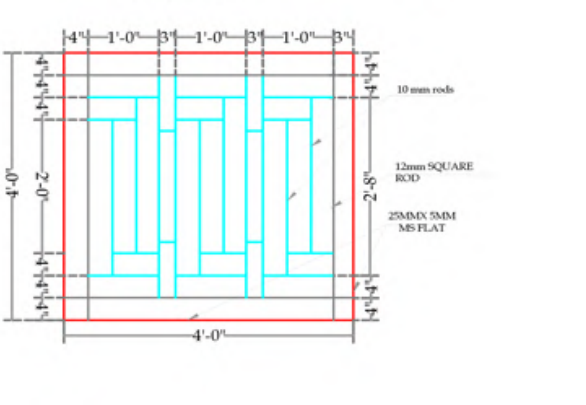

V- 1'6"X2'0" NO'S - 01
SILL LEVEL @ 5'0"

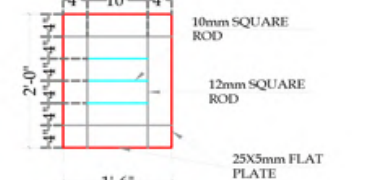

V1- 3'0"X2'0" NO'S - 03
SILL LEVEL @ 5'0"

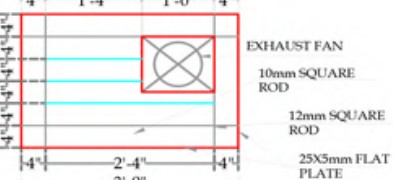


GENERAL NOTES :
1. All dimensions are in feet and inches unless otherwise specified.
2. Drawing is not to scale, hence follow the dimensions mentioned.
3.Changes in the drawing should not be made without the notice of the project head and/or architect handling the project.

CLIENT NAME: MISS.SHILPA
DRAWING NAME: WINDOW GRILL DETAILS

Revised Schedule of

NAME	SIZE	SILL	DESCRIPTION	FLOOR	No.
MD	(4'6" X 7'0")	----	Main Door	1+0+0	01
DI	(3'0" X 7'0")	----	Bedroom Door	1+0+0	06
D1A	(3'0" X 7'0")	----	Terrace & Utility Door	1+0+0	02
D2	(2'6" X 7'0")	----	Toilet Door	1+0+0	04
PD	(4'6" X 7'0")	----	Pooja Door	1+0+0	01
FD	(8'0" X 7'0")	----	French Door	1+0+0	01
SD2	(3'0" X 7'0")	----	Sliding Door	1+0+0	04
FD1	(6'0" X 7'0")	----	French Door	1+0+0	02
W	(8'0" X 5'0")	2'-0"	Window	0+1+0	01
W1	(6'0" X 5'0")	2'-0"	Window	2+0+0	02
W2	(4'6" X 5'0")	2'-0"	Window	2+0+0	02
W2A	(3'6" X 5'0")	2'-0"	Window	2+0+0	02
W3	(3'0" X 5'0")	2'-0"	Window	0+4+1	03
W4	(2'6" X 5'0")	2'-0"	Window	1+0+0	01
W5	(1'6" X 5'0")	2'-0"	Window	2+0+0	01
SW	(3'6" X 4'0")	3'-0"	Window	2+0+0	03
KW	(3'0" X 2'0")	3'-0"	KITCHEN WINDOW	2+0+0	02
KW1	(4'0" X 4'0")	3'-0"	KITCHEN WINDOW	1+0+0	01
V1	(3'0" X 2'0")	5'-0"	VENTILATOR	2+0+0	03
V	(1'6" X 2'0")	5'-0"	VENTILATOR	2+0+0	01
FG	(4'3" X 5'0")	2'-0"	FIXED GLASS	2+0+0	02

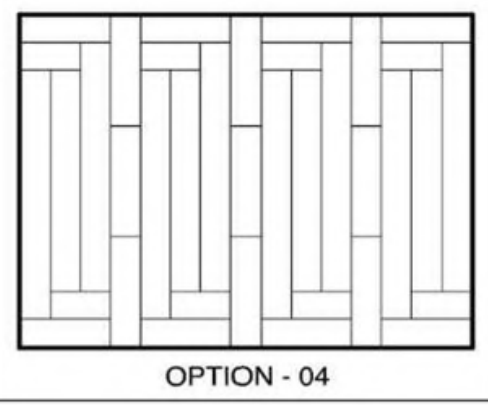REFERENCE IMAGE :


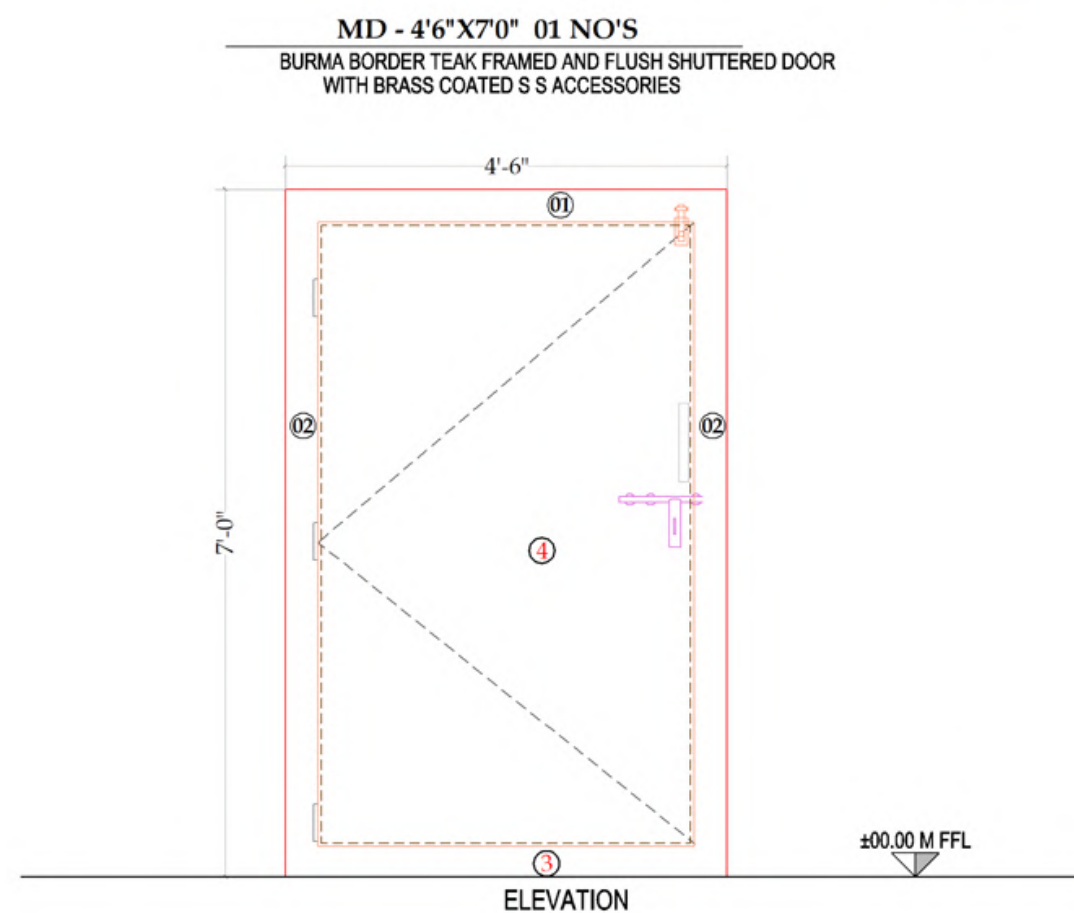
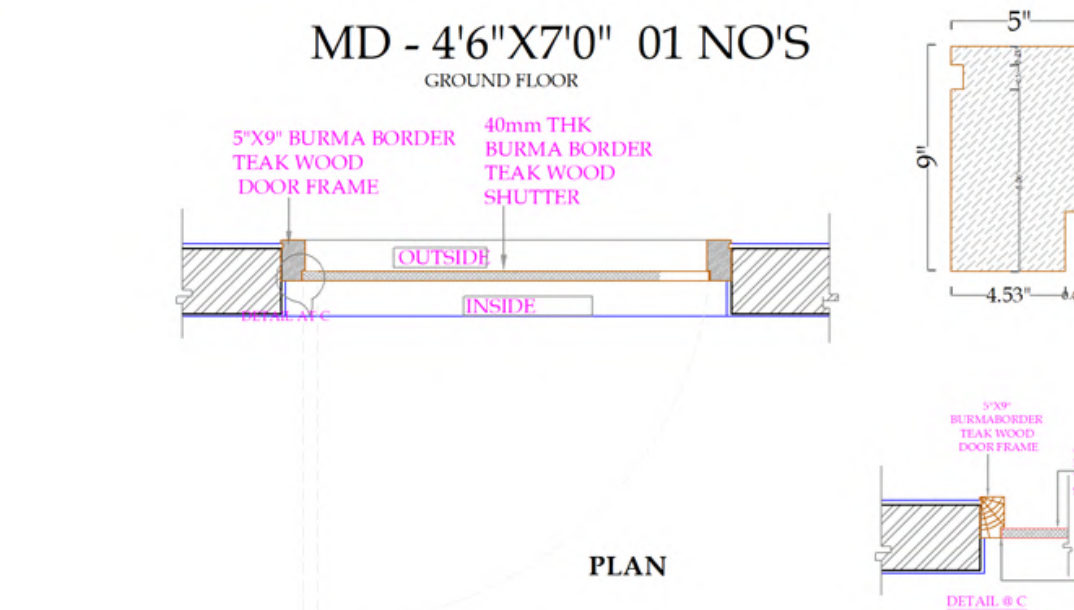
CONSULTANT:


buildAhome
A Virgo Group Company
Scenic Beauty Homes Pvt Ltd.
Address : #552, 7th Main, AGS layout, Dollars colony, RMV Stage 2nd Stage, Bangalore
Ph no : +91-7990 0056 00, +91-80-2351 1033
www.buildahome.in

DRAWING NO: BAH/1449/KRI/2022/ARCH/WD001


SHEET NO : 001	
SCALE : NOT TO SCALE	
CHECKED : Ar.SORNA	
DRAWN : KEERTHISH G	
DATE : 14.05.2026	
ARCHITECTURAL DRAWING	

NOTE :
THIS DRAWING IS THE EXCLUSIVE PROPERTY OF "BUILDHOME" AND THE REPRODUCTION OF ANY PART WITHOUT PRIOR WRITTEN CONSENT FROM THIS OFFICE IS A VIOLATION OF APPLICABLE LAWS.




NO	DISCRPTION OF ITEM	REF	QTY	SPECIFICATIONS
A.FRAME SECTION :-				
01	TOP FRAME	01	01	5" X 9" BURMA BORDER TEAK WOOD FRAME SECTION
02	SIDE FRAME	02	02	5" X 9" BURMA BORDER TEAK WOOD FRAME SECTION
03	BOTTOM FRAME	03	01	5" X 9" BURMA BORDER TEAK WOOD FRAME SECTION
B. SHUTTER SECTION :-				
04	SHUTTER	04	01	40mm THICK BURMA BORDER TEAK WOOD SHUTTER

D1- 3'0"X7'0" 06 NO'S

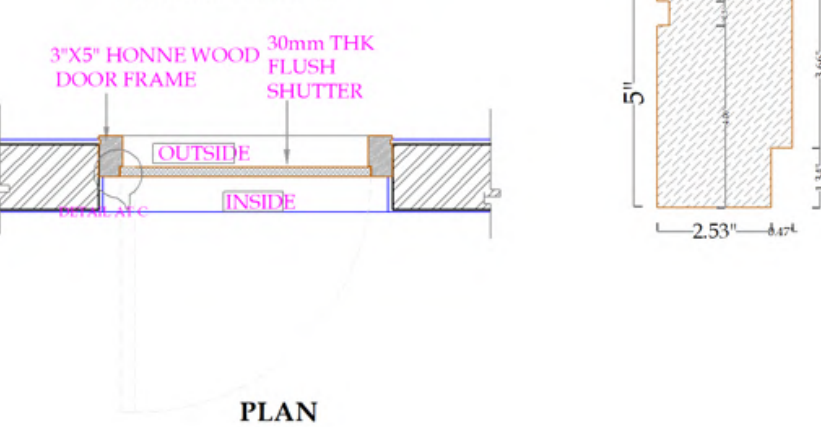

D1 - 3'0"X7'0" 06 NO'S

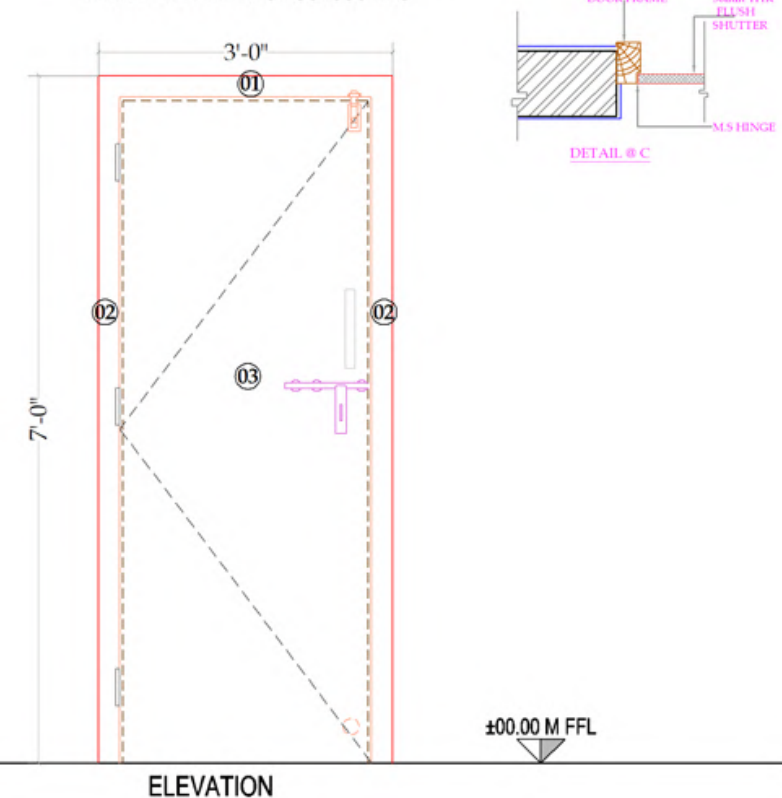

NO	DISCRPTION OF ITEM	REF	QTY	SPECIFICATIONS
A.FRAME SECTION :-				
01	TOP FRAME	01	01	3" X 5" HONNE WOOD FRAME SECTION
02	SIDE FRAME	02	02	3" X 5" HONNE WOOD FRAME SECTION
B. SHUTTER SECTION :-				
03	SHUTTER	03	01	30mm THICK FLUSH SHUTTER

Revised Schedule of Opening - SHILPA - 1449					
NAME	SIZE	SILL	DESCRIPTION	FLOOR	NO
MD	(4'6" X 7'0")	----	Main Door	1st+0'0"	01
D1	(3'0" X 7'0")	----	Bedroom Door	1st+0'0"	06
D1A	(3'0" X 7'0")	----	Terrace & Utility Door	1st+0'0"	02
D2	(2'6" X 7'0")	----	Toilet Door	1st+0'0"	04
PD	(4'6" X 7'0")	----	Pooja Door	1st+0'0"	01
PD	(4'6" X 7'0")	----	French Door	1st+0'0"	01
SD2	(3'0" X 7'0")	----	Sliding Door	1st+0'0"	04
PD1	(6'0" X 7'0")	----	French Door	1st+0'0"	02
21					
W	(8'0" X 5'0")	2'-0"	Window	0st+0'0"	01
W1	(6'0" X 5'0")	2'-0"	Window	2nd+0'0"	02
W2	(4'6" X 5'0")	2'-0"	Window	1st+0'0"	02
W2A	(3'6" X 5'0")	2'-0"	Window	2nd+0'0"	02
W3	(3'0" X 5'0")	2'-0"	Window	2nd+0'0"	05
W4	(2'6" X 5'0")	2'-0"	Window	1st+0'0"	01
W5	(1'6" X 5'0")	2'-0"	Window	1st+0'0"	01
SW	(3'6" X 4'0")	3'-0"	Window	1st+0'0"	03
KW	(3'0" X 2'0")	3'-0"	KITCHEN WINDOW	2nd+0'0"	02
KW1	(4'0" X 4'0")	3'-0"	KITCHEN WINDOW	1st+0'0"	01
V1	(3'0" X 2'0")	5'-0"	VENTILATOR	0st+0'0"	03
V	(1'6" X 2'0")	5'-0"	VENTILATOR	1st+0'0"	01
FG	(4'3" X 3'0")	2'-0"	FIXED GLASS	1st+0'0"	02
26					



CONSULTANT:

buildAhome
ScenicBeauty Homes Pvt Ltd.
Address: Fourth Floor, CRN Chambers, 13, Kasturba Rd, Shanthala Nagar, Ashok Nagar, Bengaluru, Karnataka 560001
Ph.no: +91 7090 0056 00, +91 80 2351 1033
www.buildahome.in

DRAWING NO: BAH/1449/ MISS.SHILPA/2025/ ARCH/WD003/01
SHEET NO : 001
SCALE : NOT TO SCALE
DESIGNED : Ar.SORNA
CHECKED : Ar.VIKAS RAO
DRAWN : KEERTHISH G
DATE : 14-05-2026
ARCHITECTURAL DRAWING

NOTE :
THIS DRAWING IS THE EXCLUSIVE PROPERTY OF "BUILDHOME" AND THE REPRODUCTION OF ANY PART WITHOUT PRIOR WRITTEN CONSENT FROM THIS OFFICE IS A VIOLATION OF APPLICABLE LAWS.


PD - 4'6"X7'0" 01 NO'S

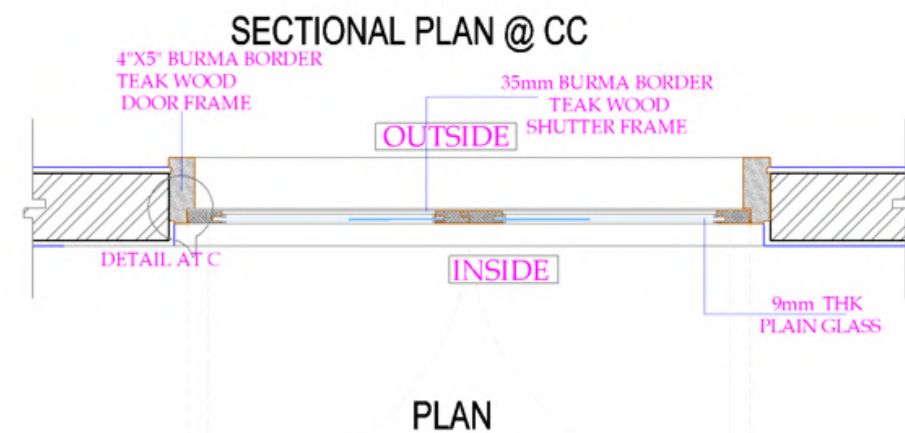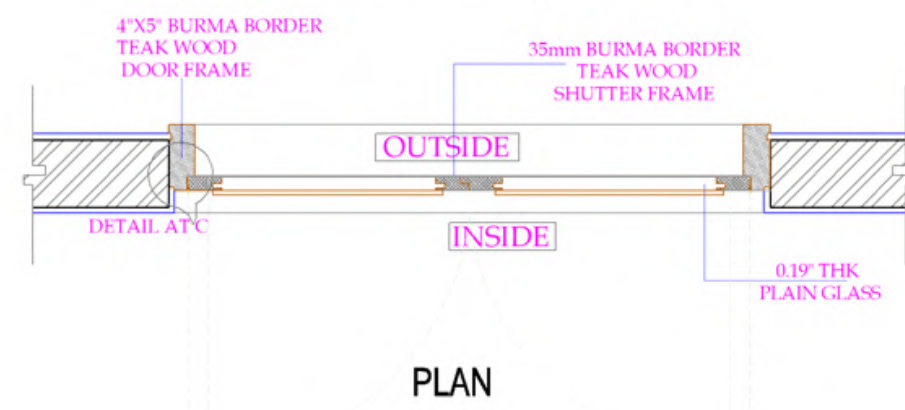


PD - 4'6" X 7'0" - 01 NO'S

BURMA BORDER TEAK WOOD WITH BRASS COATED S S ACCESSORIES

NO	DISCRPTION OF ITEM	REF	QTY	SPECIFICATIONS
A.FRAME SECTION :-				
01	TOP FRAME	01	01	4" X 5" BURMA BORDER TEAK WOOD FRAME SECTION
02	SIDE FRAME	02	02	4" X 5" BURMA BORDER TEAK WOOD FRAME SECTION
03	BOTTOM FRAME	03	01	4" X 5" BURMA BORDER TEAK WOOD FRAME SECTION
B. SHUTTER SECTION :-				
04	TOP RAIL	04	02	1.5" BURMA BORDER TEAK WOOD FRAME SHUTTER
05	BOTTOM RAIL	05	02	1.5" BURMA BORDER TEAK WOOD FRAME SHUTTER
06	SIDE RAIL	06	02	1.5" BURMA BORDER TEAK WOOD FRAME SHUTTER
07	INTERLOCKING RAIL (VERTICAL)	07	02	1.5" BURMA BORDER TEAK WOOD FRAME SHUTTER
08	WOOD PANEL	08	02	0.39" X 0.39" BURMA BORDER TEAK WOOD / BRONZE COATED M.S.RODS
09	GLASS PANEL	09	02	9 MM THK PLAIN GLASS

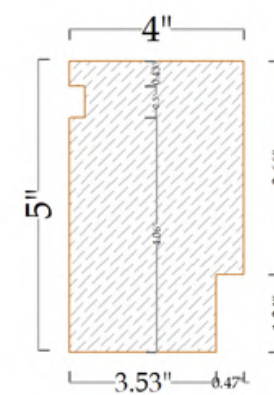

DETAIL @ C

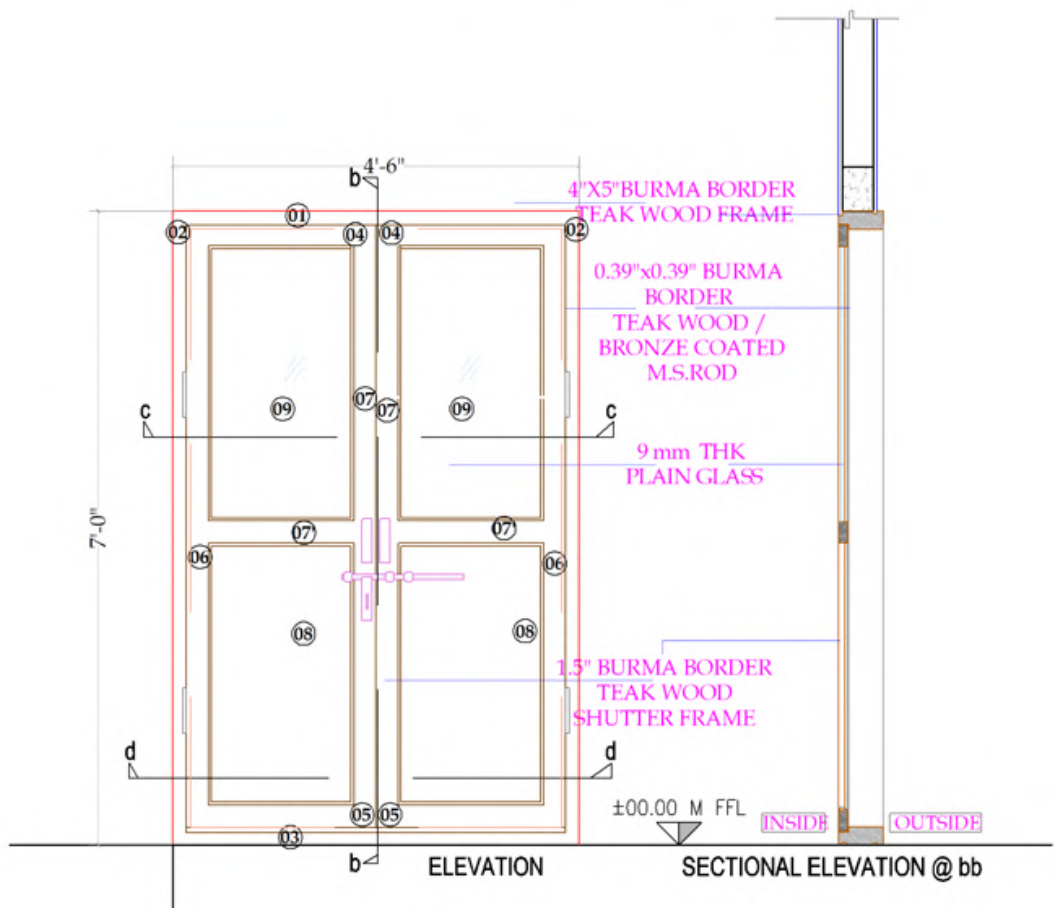

Revised Schedule - DOOR DETAILS					
NAME	SIZE	SILL	DESCRIPTION	FLOOR	NO
MD	(4'6" X 7'0")	----	Main Door	1st+0'0"	01
D1	(3'0" X 7'0")	----	Bedroom Door	1st+0'0"	06
D1A	(3'0" X 7'0")	----	Terrace & Utility Door	1st+0'0"	02
D2	(2'6" X 7'0")	----	Toilet Door	1st+0'0"	04
PD	(4'6" X 7'0")	----	Pooja Door	1st+0'0"	01
PD	(4'6" X 7'0")	----	French Door	1st+0'0"	01
SD2	(3'0" X 7'0")	----	Sliding Door	1st+0'0"	04
PD1	(6'0" X 7'0")	----	French Door	1st+0'0"	02
21					
W	(8'0" X 5'0")	2'-0"	Window	0st+0'0"	01
W1	(6'0" X 5'0")	2'-0"	Window	2nd+0'0"	02
W2	(4'6" X 5'0")	2'-0"	Window	1st+0'0"	02
W2A	(3'6" X 5'0")	2'-0"	Window	2nd+0'0"	02
W3	(3'0" X 5'0")	2'-0"	Window	2nd+0'0"	05
W4	(2'6" X 5'0")	2'-0"	Window	1st+0'0"	01
W5	(1'6" X 5'0")	2'-0"	Window	1st+0'0"	01
SW	(3'6" X 4'0")	3'-0"	Window	1st+0'0"	03
KW	(3'0" X 2'0")	3'-0"	KITCHEN WINDOW	2nd+0'0"	02
KW1	(4'0" X 4'0")	3'-0"	KITCHEN WINDOW	1st+0'0"	01
V1	(3'0" X 2'0")	5'-0"	VENTILATOR	0st+0'0"	03
V	(1'6" X 2'0")	5'-0"	VENTILATOR	1st+0'0"	01
FG	(4'3" X 3'0")	2'-0"	FIXED GLASS	1st+0'0"	02
26					

CONSULTANT:

buildAhome
ScenicBeauty Homes Pvt Ltd.
Address: Fourth Floor, CRN Chambers, 13, Kasturba Rd, Shanthala Nagar, Ashok Nagar, Bengaluru, Karnataka 560001
Ph.no: +91 7090 0056 00, +91 80 2351 1033
www.buildahome.in

DRAWING NO: BAH/1449/ MISS.SHILPA/2025/ ARCH/WD003/01
SHEET NO : 004
SCALE : NOT TO SCALE
DESIGNED : Ar.SORNA
CHECKED : Ar.VIKAS RAO
DRAWN : KEERTHISH G
DATE : 14-05-2026
ARCHITECTURAL DRAWING

NOTE :
THIS DRAWING IS THE EXCLUSIVE PROPERTY OF "BUILDHOME" AND THE REPRODUCTION OF ANY PART WITHOUT PRIOR WRITTEN CONSENT FROM THIS OFFICE IS A VIOLATION OF APPLICABLE LAWS.

EXTERNAL PAINT CODE - 966



966 - INTERNAL PAINT CODE

966 - INTERNAL PAINT CODE


PAINT CODES

- OPTION 1


1.  COOL WATER 8407

2.  IVORY PALACE 0954
- OPTION 2

 OPALINE GREEN 2463

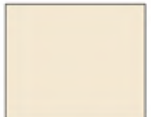 PALE IVORY 7892

GROUND FLOOR - all internal walls

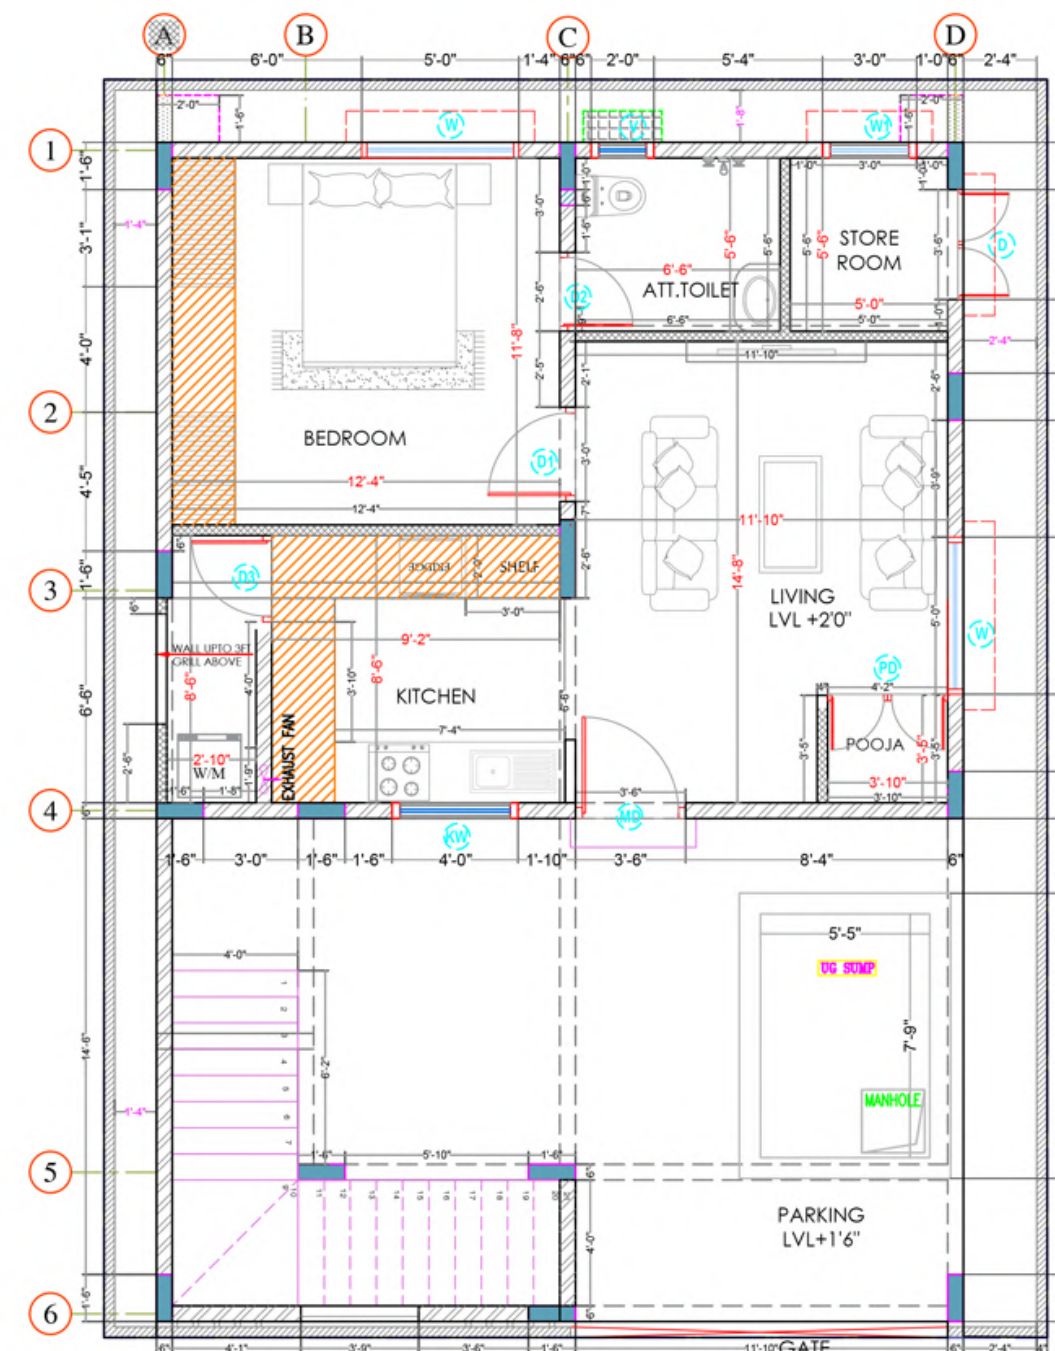

OPTION 1



CREAM PIE (L152)

OPTION 2




PRISTINE LINEN (L153)

OPTION 3



WHITE BUTTER (L164)

FIRST FLOOR

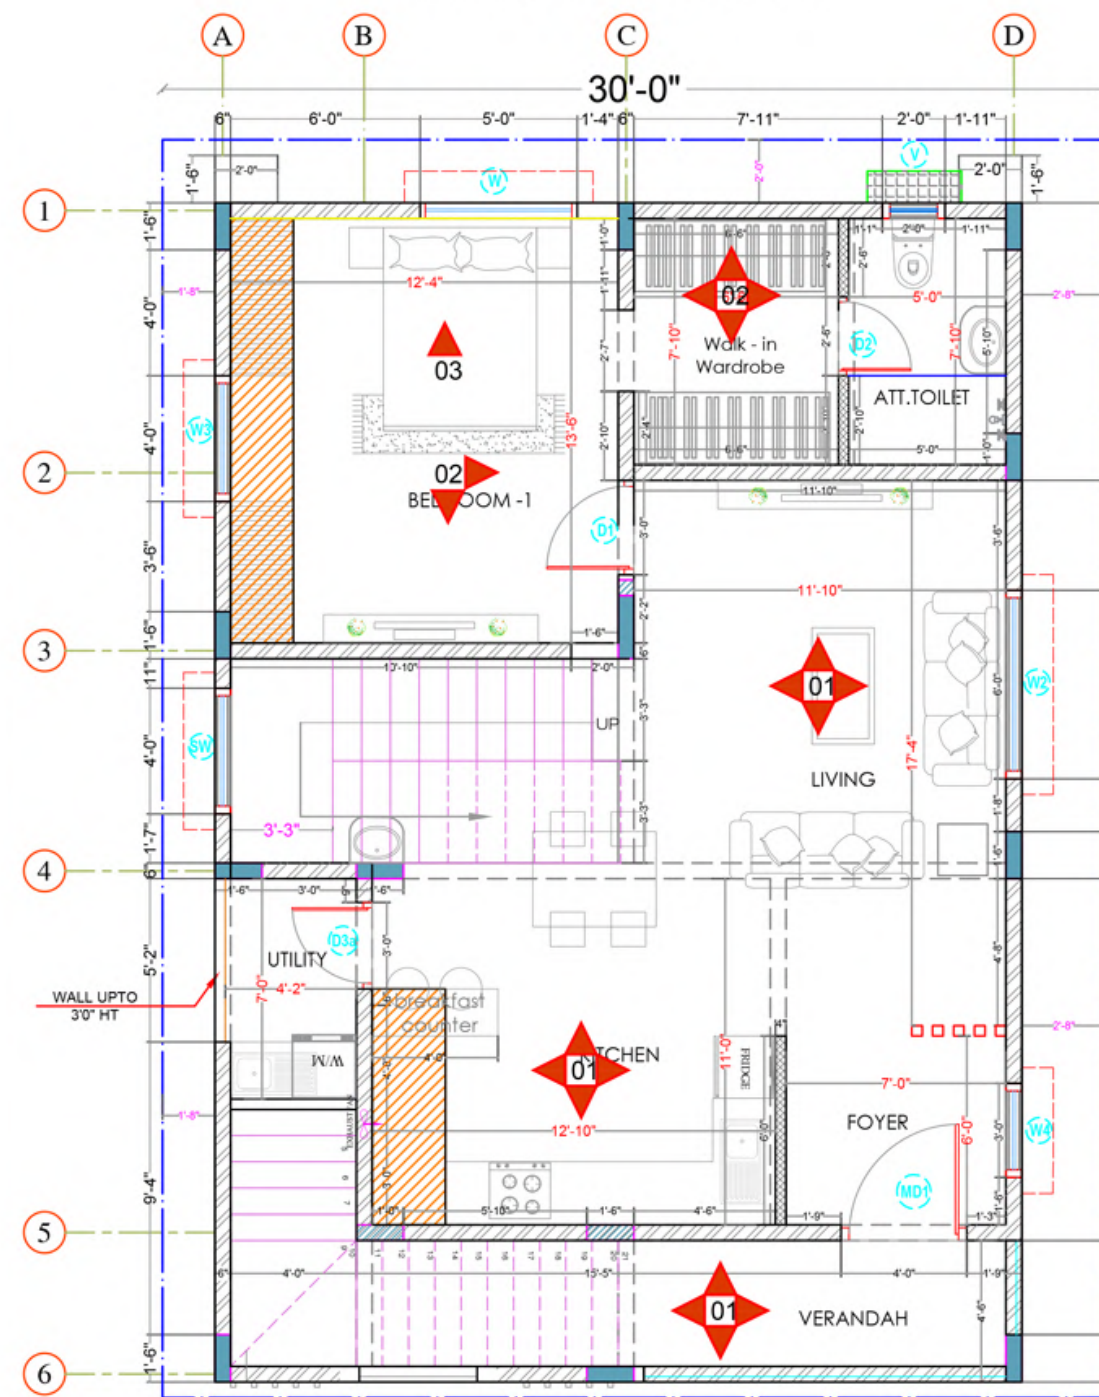

OPTION 1



MORNING GLORY (0765)

OPTION 2



PEARL STAR (L103)

OPTION 1



LOVE SONG (L144)

OPTION 2



GLACIER RIDGE (8428)

PARENTS BEDROOM HIGHLIGHTER




HONEY MUSTARD (7880)

OPTION 2



NATURAL TINGE (7879)

SECOND FLOOR

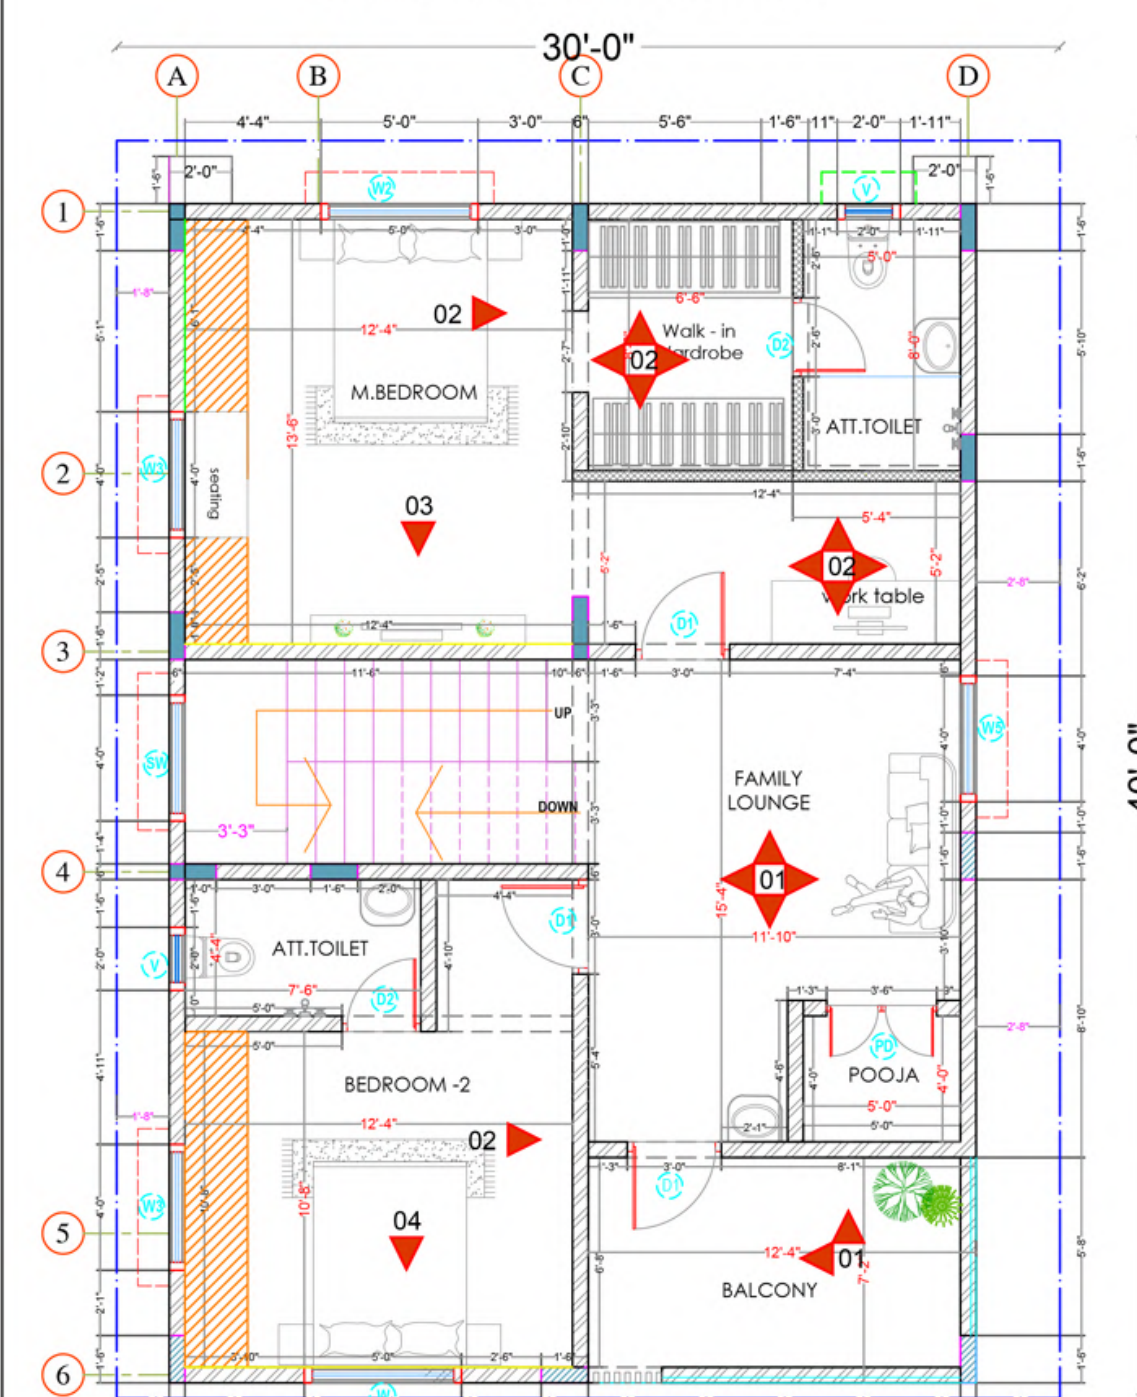

OPTION 1



MORNING GLORY (0765)

OPTION 2



PEARL STAR (L103)


MASTER BEDROOM HIGHLIGHTER



DESERT BEIGE (8465)

TWINKLING STAR (8466)

BOTH BEDROOM LIGHTER

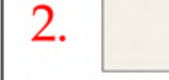

LOVE SONG (L144)


KIDS BEDROOM HIGHLIGHTER



GRACEFUL PINK (8115)

SUGARED PEACH (8032)

THIRD FLOOR - all internal walls

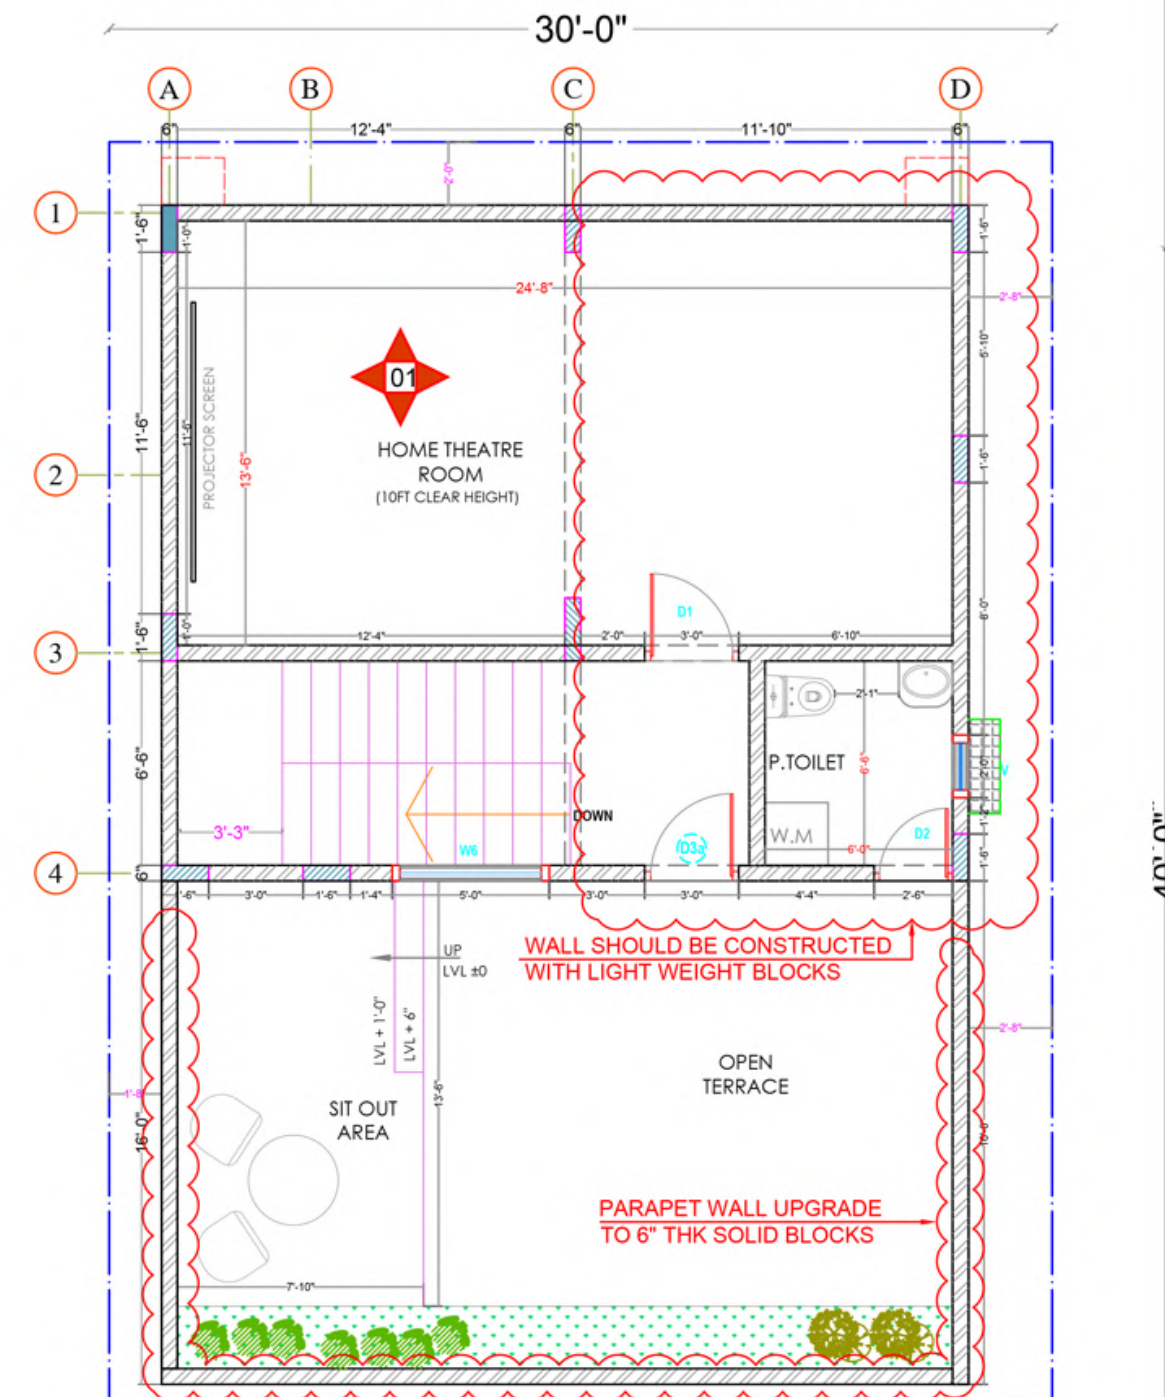


OPTION 1




MORNING GLORY (0765)

OPTION 2

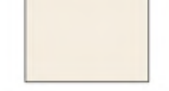


PEARL STAR (L103)


ALL THE PAINT CODES ARE ACCORDING TO ASIAN PAINTS
NOTE : PLEASE DO PATCH TEST ON SITE BEFORE PROCEEDING AND
TAKE CONFIRMATION FROM THE CLIENT AND ARCHITECT FOR THE SAME.

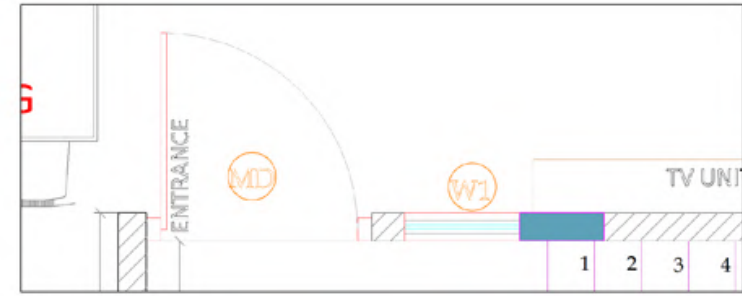


PLAN

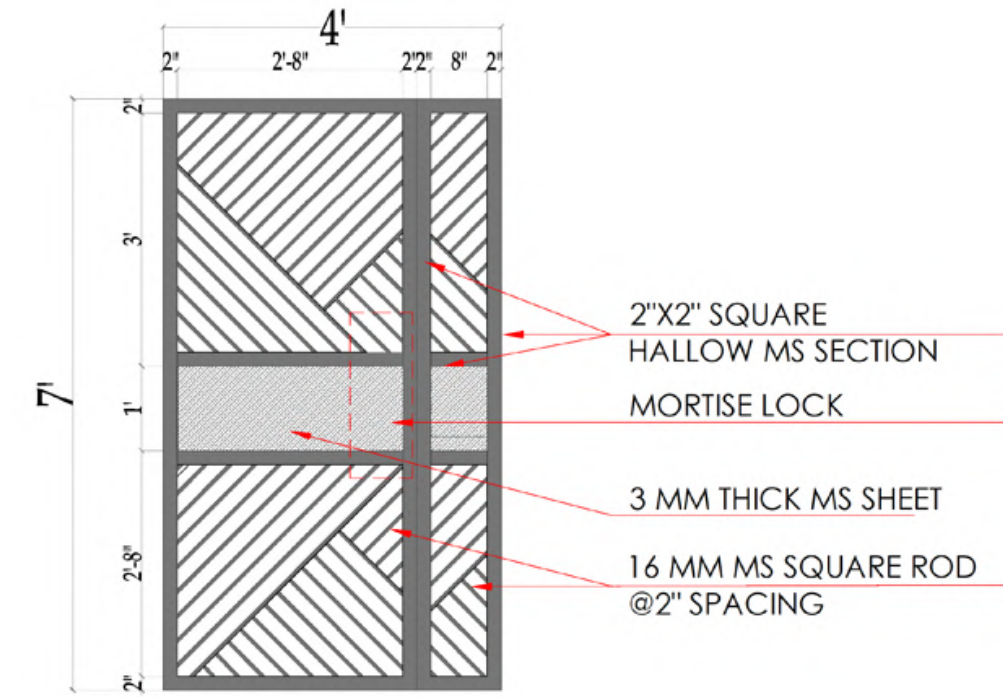


DOOR ELEVATION

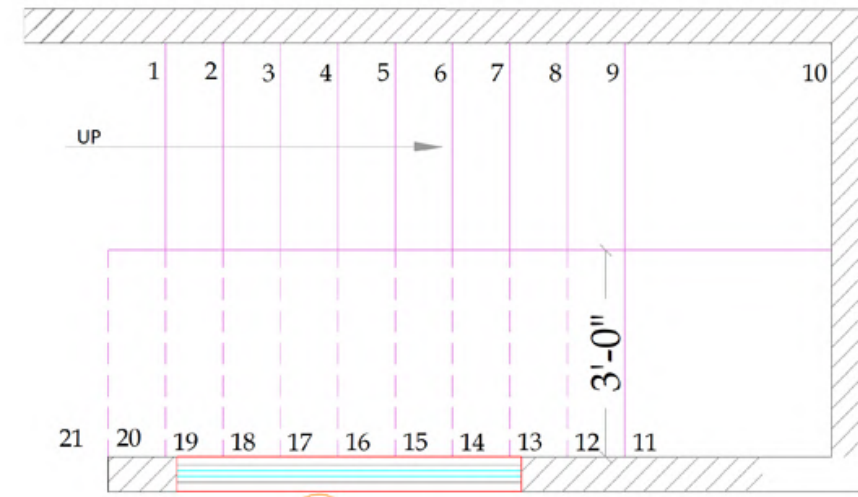


PLAN

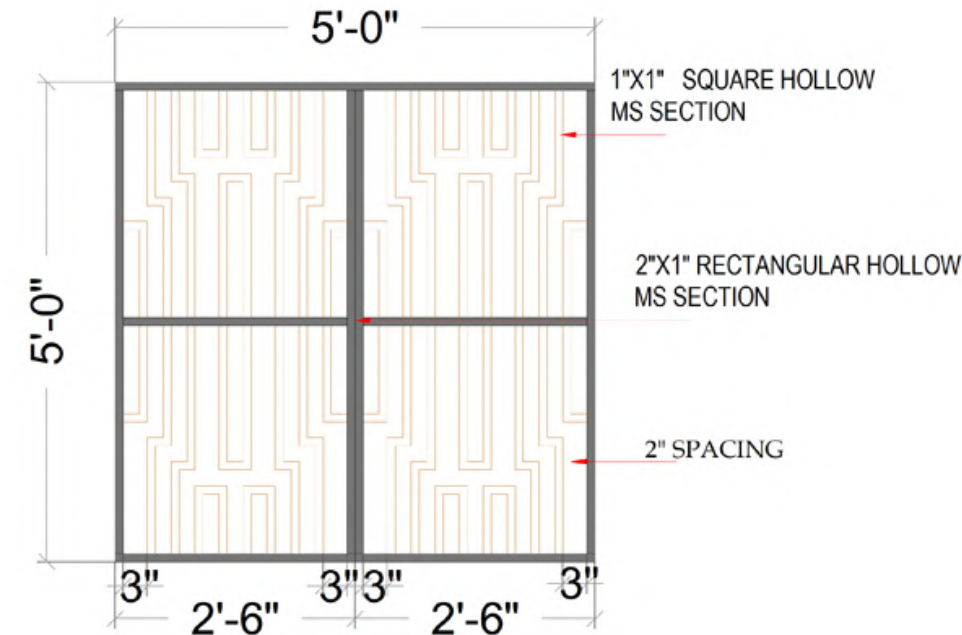


ELEVATION - 2 NOS

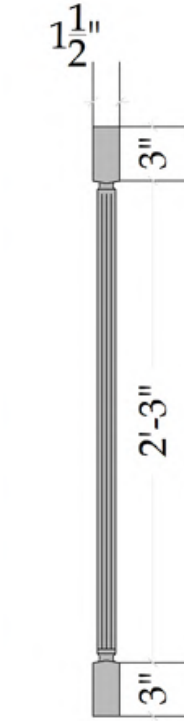



DETAIL-A

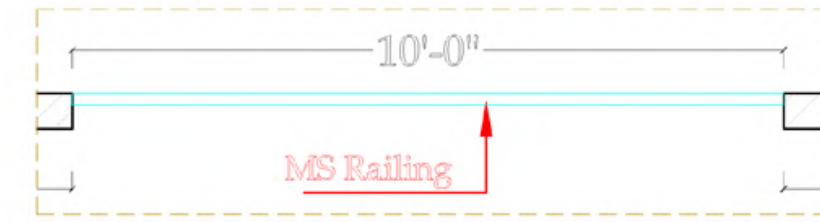

PLAN

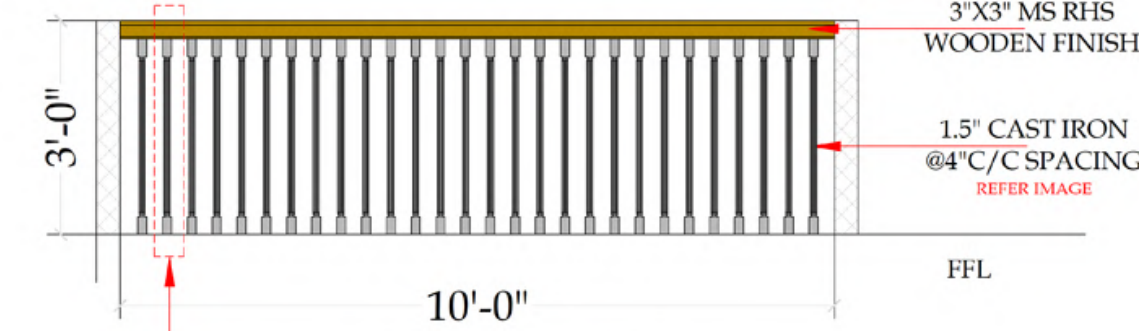

FRONT VIEW

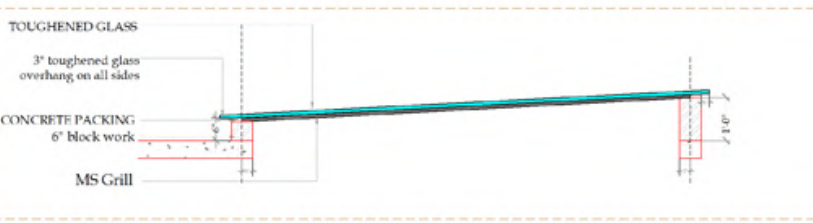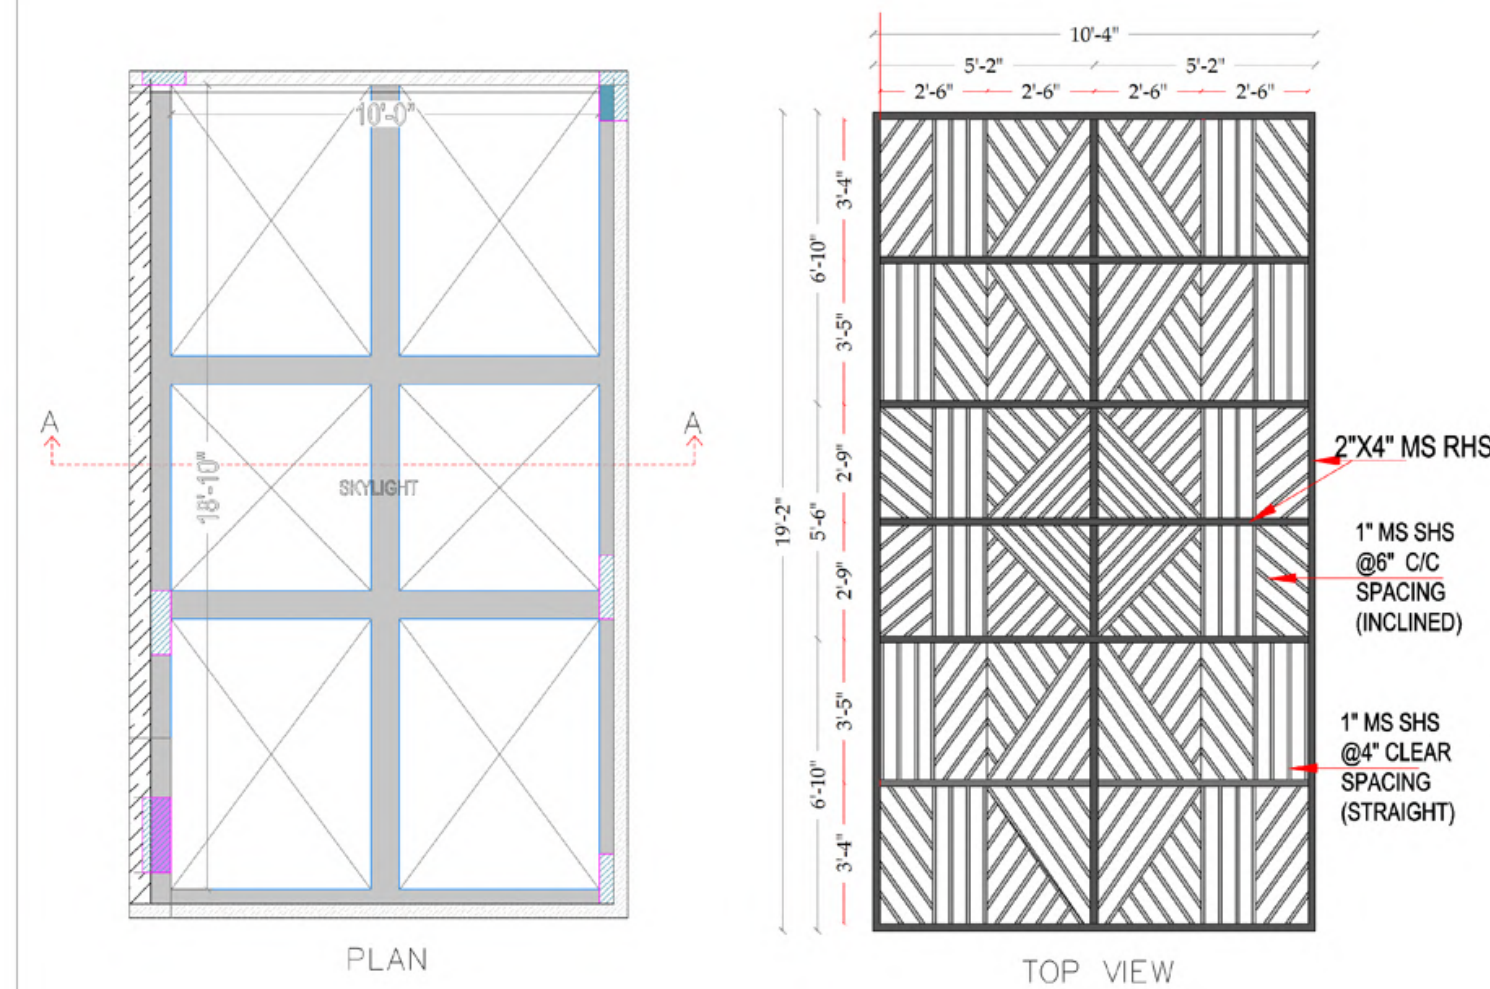

SECTION - A

CLIENT NAME : Mr.RAGHUNATH - 1101

DRAWING NAME : FIRST FLOOR ENTRANCE SAFETY DOOR DETAILS

buildAhome

A ViRgo Group Company

Scenic Beauty Homes Pvt Ltd.

Address : 552, 7th Main Road, AGS Layout,
Dollars Colony, R.M.V. 2nd Stage,
Bengaluru, Karnataka 560094

Ph no : +91-7090 0056 00 , +91-80-2351 1033
www.buildahome.in

DRAWING NO:
BAH/1101/RAGHUNATH/2024/ARCH/WD006

SHEET NO : 001

SCALE : NOT TO SCALE

CHECKED : Ar. RANJAN

DESIGN : Ar. BASWARAJ

DRAWN : KEERTHISH G

DATE : 08-05-2026

ARCHITECTURAL DRAWING

NOTE :
THIS DRAWING IS THE EXCLUSIVE PROPERTY OF
"BUILD-AHOME" AND THE REPRODUCTION OF ANY PART WITHOUT PRIOR
WRITTEN CONSENT FROM THIS OFFICE IS A VIOLATION OF APPLICABLE LAWS.

E

N

S

W

CLIENT NAME : Mr.RAGHUNATH - 1101

DRAWING NAME : WEST STAIRCASE GRILL DETAILS

buildAhome

A ViRgo Group Company

Scenic Beauty Homes Pvt Ltd.

Address : 552, 7th Main Road, AGS Layout,
Dollars Colony, R.M.V. 2nd Stage,
Bengaluru, Karnataka 560094

Ph no : +91-7090 0056 00 , +91-80-2351 1033
www.buildahome.in

DRAWING NO:
BAH/1101/RAGHUNATH/2024/ARCH/WD006

SHEET NO : 002

SCALE : NOT TO SCALE

CHECKED : Ar. RANJAN

DESIGN : Ar. BASWARAJ

DRAWN : KEERTHISH G

DATE : 08-05-2026

ARCHITECTURAL DRAWING

NOTE :
THIS DRAWING IS THE EXCLUSIVE PROPERTY OF
"BUILD-AHOME" AND THE REPRODUCTION OF ANY PART WITHOUT PRIOR
WRITTEN CONSENT FROM THIS OFFICE IS A VIOLATION OF APPLICABLE LAWS.

E

N

S

W

CLIENT NAME : MR.VENKATARAMANA & FAMILY - 1170

DRAWING NAME : FIRST FLOOR OPEN TERRACE RAILING DETAILS

buildAhome

A ViRgo Group Company

Scenic Beauty Homes Pvt Ltd.

Address : 552, 7th Main Road, AGS Layout,
Dollars Colony, R.M.V. 2nd Stage, Bengaluru,
Karnataka 560094.

Ph no : +91-7090 0056 00 , +91-80-2351 1033
www.buildahome.in

DRAWING NO:
BAH/1170/VENKATARAMANA/2025/ARCH/WD006

SHEET NO : 001

SCALE : NOT TO SCALE

CHECKED : Ar. JAYDEEP

DESIGN : Ar. JAYDEEP

DRAWN : KEERTHISH G

DATE : 12-05-2026

ARCHITECTURAL DRAWING

NOTE :
THIS DRAWING IS THE EXCLUSIVE PROPERTY OF
"BUILD-AHOME" AND THE REPRODUCTION OF ANY PART WITHOUT PRIOR
WRITTEN CONSENT FROM THIS OFFICE IS A VIOLATION OF APPLICABLE LAWS.

E

N

S

W

CLIENT NAME : Mr.DINAKAR - 1111

DRAWING NAME : LIVING SKYLIGHT DETAILS

buildAhome

A ViRgo Group Company

Scenic Beauty Homes Pvt Ltd.

Address : 552, 7th Main Road, AGS Layout,
Dollars Colony, R.M.V. 2nd Stage, Bengaluru,
Karnataka 560094.

Ph no : +91-7090 0056 00 , +91-80-2351 1033
www.buildahome.in

DRAWING NO:
BAH/2024/1111/WD006

SHEET NO : 001

SCALE : NOT TO SCALE

CHECKED : BASAWARAJ

DESIGN : BASAWARAJ

DRAWN : KEERTHISH G

DATE : 18-05-2026

ARCHITECTURAL DRAWING

NOTE :
THIS DRAWING IS THE EXCLUSIVE PROPERTY OF
"BUILD-AHOME" AND THE REPRODUCTION OF ANY PART WITHOUT PRIOR
WRITTEN CONSENT FROM THIS OFFICE IS A VIOLATION OF APPLICABLE LAWS.

E

N

S

W

41

42

1759 - CTR

3D RENDERS

Project : Traditional Mangalore Style Restaurant

Site Dimension : 30'-4" × 99'-9"

Plot Area : 3026 sq.ft

Primary Function : Fast dining, fine dining, VIP dining, banquet/dining halls and supporting kitchen/service facilities.

DESIGN INTENT :

To create a contemporary restaurant inspired by traditional Mangalore architecture, incorporating sloped tiled roofs, arched windows, timber elements and warm earthy materials. A central courtyard forms the heart of the design, creating visual connectivity and an immersive dining experience while maintaining efficient modern restaurant functions.



FRONT ELEVATION



MAIN DOOR ENTRY



VIEW OF COURTYARD



COURTYARD HIGHLIGHTER WALL



DINING AREA VIEW

ELEVATIONS

3D RENDERS

Project Type : Residential
Site Dimension : 30'-0" × 40'-0"








The residential elevation focuses on a modern and elegant architectural character, using clean forms, balanced proportions, and subtle material variations. Carefully placed windows, balconies, and projections add depth to the façade while providing natural light and functional outdoor spaces. Overall, the design aims to create a simple, contemporary, and welcoming home with a strong visual identity.




04 BUILDING MATERIALS & CONSTRUCTION TECHNOLOGY

Project Type : Wardrobe, Kitchen, False Ceiling
Semester : S7


This chapter includes the BMCT drawings done in the seventh semester. It contains plans, sections, elevations, and construction details that explain how different parts of a building are drawn and detailed. The drawings focus on understanding construction elements, materials, and basic detailing through clear and simple representation.

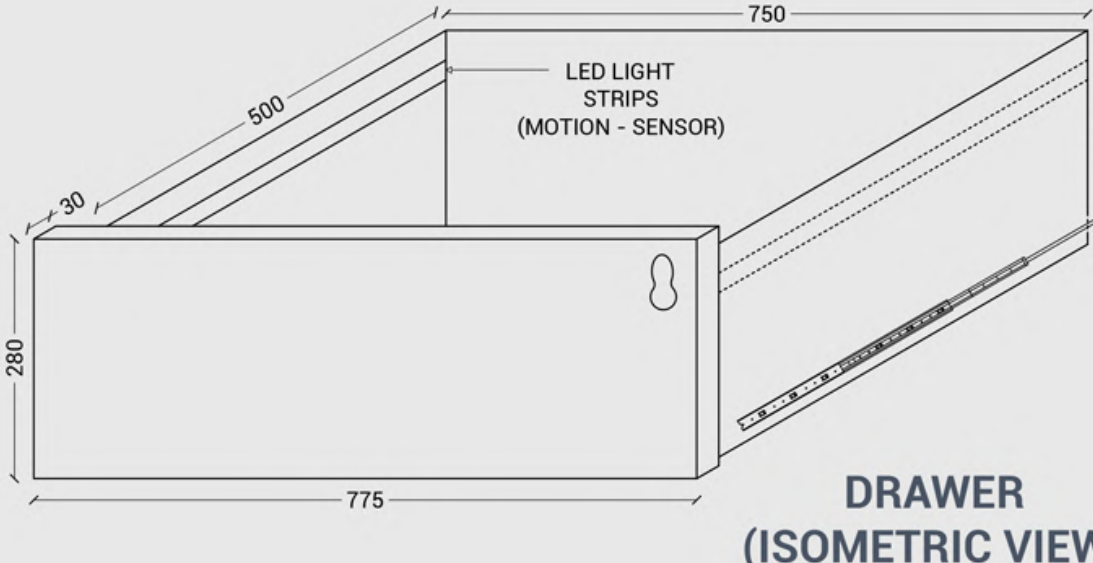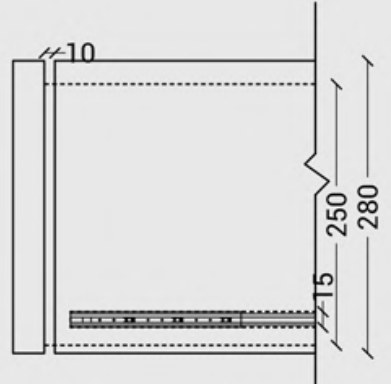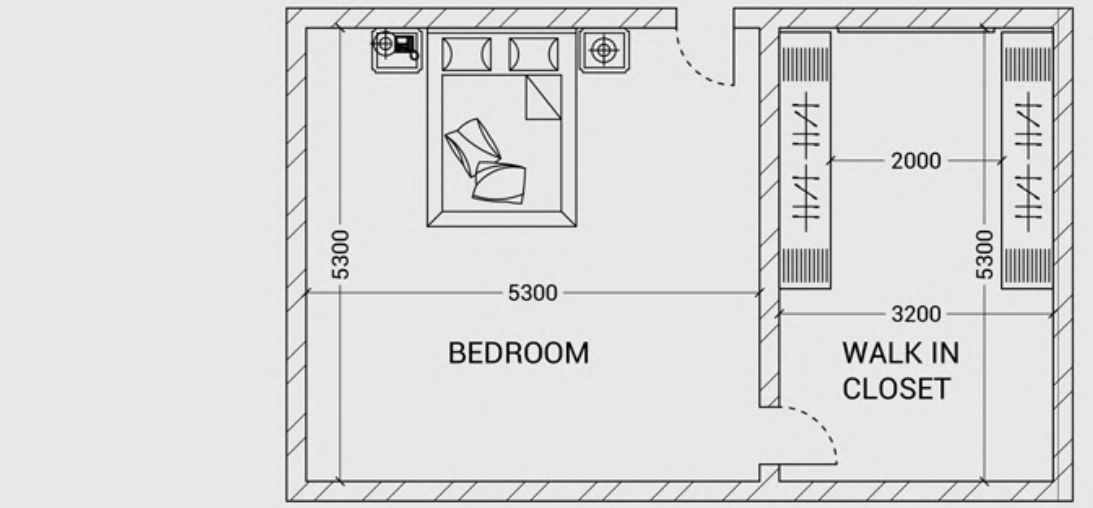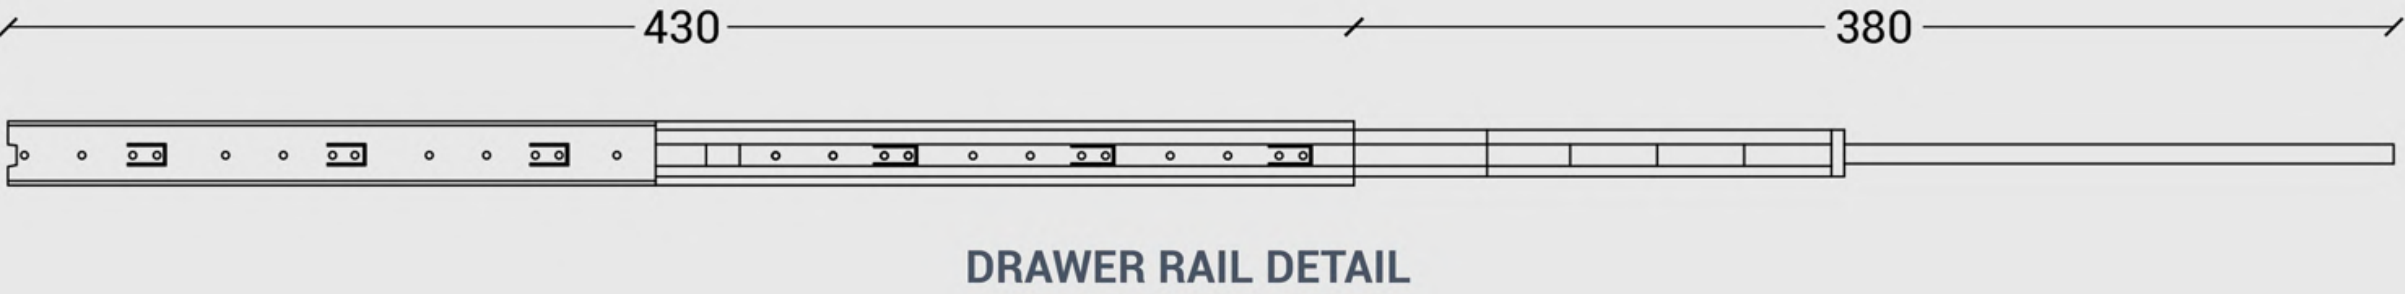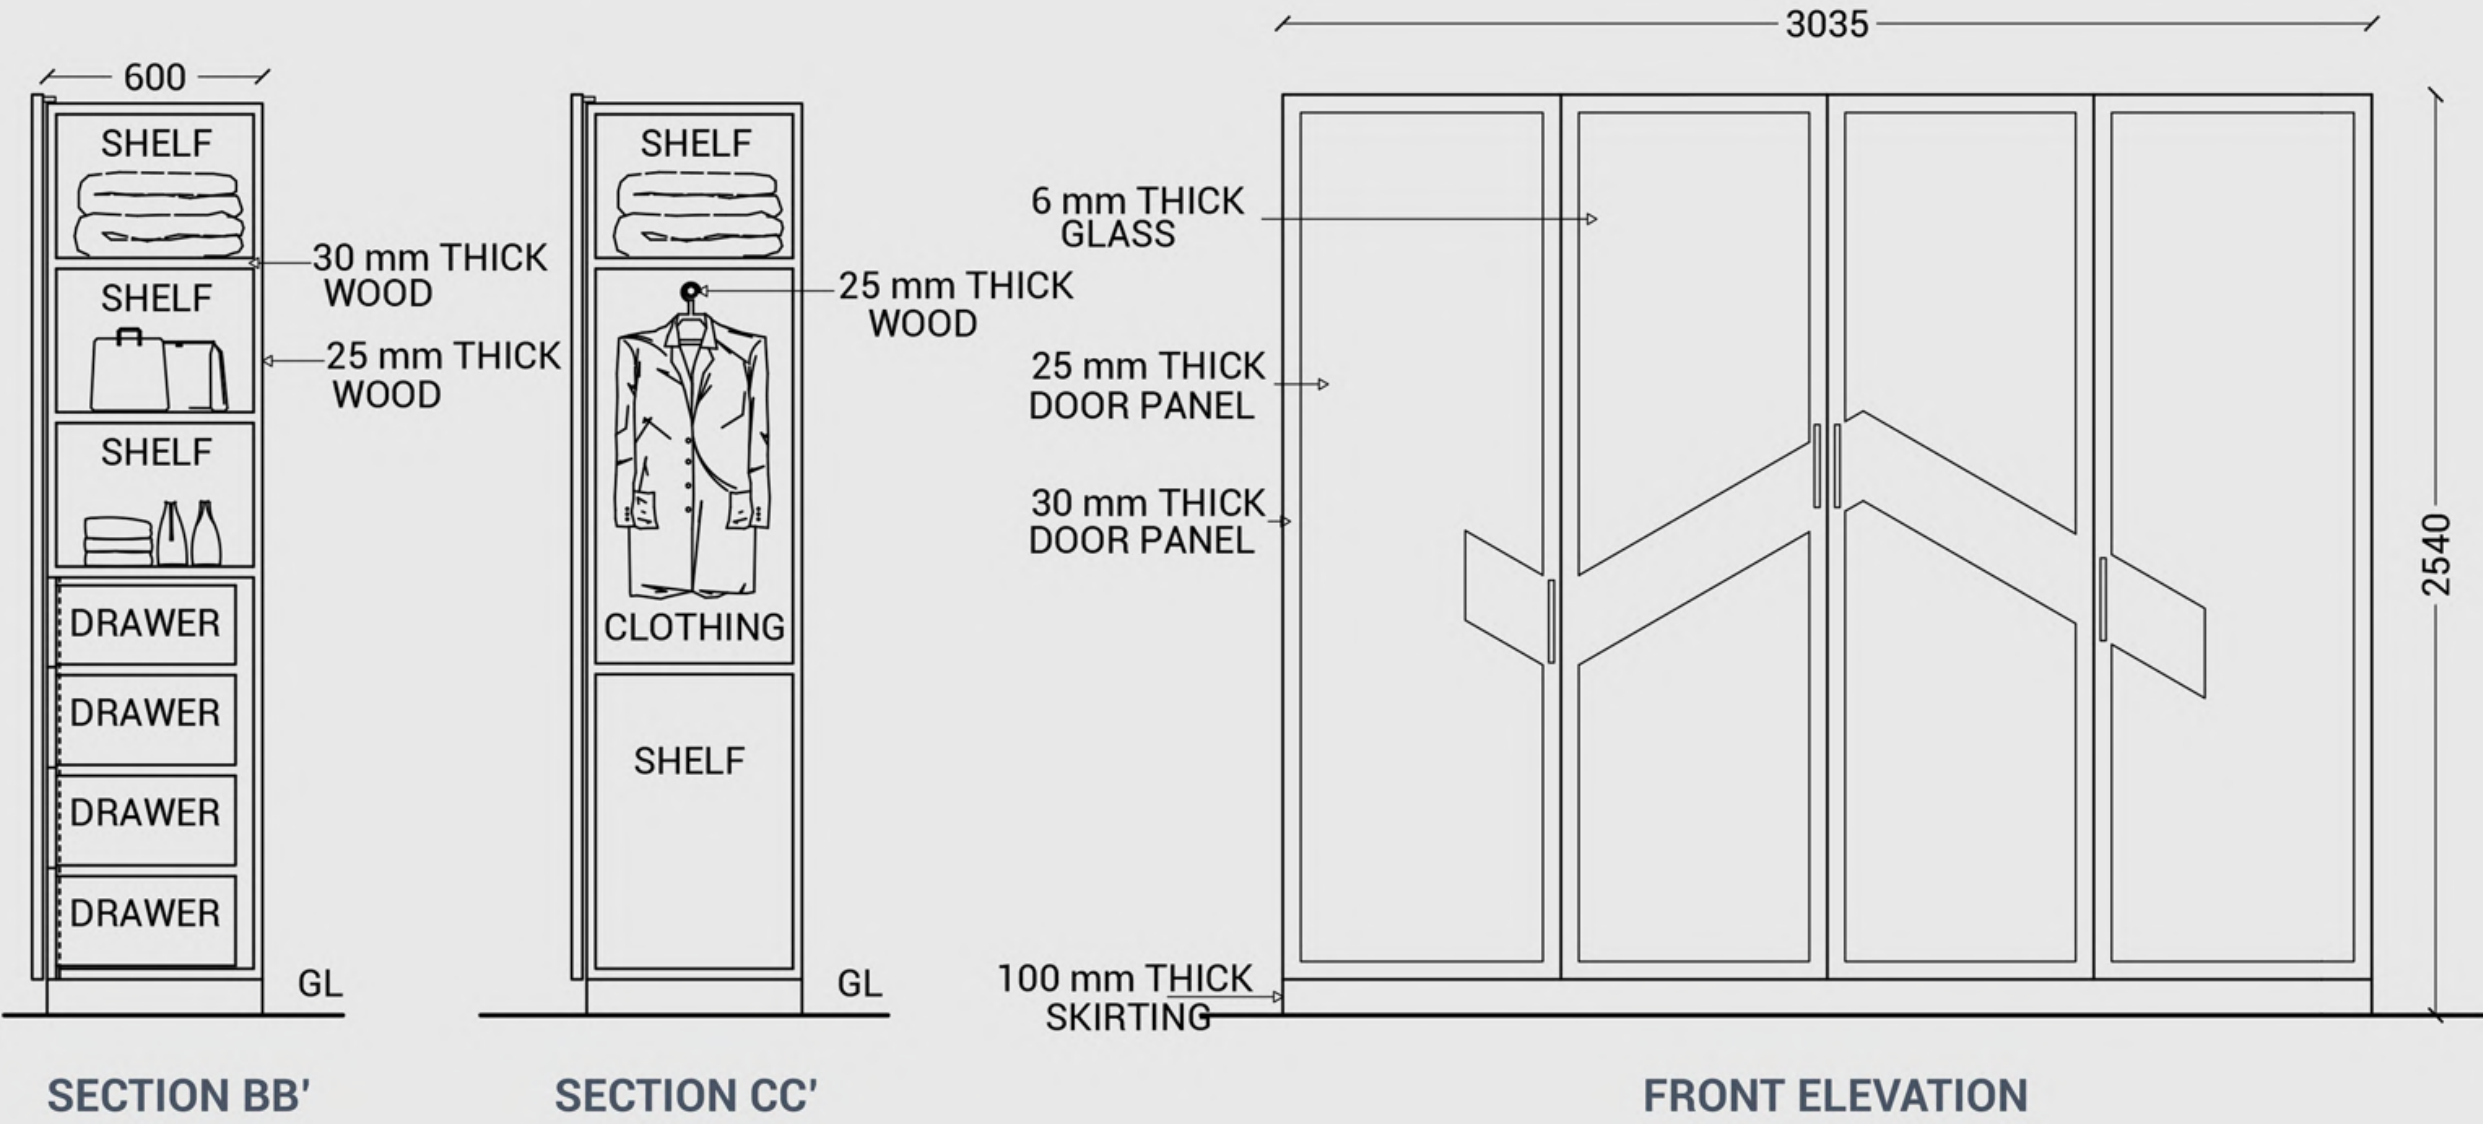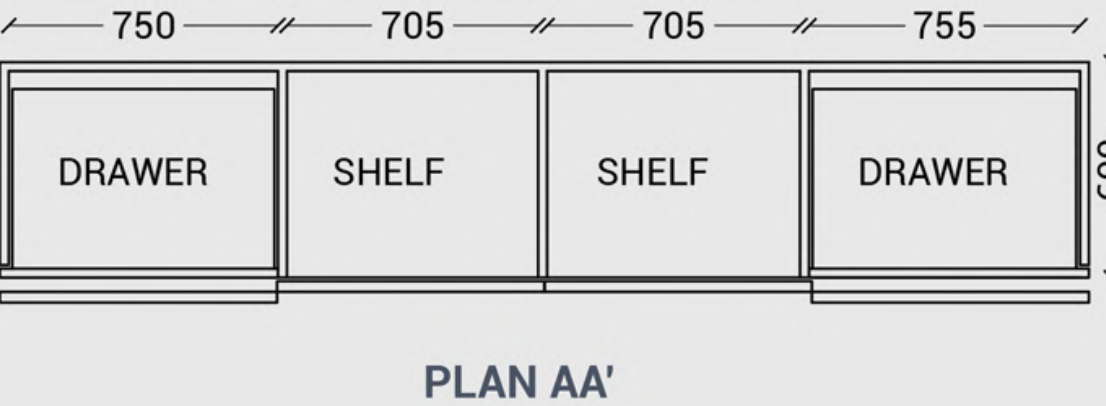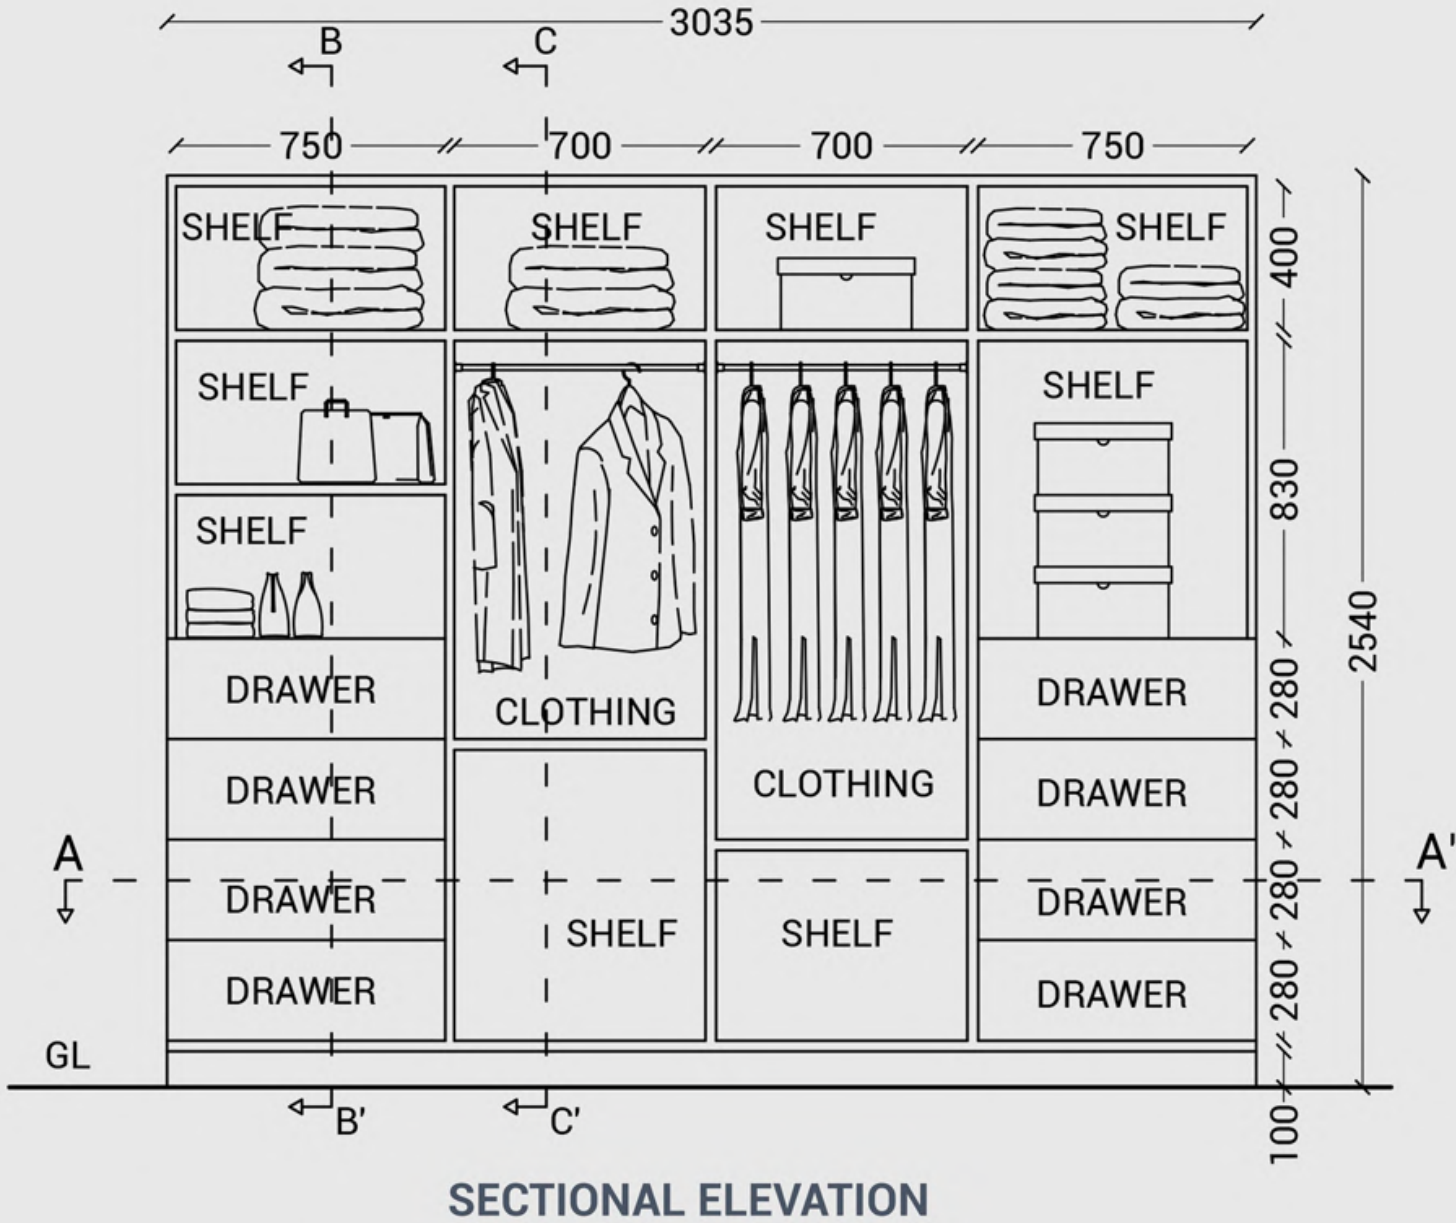


WALK-IN PARALLEL WARDROBE

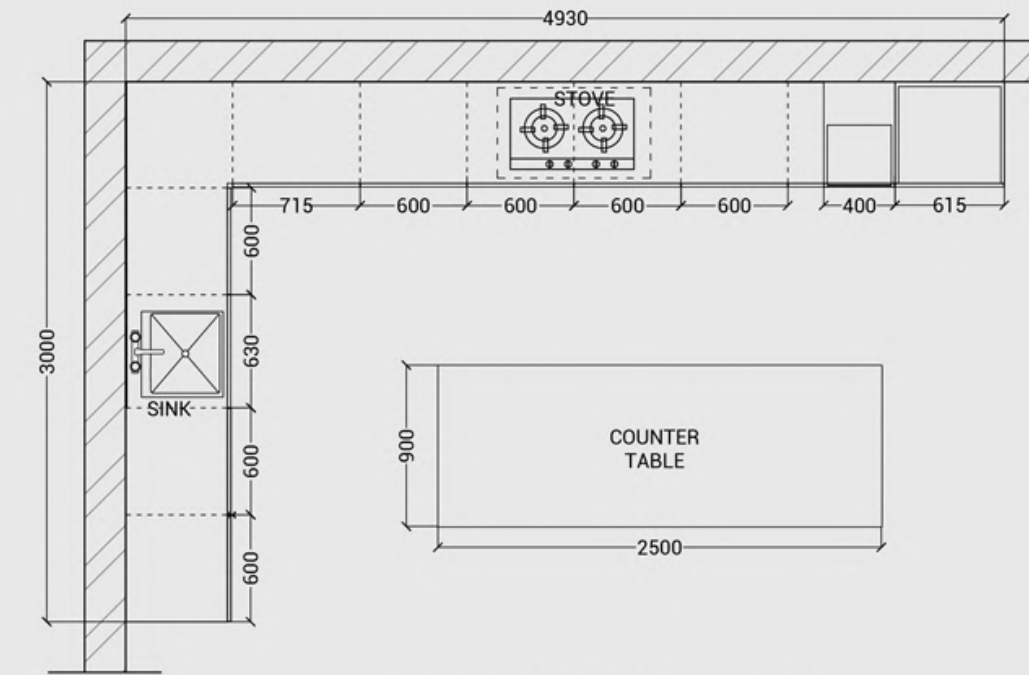


PLAN OVER COUNTER

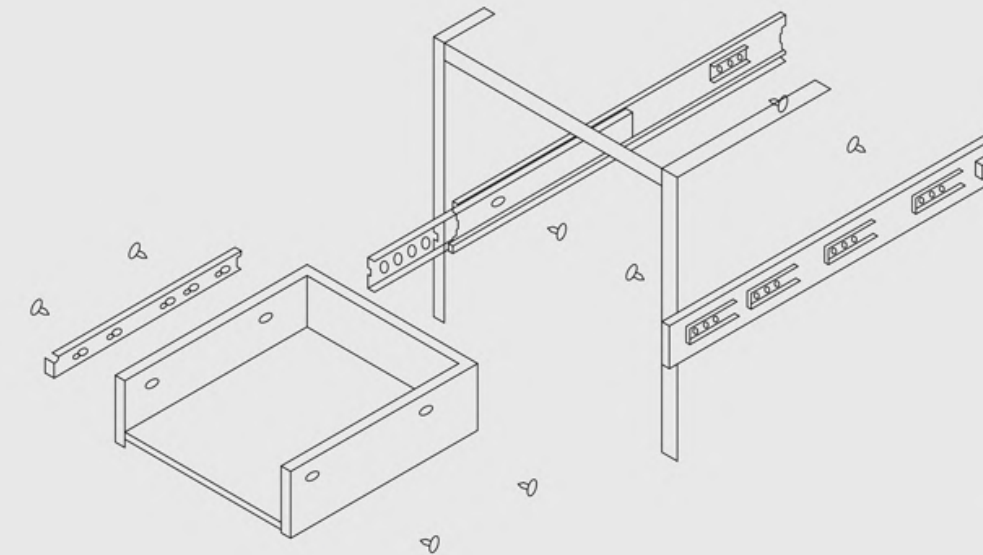


TELESCOPIC
DRAWER DETAIL

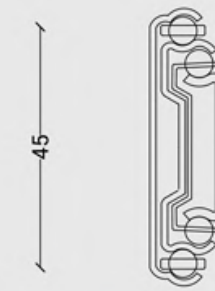


TELESCOPIC
RAIL DETAIL

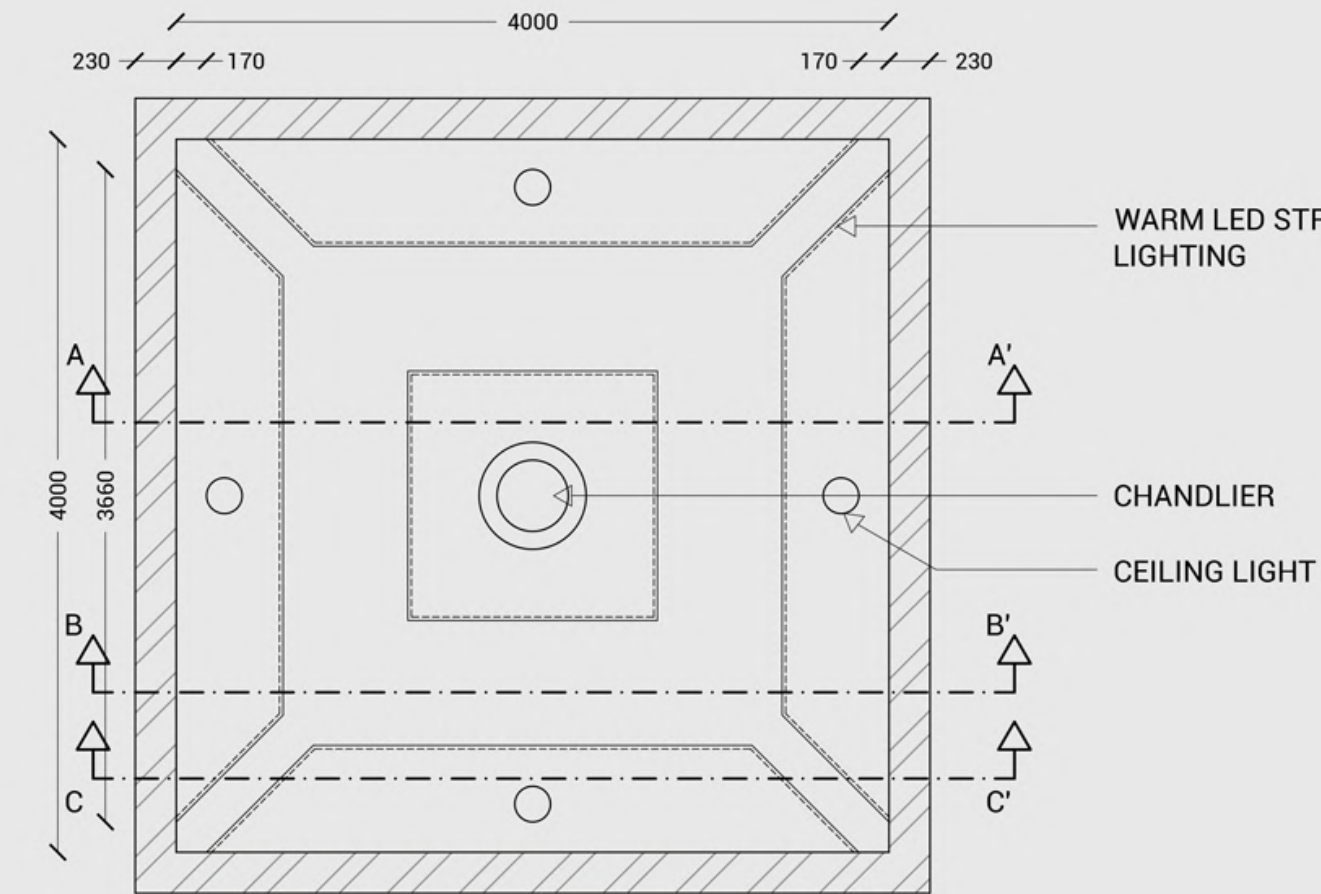


REFLECTED CEILING PLAN

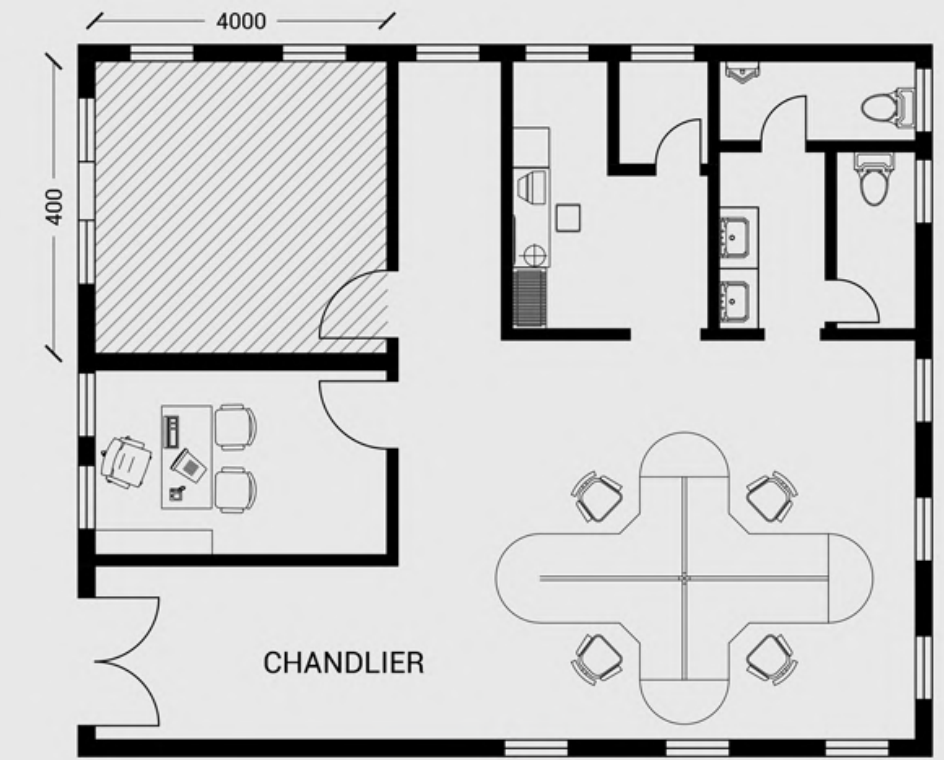



KEY PLAN

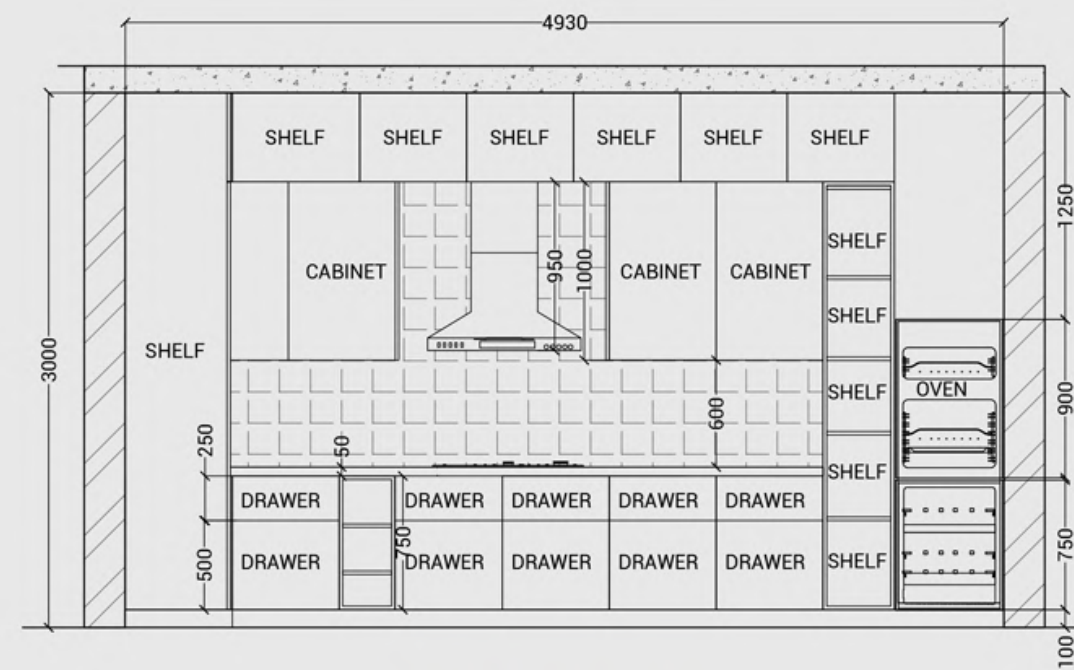


ELEVATION AA'

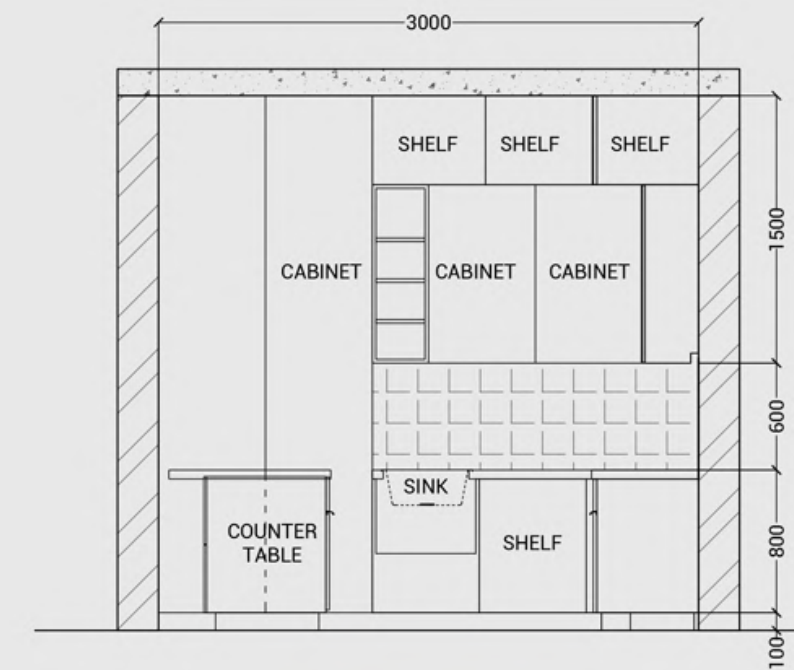


ELEVATION BB'

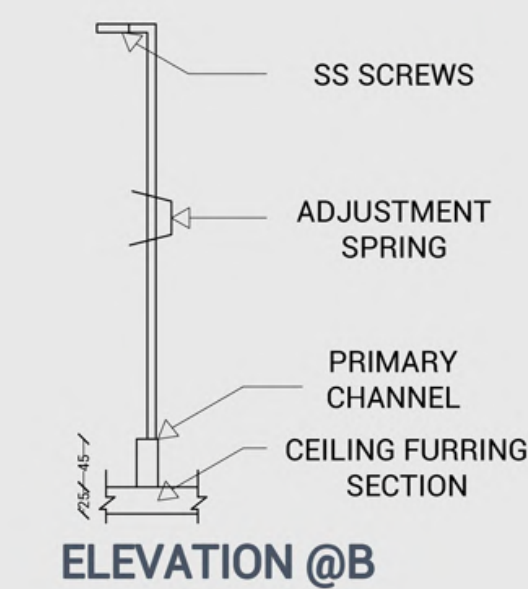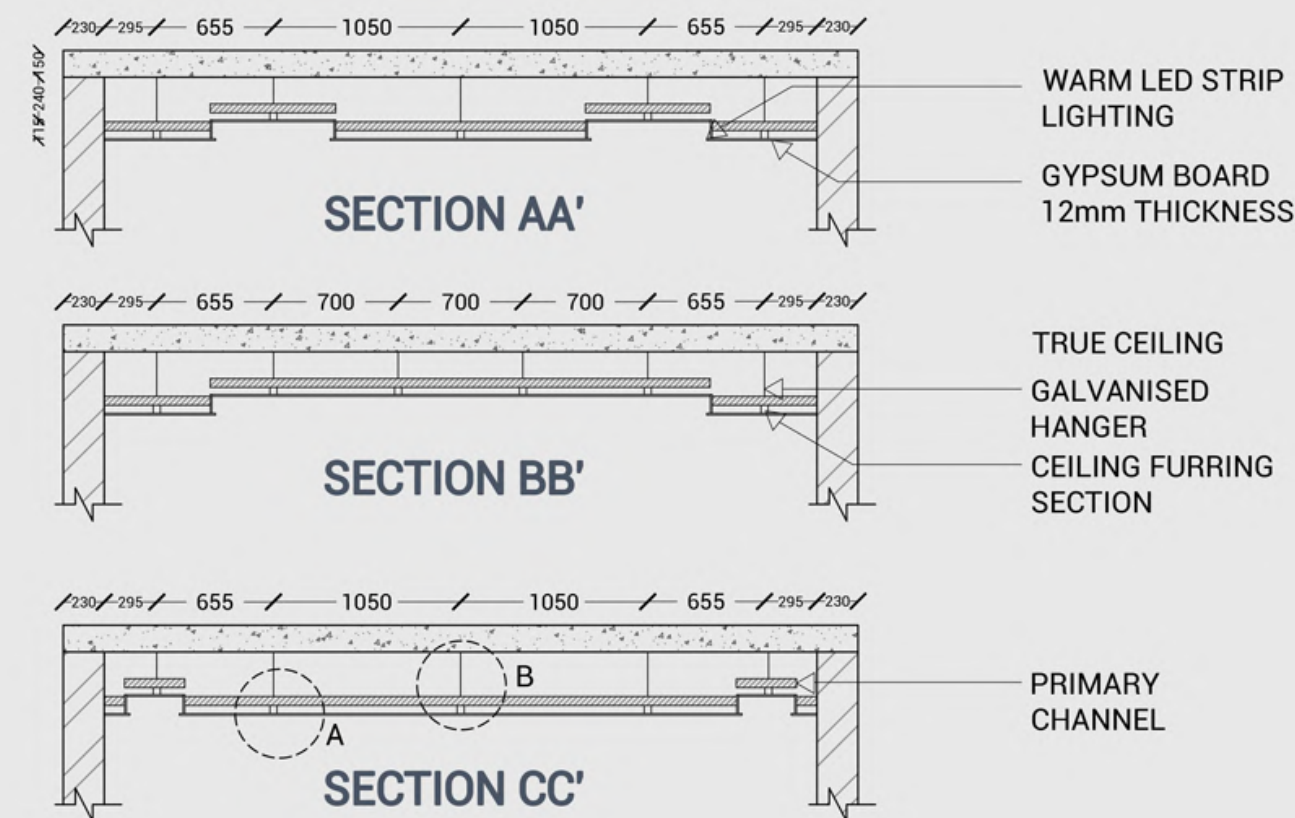


ELEVATION @B

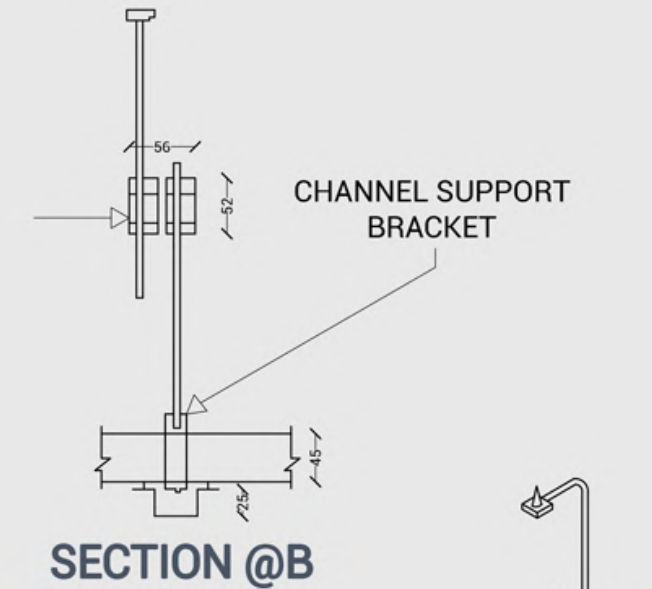

SECTION @B

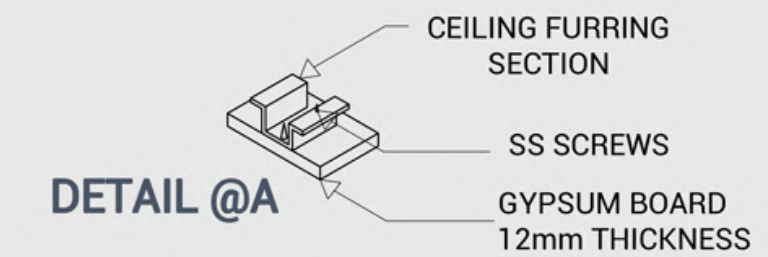

DETAIL @A

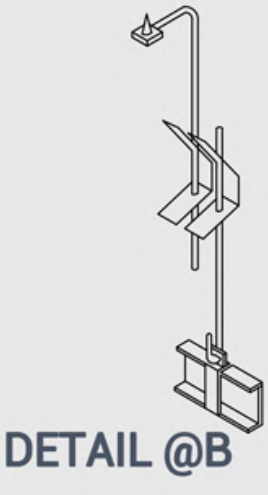

DETAIL @B

L-SHAPED KITCHEN

FALSE CEILING

05 MISCELLANEOUS

This chapter includes photography, physical model making, site visits and many more creative and exploratory works developed alongside academic studio projects

